


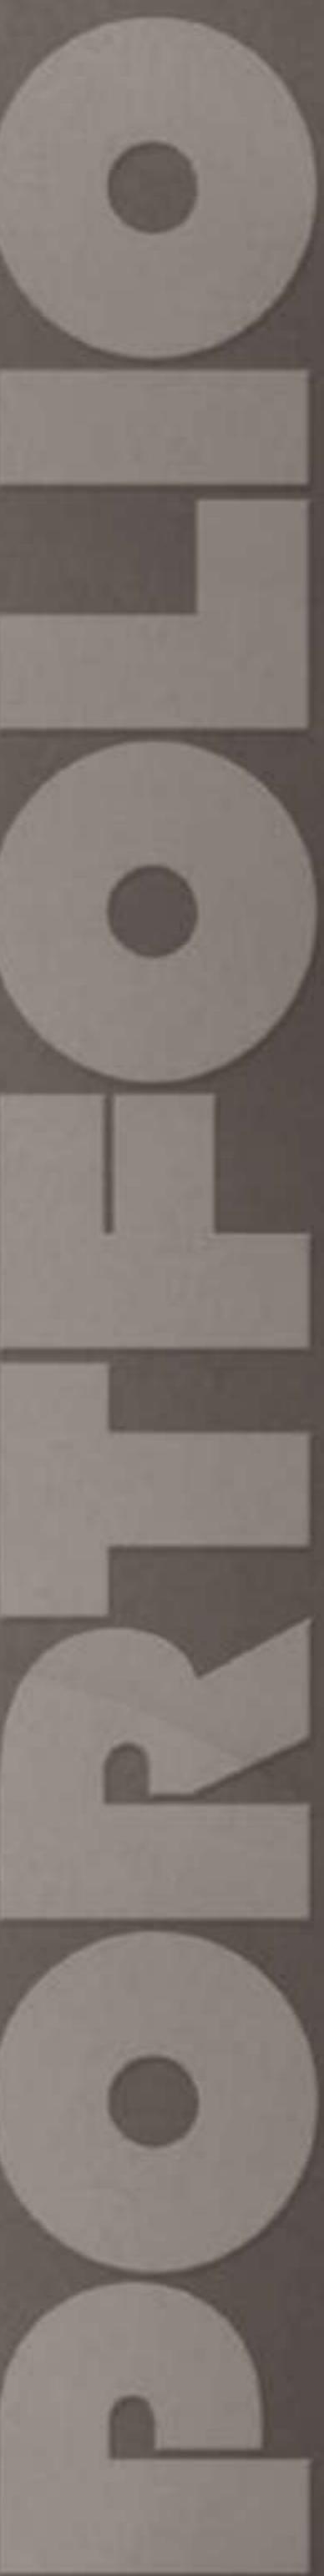

USAID BHATI

**ARCHITECTURAL
STRUCTURE**



DEAR SIR/MADAM,

I, USAID FAROOQ BHATI, CURRENTLY IN FOURTH YEAR, B. ARCH, ALLANA COLLEGE OF ARCHITECTURE, SAVITRIBAI PHULE PUNE UNIVERSITY, WISH TO APPLY FOR AN INTERN'S POSITION IN YOUR FIRM. MY SKILL AND ABILITIES WILL SURELY ADD SOMETHING TO YOUR ALREADY ESTEEMED FIRM. I AM EXTREMELY EXCITED TO WORK IN YOUR OFFICE AS YOUR PROJECT AND DESIGN STYLE MATCHES MY INTEREST. I WISH TO BUILD UP AND ENHANCE MY SKILLS IN TERMS OF DESIGNING FOR ARCHITECTURE IN PRACTICE. I WOULD CONSIDER IT AN HONOUR TO GET AN OPPORTUNITY TO WORK AT YOUR FIRM.

THE DURATION OF INTERNSHIP REQUIRED IS 120 WORKING DAYS. I CAN JOIN AS SOON AS THE CURRENT SEMESTER ENDS I.E IN SECOND WEEK OF MAY 2018.

MY CV AND PORTFOLIO ARE ATTACHED HEREWITH FOR YOUR KIND PERUSAL. THANKYOU FOR REVIEWING THIS LETTER & KINDLY GO THROUGH MY PORTFOLIO.

I HOPE TO RECEIVE A POSITIVE REPLY FROM YOU.

THANKING YOU,

USAID BHATI.



USAID BHATI TO BE ARCHITECT



PROFILE

AS A STUDENT OF ARCHITECTURE, I HAVE LEARNED THE EXTENT TO WHICH OUR WORLD NEEDS TO BE DESIGNED WITH CARE FOR THE END USER AND CONCERN FOR THE PROCESS. I BELIEVE THAT DESIGN CAN MAKE A DIFFERENCE AND CREATIVE SOLUTIONS CAN BE ACHIEVED FOR SOME OF THE WORLD'S LARGEST MODERN ISSUES AND I ASPIRE TO BE PART OF THAT CHANGE.



HARD FACTS

AGE 25

NATIONALITY INDIAN

LANGUAGES ENGLISH (UPPER INTERMEDIATE)
HINDI, URDU, MARATHI.



CONTACT

ADDRESS 316, SATHE COMPLEX, OLD MOTOR STAND, PUNE 411042.

E-MAIL bhatiusaid@gmail.com

PHONE 00918668536406



SKILLS

CREATIVITY



TEAMWORK



LOYALTY



COMMUNICATION



EDUCATION

- **S.S.C (10 TH STD)** // March 2008.
KOLHAPUR BOARD.
PERCENTAGE - 66.46%
VIDYA NIKETAN HIGH SCHOOL, PANCHGANI.
- **H.S.C (12 TH STD)** // Feb 2010.
KOLHAPUR BOARD.
PERCENTAGE- 59%
VIDYA NIKETAN JUNIOR COLLEGE, PANCHGANI.
1ST RANK IN AIEEE IN COLLEGE.
- **B. ARCH (GRADUATION)** // (JOINED- AUGUST 2010.)
PUNE UNIVERSITY
NATA SCORE- 105 / 200.
CURRENTLY IN FOURTH YEAR.
PARTICIPATED IN- ZONAL NASA COMPETITIONS, SEMINARS, FEED LECTURES.
- **INTERESTS AND ABILITIES.** // SINCE 2010
TO KNOW A MAN, YOU MUST KNOW HIS INTERESTS.
TRAVELLING, ART, DESIGNING, ARCHITECTURE, TREKKING, SPORTS.
VERY EXCITED FOR MAKING NEW FRIENDS AND ABOUT THE NEW OPPORTUNITIES



PROJECTS

FIRST YEAR & SECOND YEAR.

- 1. KIOSK DESIGN & STATIONARY SHOP.
- 2. PRIMARY SCHOOL DESIGN.
- 3. RESIDENTIAL BUNGALOW.
- 4. ART & ARTIFACT MUSEUM DESIGN.

THIRD YEAR & FOURTH YEAR.

- 1. ART GALLERY & CITY LIBRARY
- 2. INTERPRETATION CENTER & WINERY INDUSTRY
- 3. POLICE HOUSING SOCIETY.
- 4. DAIRY INDUSTRY

ON SITE EXPERIENCE.

- 1. RESIDENTIAL BUNGALOW SOCIETY - PANCHGANI.
- 2. HIGH END RESIDENTIAL COMPLEX -BANDRA



SOFTWARE

AUTOCAD



PHOTOSHOP



SKETCHUP



ARCHICAD



LUMION



MS OFFICE



LIST OF PROJECTS

DESIGN.

DAIRY INDUSTRY.....(1)

POLICE HOUSING.....(2)

ART GALLERY.....(3)

CITY LIBRARY.....(4)

WINERY INDUSTRY.....(5)

WORKING DRAWING.

BUNGALOW.....(6)

CONSTRUCTION TECHNOLOGY.


INDUSTRIAL SHED.....(7)

DAIRY INDUSTRY.

01



ROAD SIDE ELEVATION


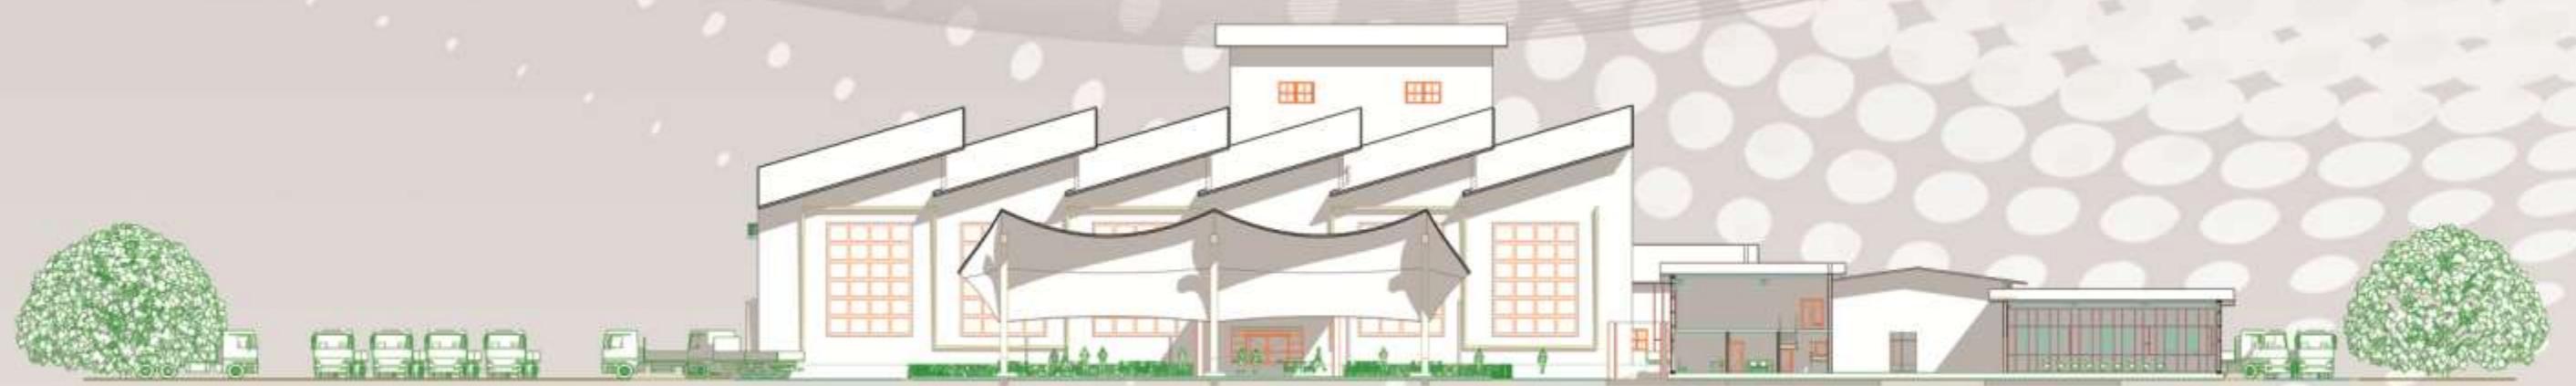


SITE SECTION.


PROJECT- A DAIRY INDUSTRY WAS TO BE DESIGNED AT SHIKRAPUR WITH AN OUTLET FOODCOURT AND FEW GUEST HOUSES BUILUP AREA- 6.1 ACRES.

DESIGN APPROACH- THE FACTORY IS DESIGNED AND SITUATED IN SUCH A WAY THAT IT SEGRIGATES THE SITE INTO TWO PARTS, THE RIGHT PART WITH PUBLIC SPACES CONSISTING OF FOOD COURT, GUEST HOUSES AND THE ADMIN BUILDING WHILE THE LEFT PART OF THE SITE CONSISTING OF SERVICE AREAS. AS THE FACTORY IS PLACED LONGITUDINALLY THE ROOF IS DESIGNED TO BE A TWO WAY SLOPED NORTH ROOF. THE OVERALL DESIGN OF THE FACTORY GIVES A SPEC-TACULAR FACADE VIEW FROM THE ENTRNCE OF THE SITE. A BUFFER SPACE IS PROVIDED BETWEEN THE FACTORY AND THE TENSILE COVERD FOOD COURT. THE GUEST HOUSE IS PLACED AT THE TOP RIGHT CORNER OF THE SITE MAKING IT UNDISTURBED WITH EASY ACCESS.

PRODUCTION FACTORY

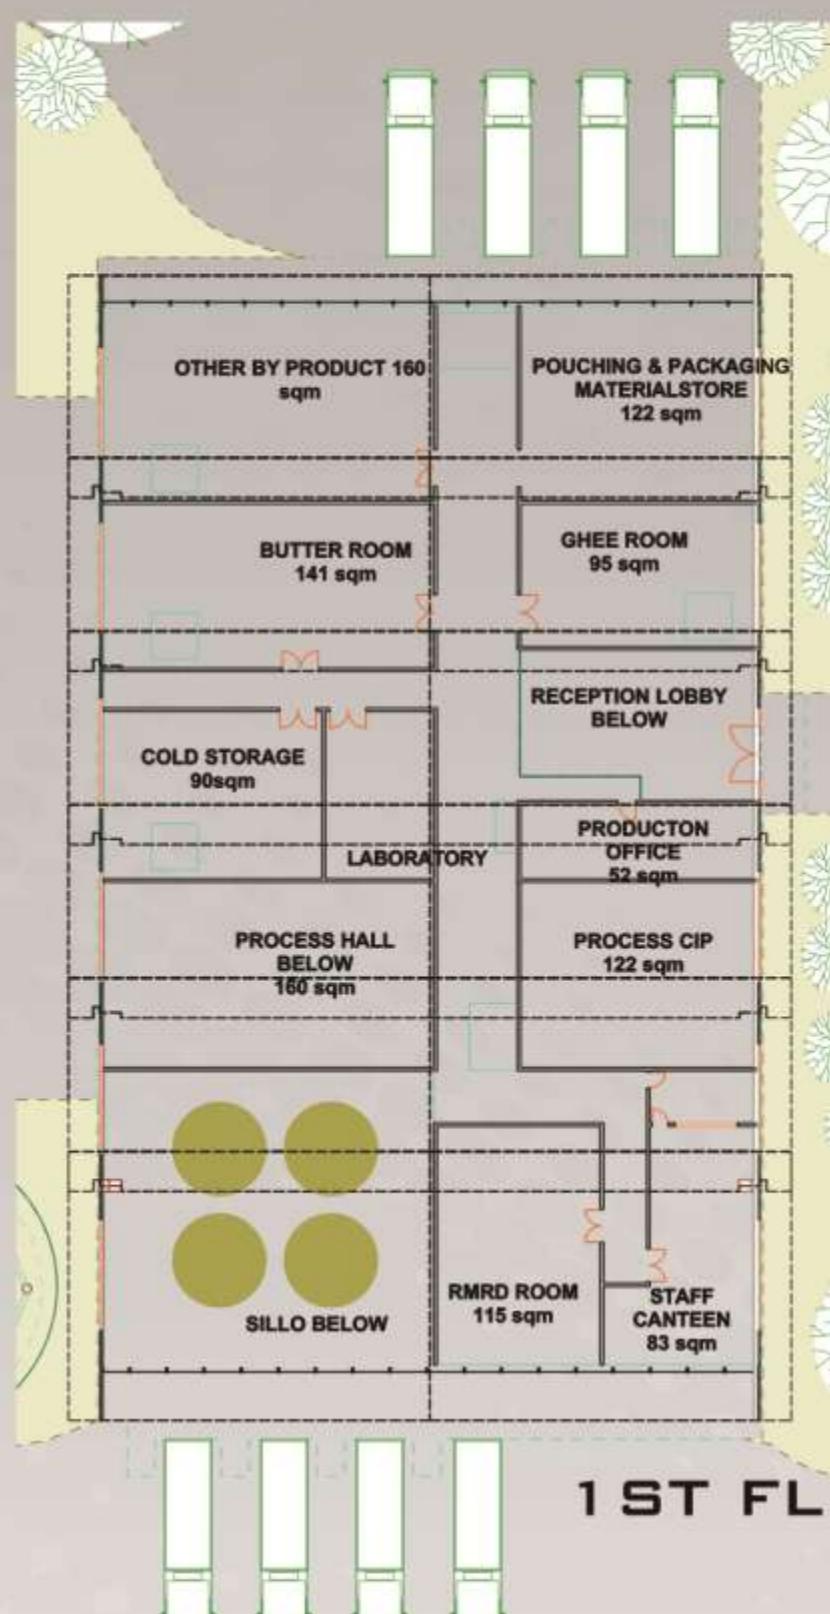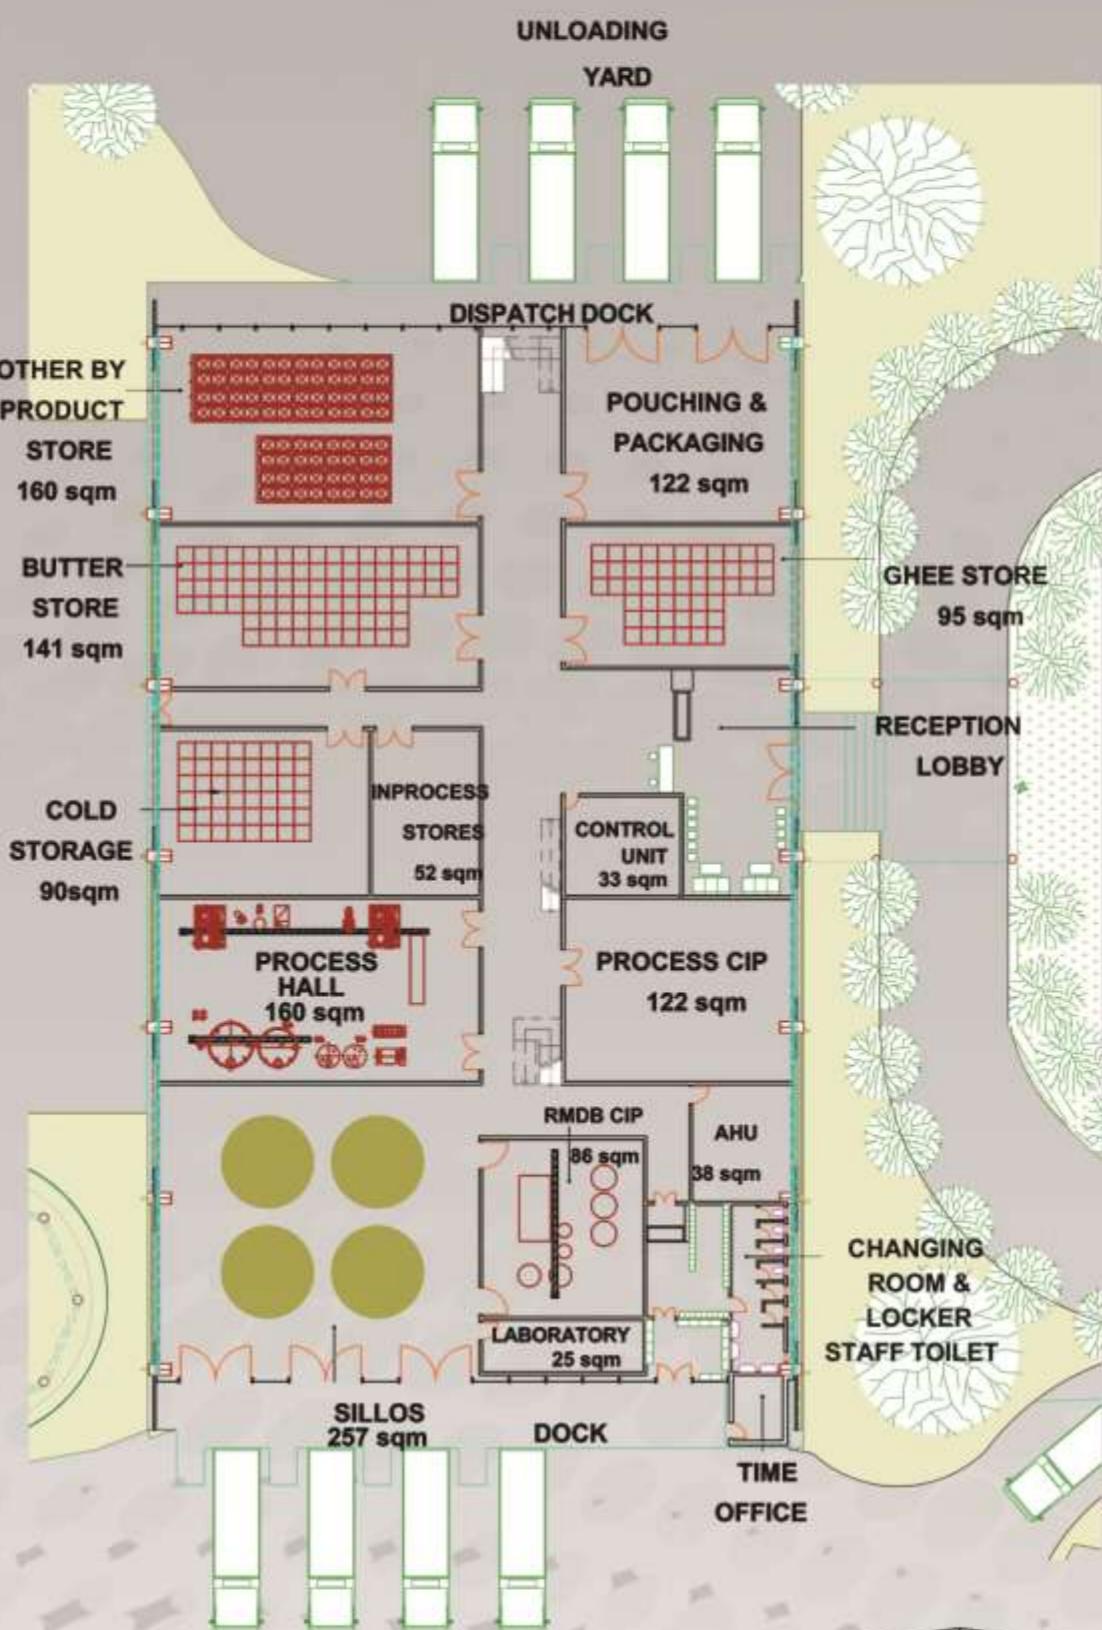

PEB STRUCTURE OF THE FACTORY

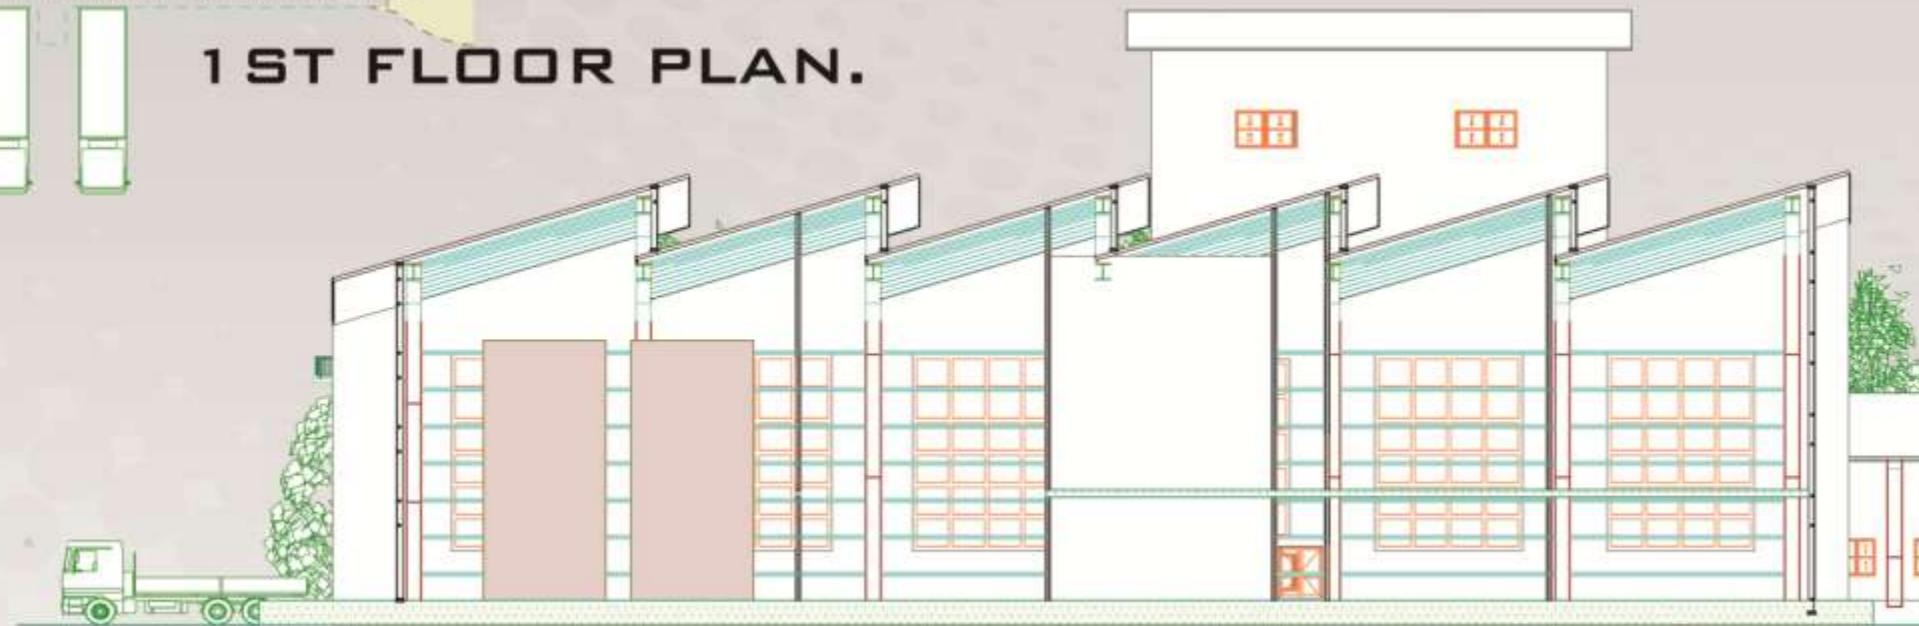


SOUTH SIDE ELEVATION




NORTH SIDE ELEVATION

WEST SIDE ELEVATION

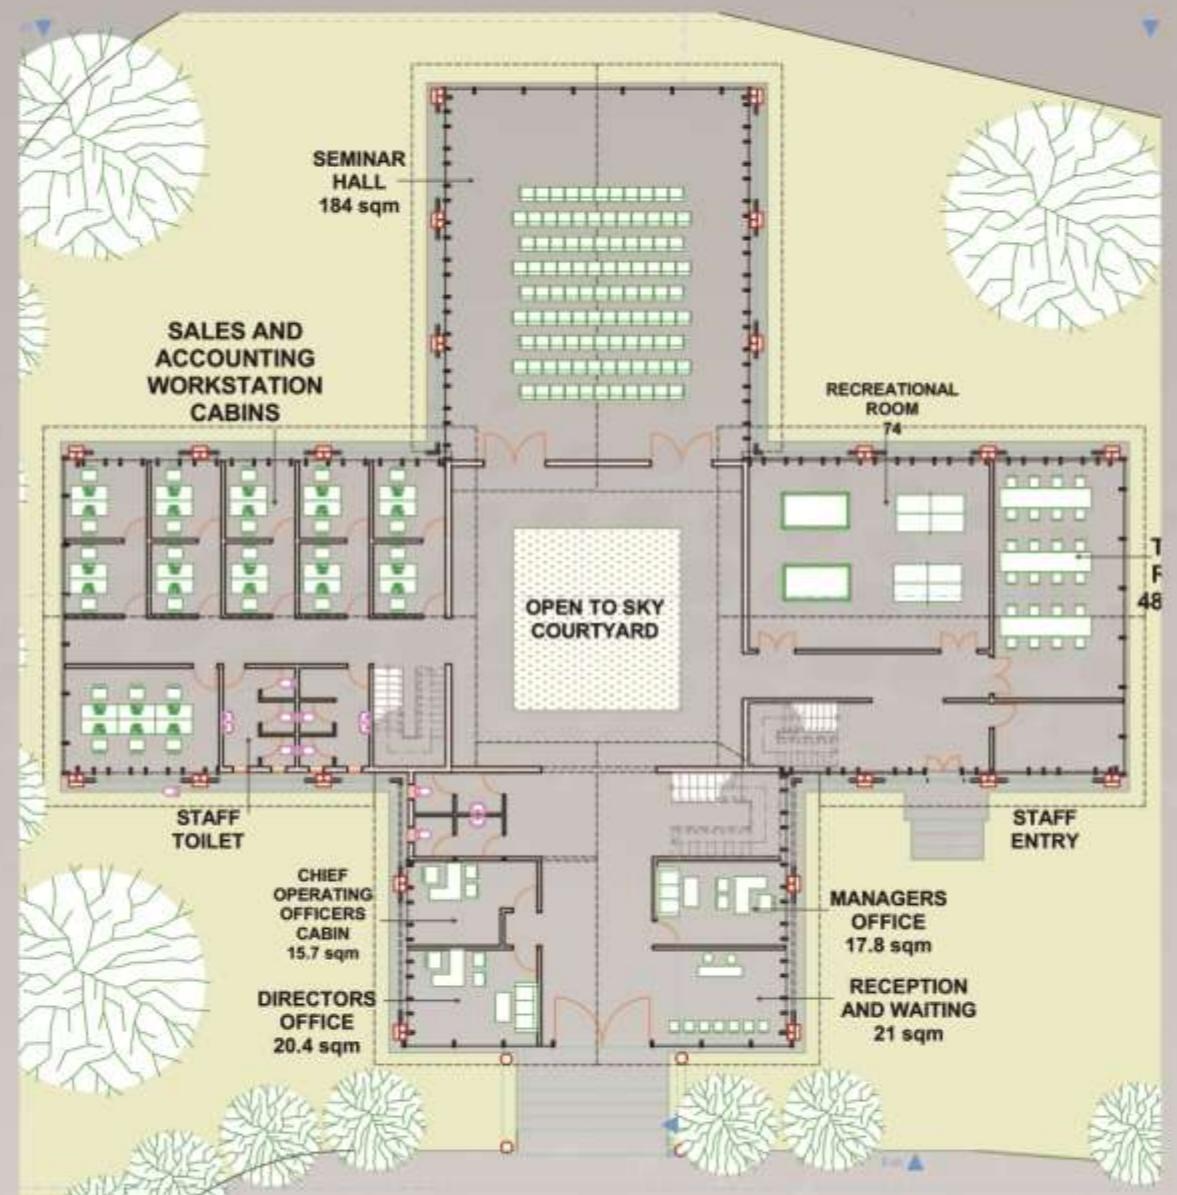


GROND FLOOR PLAN.

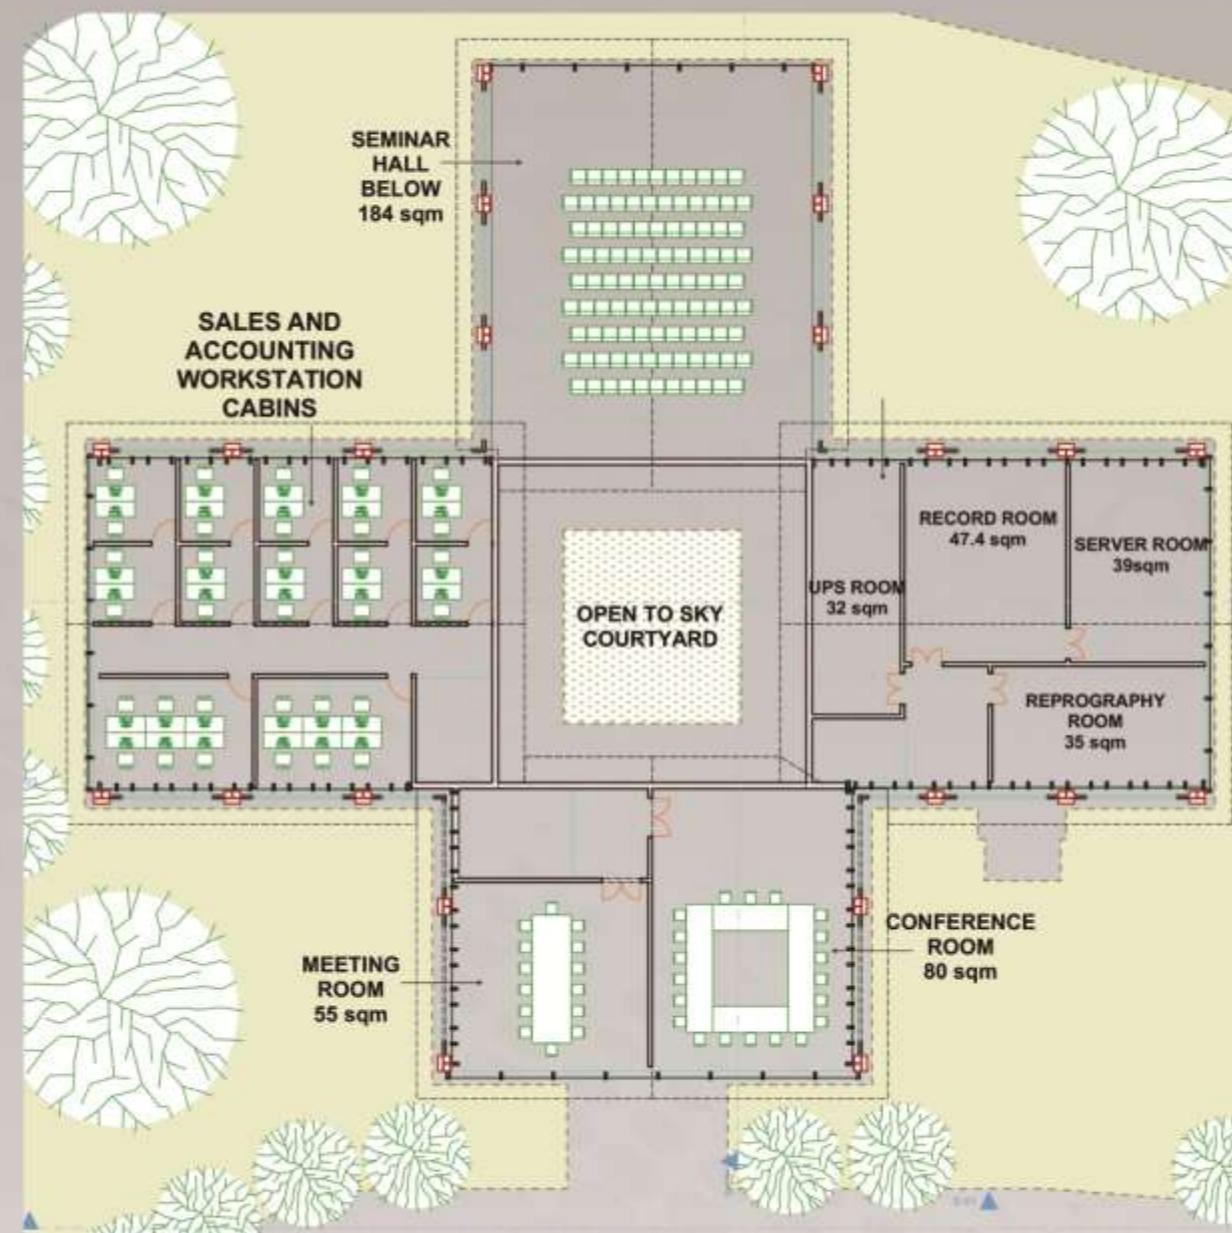

1ST FLOOR PLAN.

ADMINISTRATION BUILDING

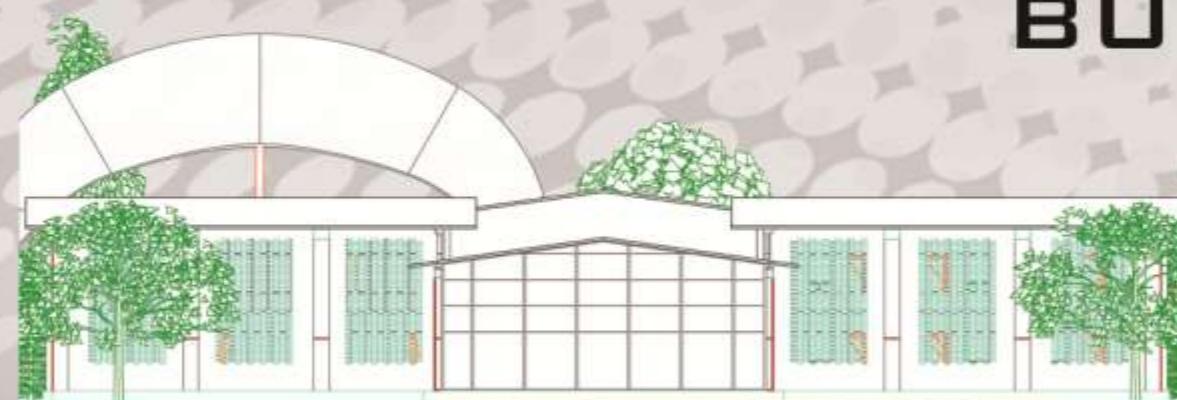


SOUTH SIDE ELEVATION.



SECTION



NORTH SIDE ELEVATION.

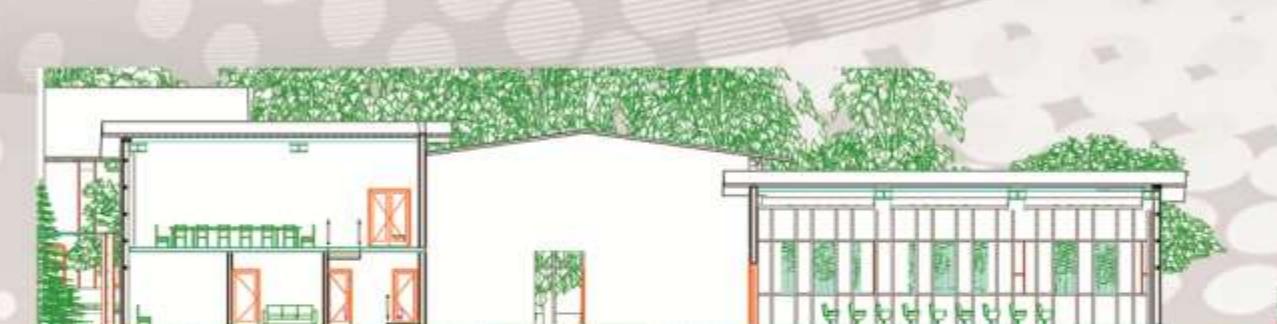

SECTION



1ST FLOOR PLAN SHOWING STELL STRUCTURE



BIRD EYE VIEW OF THE ADMIN FOOD COURT AND THE FACTORY


SITE VIEW AND MODEL PICTURES

04



POLICE HOUSING SOCIETY

05

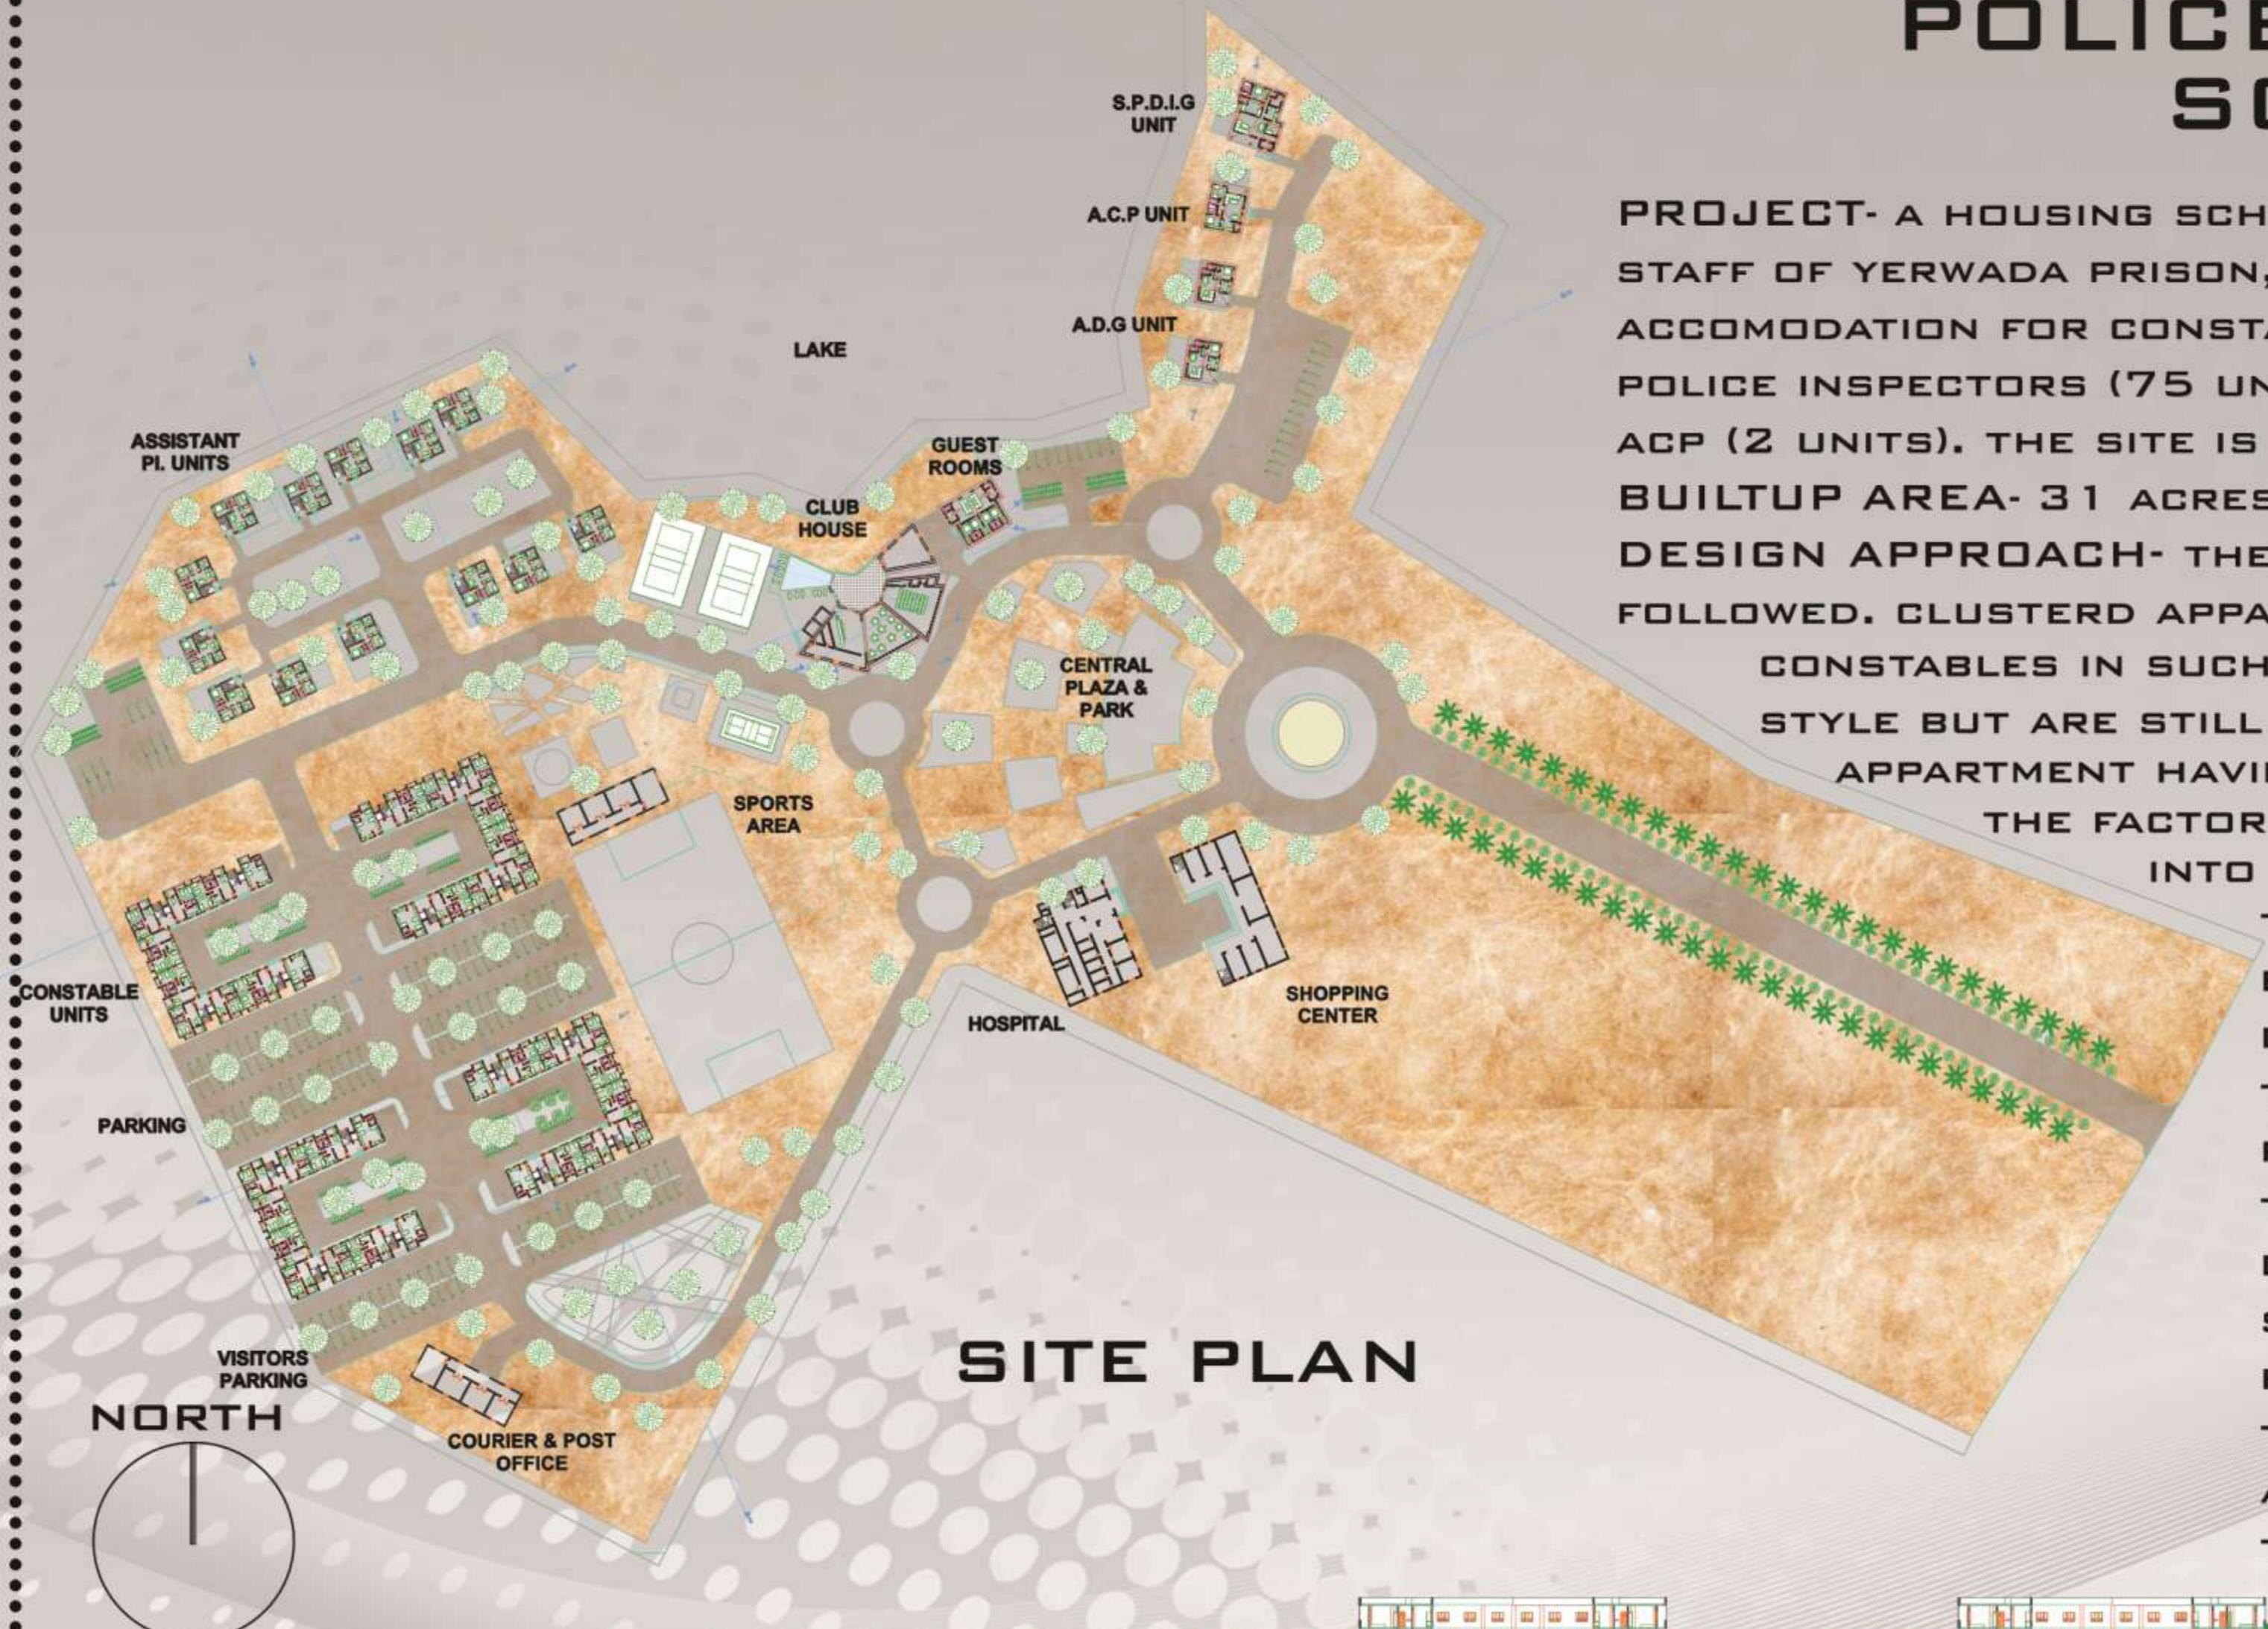

SITE PLAN

PROJECT- A HOUSING SCHEME, PROPOSED FOR THE PRISON STAFF OF YERWADA PRISON, PUNE. IT WILL PROVIDE ACCOMODATION FOR CONSTABLE INSPECTORS (220 UNITS), ASS. POLICE INSPECTORS (75 UNITS), ADG (1 UNIT), SP. DIG (1 UNT), ACP (2 UNITS). THE SITE IS ADJACENT TO YERWADA PRISON. BUILTUP AREA- 31 ACRES.

DESIGN APPROACH- THE FACTOR OF COMMUNITY LIVING IS FOLLOWED. CLUSTERD APPARTMENT BUILDINS ARE DESIGNED FOR CONSTABLES IN SUCH A WAY THAT THEY MADE IN A CHAWL STYLE BUT ARE STILL COMPLETELY PRIVATE WITH EACH APPARTMENT HAVING WINDOWS ON BOTH THE SIDE AND THE FACTOR OF DEFENSIBLE SPACES IS TAKEN INTO CONSIDERATION WHILE DESIGNING.


THE ASS. PI UNITS ARE DESIGNED TO BE DUPLEX ROW HOUSES WITH DECENT PRIVACY.

THE ADG, SP.DIG AND ACP UNITS ARE PLACED ON THE LAKE SIDE PART OF THE SITE. A PARK AND PLAZA IS DESIGNED IN THE CENTER OF THE SITE WITH A CLUB HOUSE AND UEST HOUSES ADJOINING THE PARK FACING THE LAKE. VARIOUS SPORT FIELDS ARE PROVIDE WITH JOGGING PARK AT THE ENTRANCE OF THE SITE.



SITE SETION


ASSISTANT PI. UNIT.

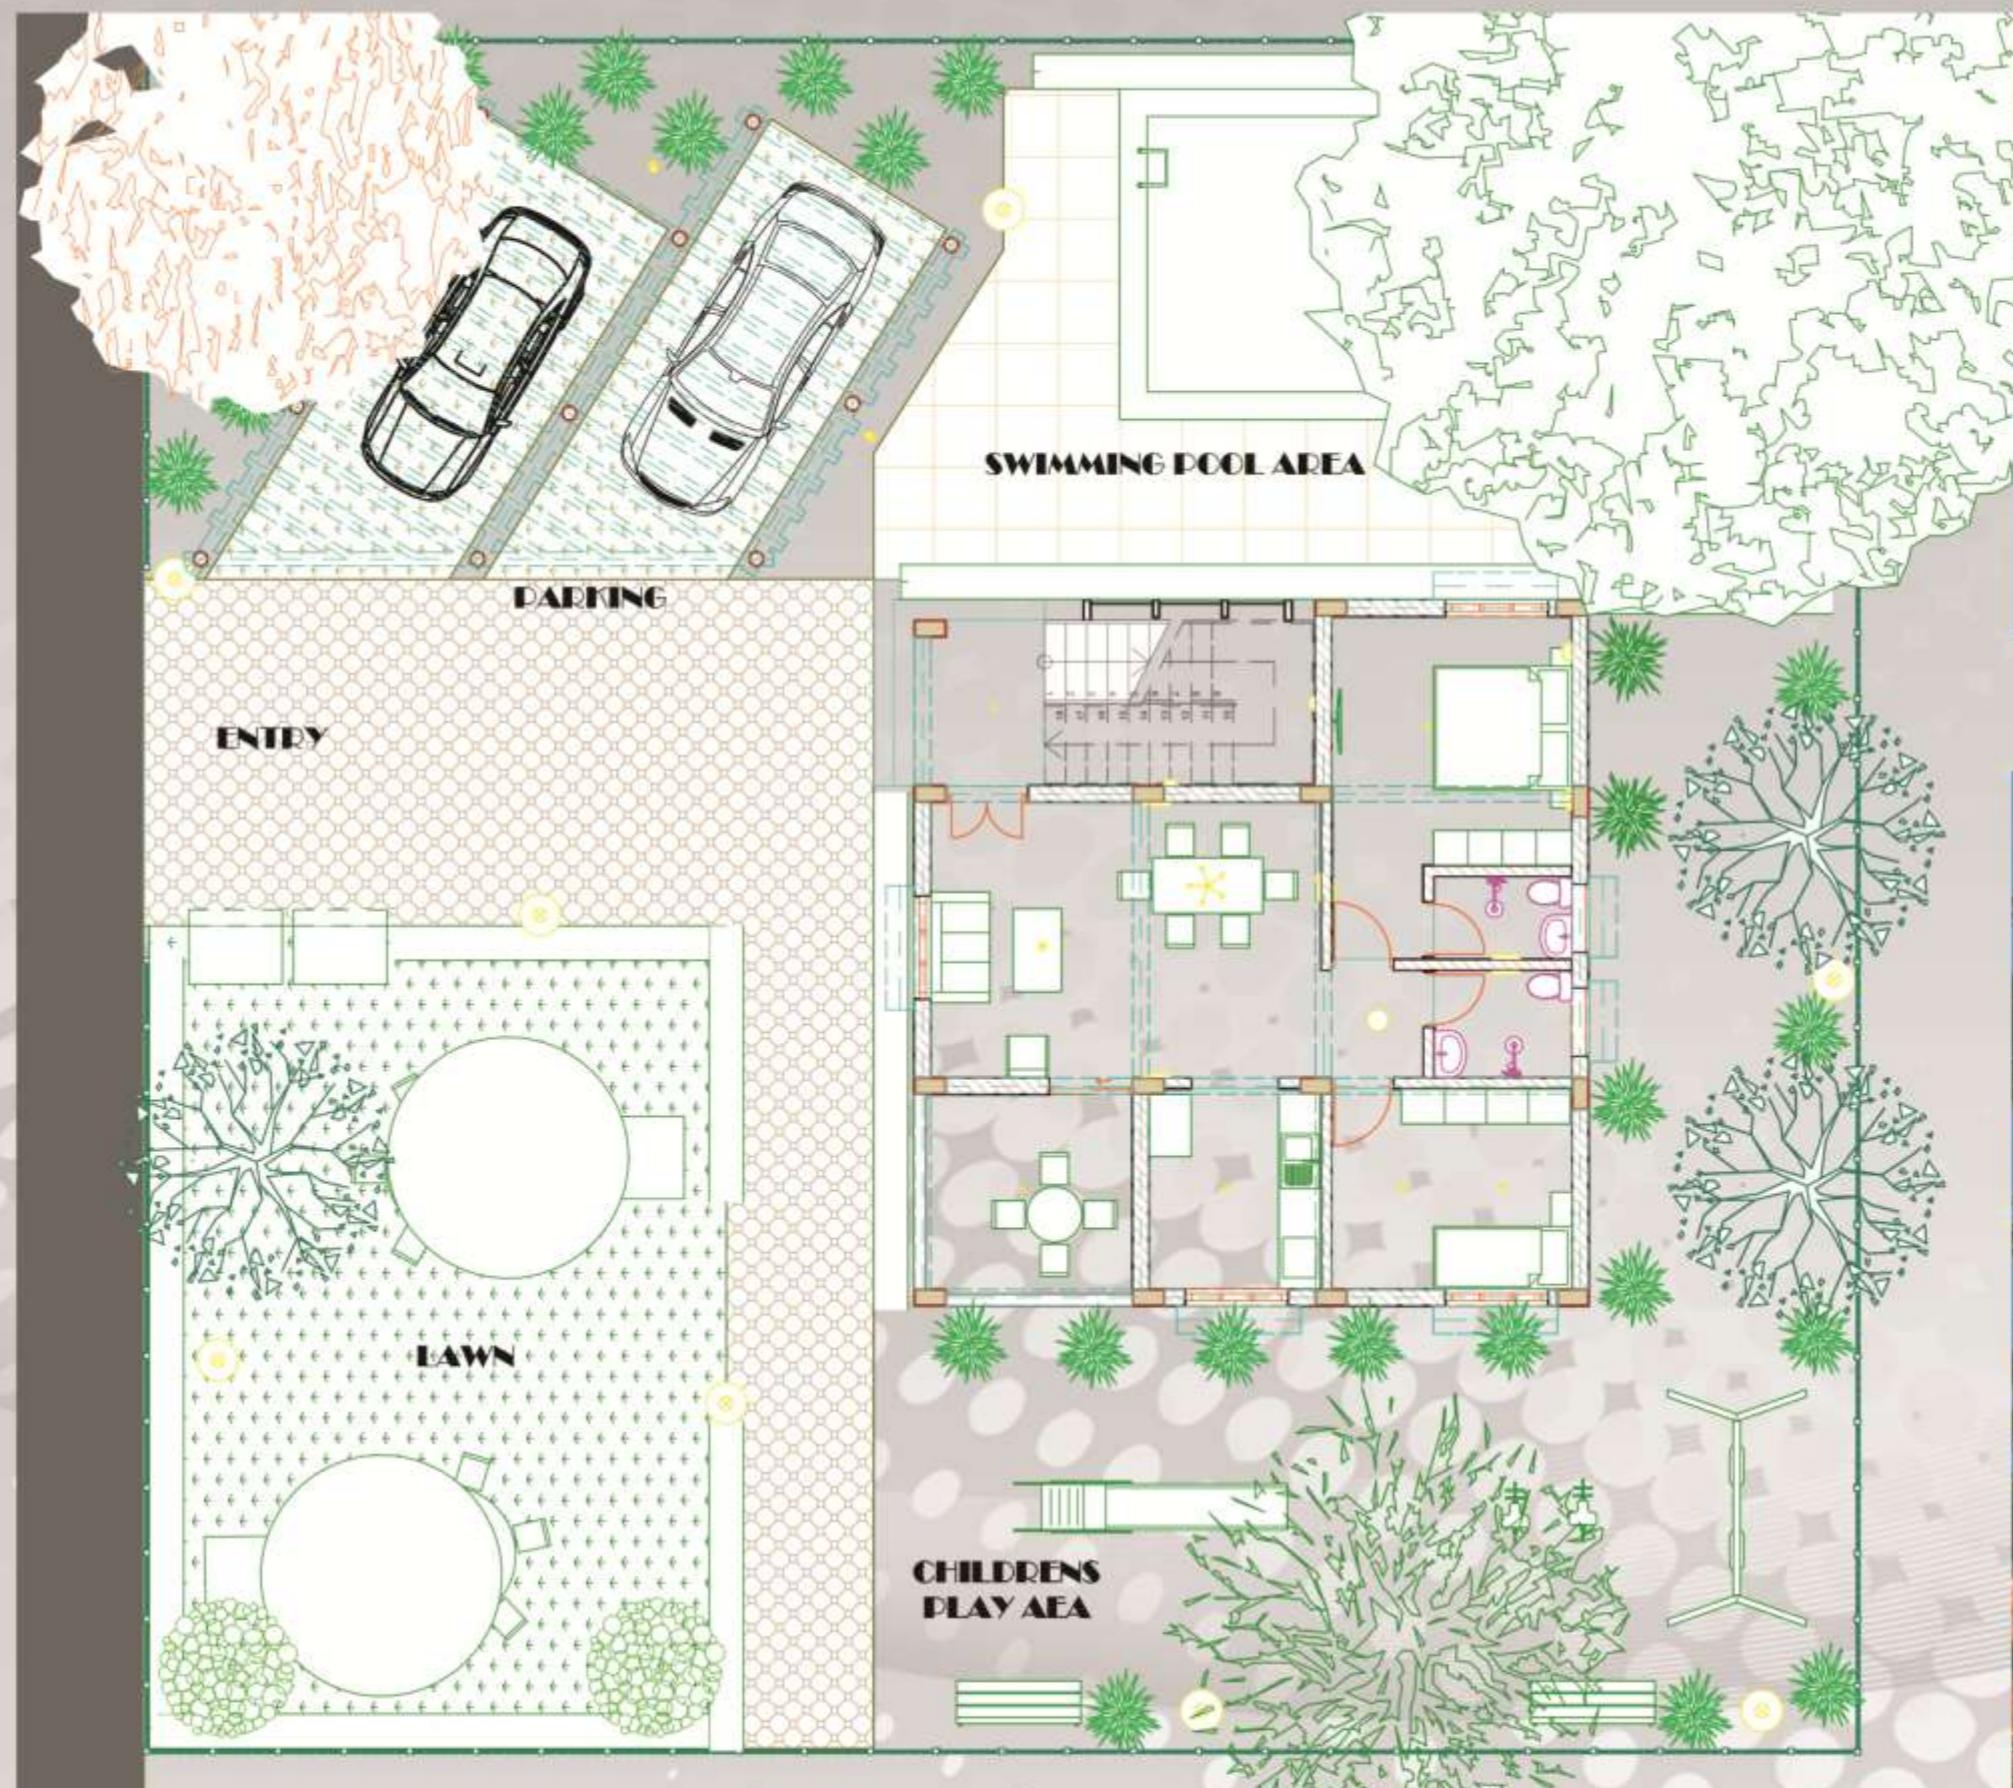

SITE DEVELOPMENT



DAY AND NIGHT VIEW

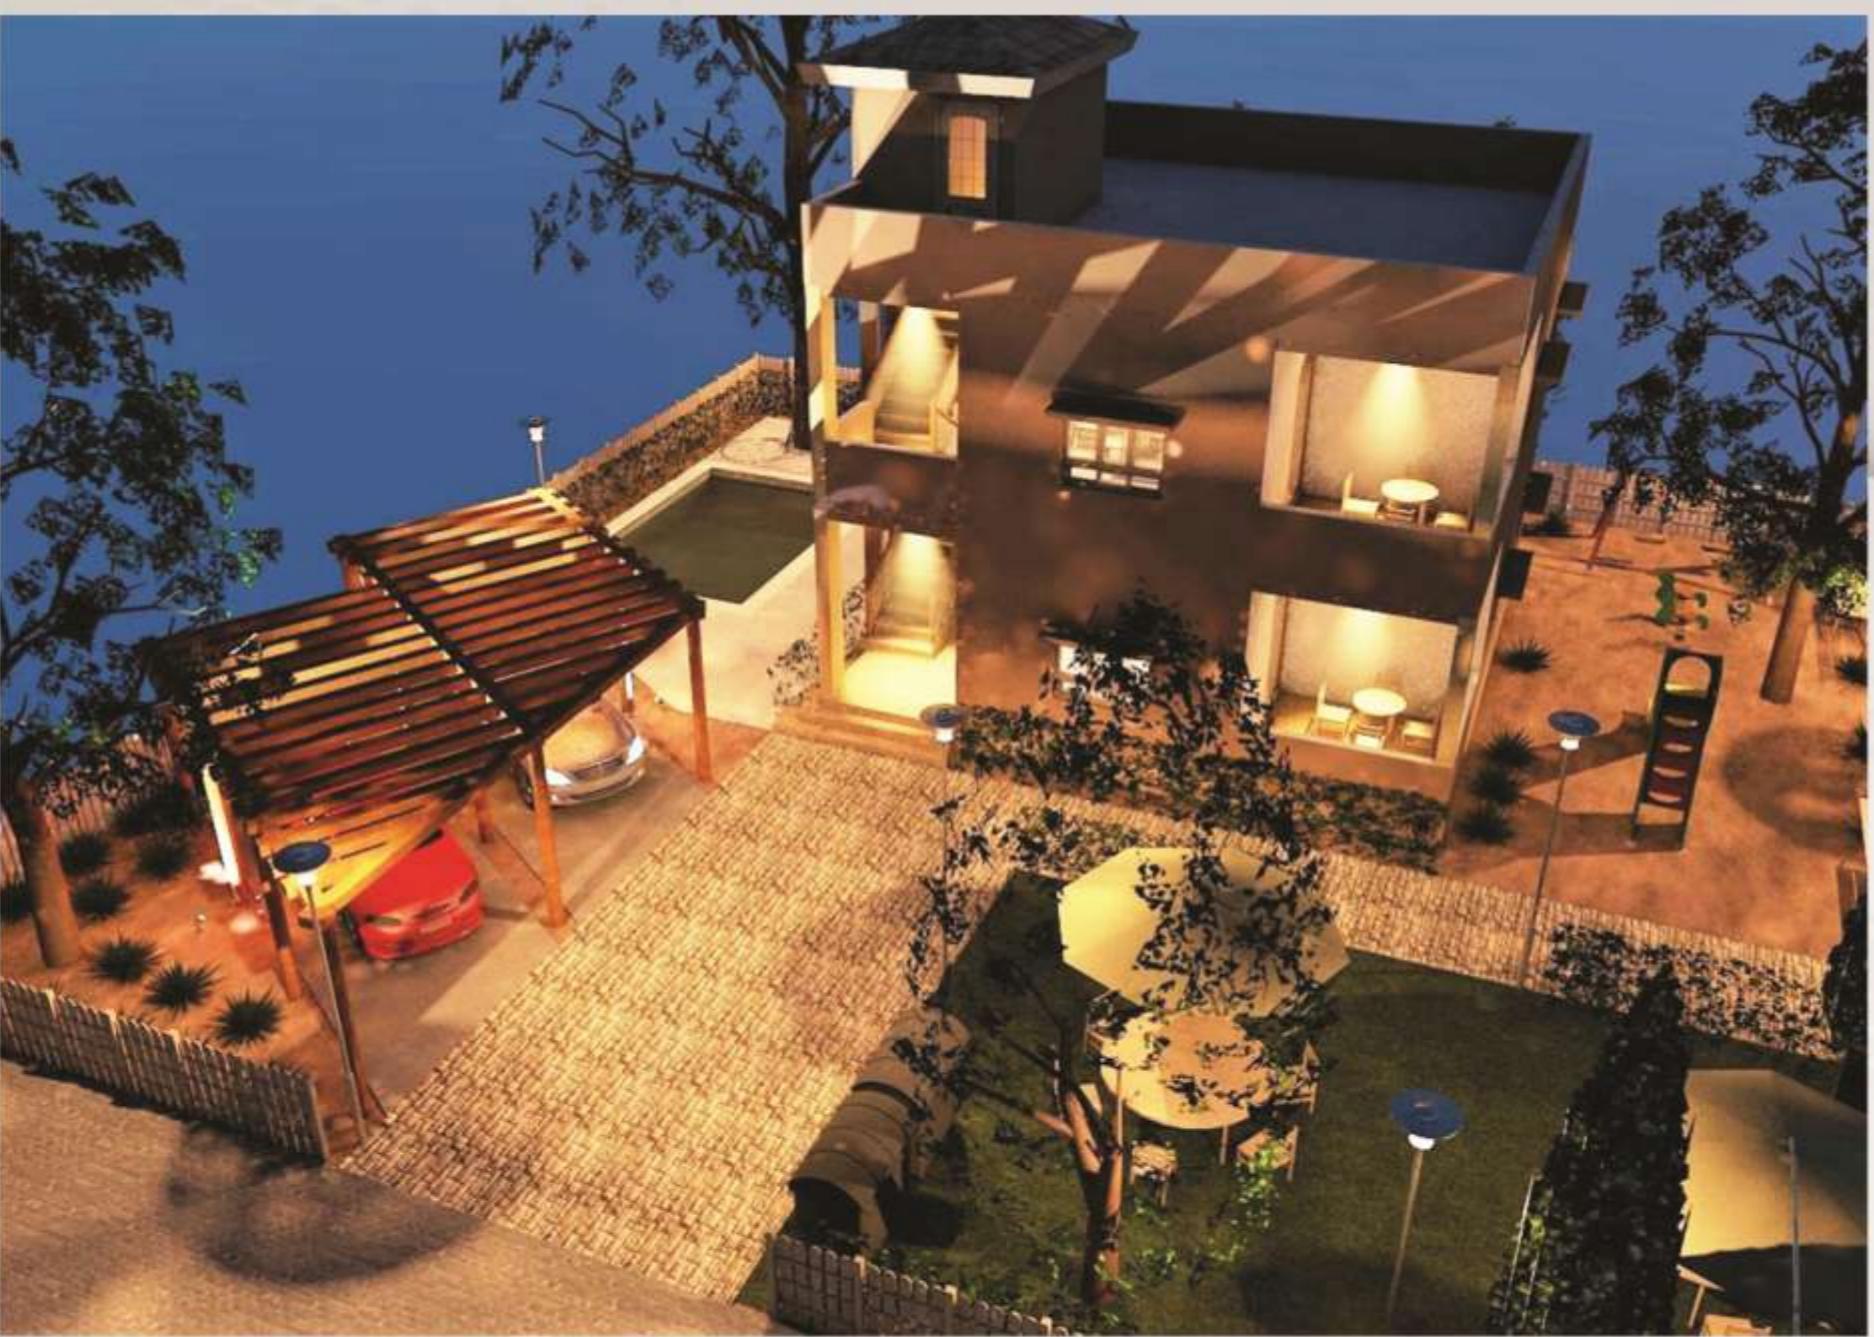



SOUTH ELEVATION




WEST ELEVATION




SECTION S-01



SECTION S-02

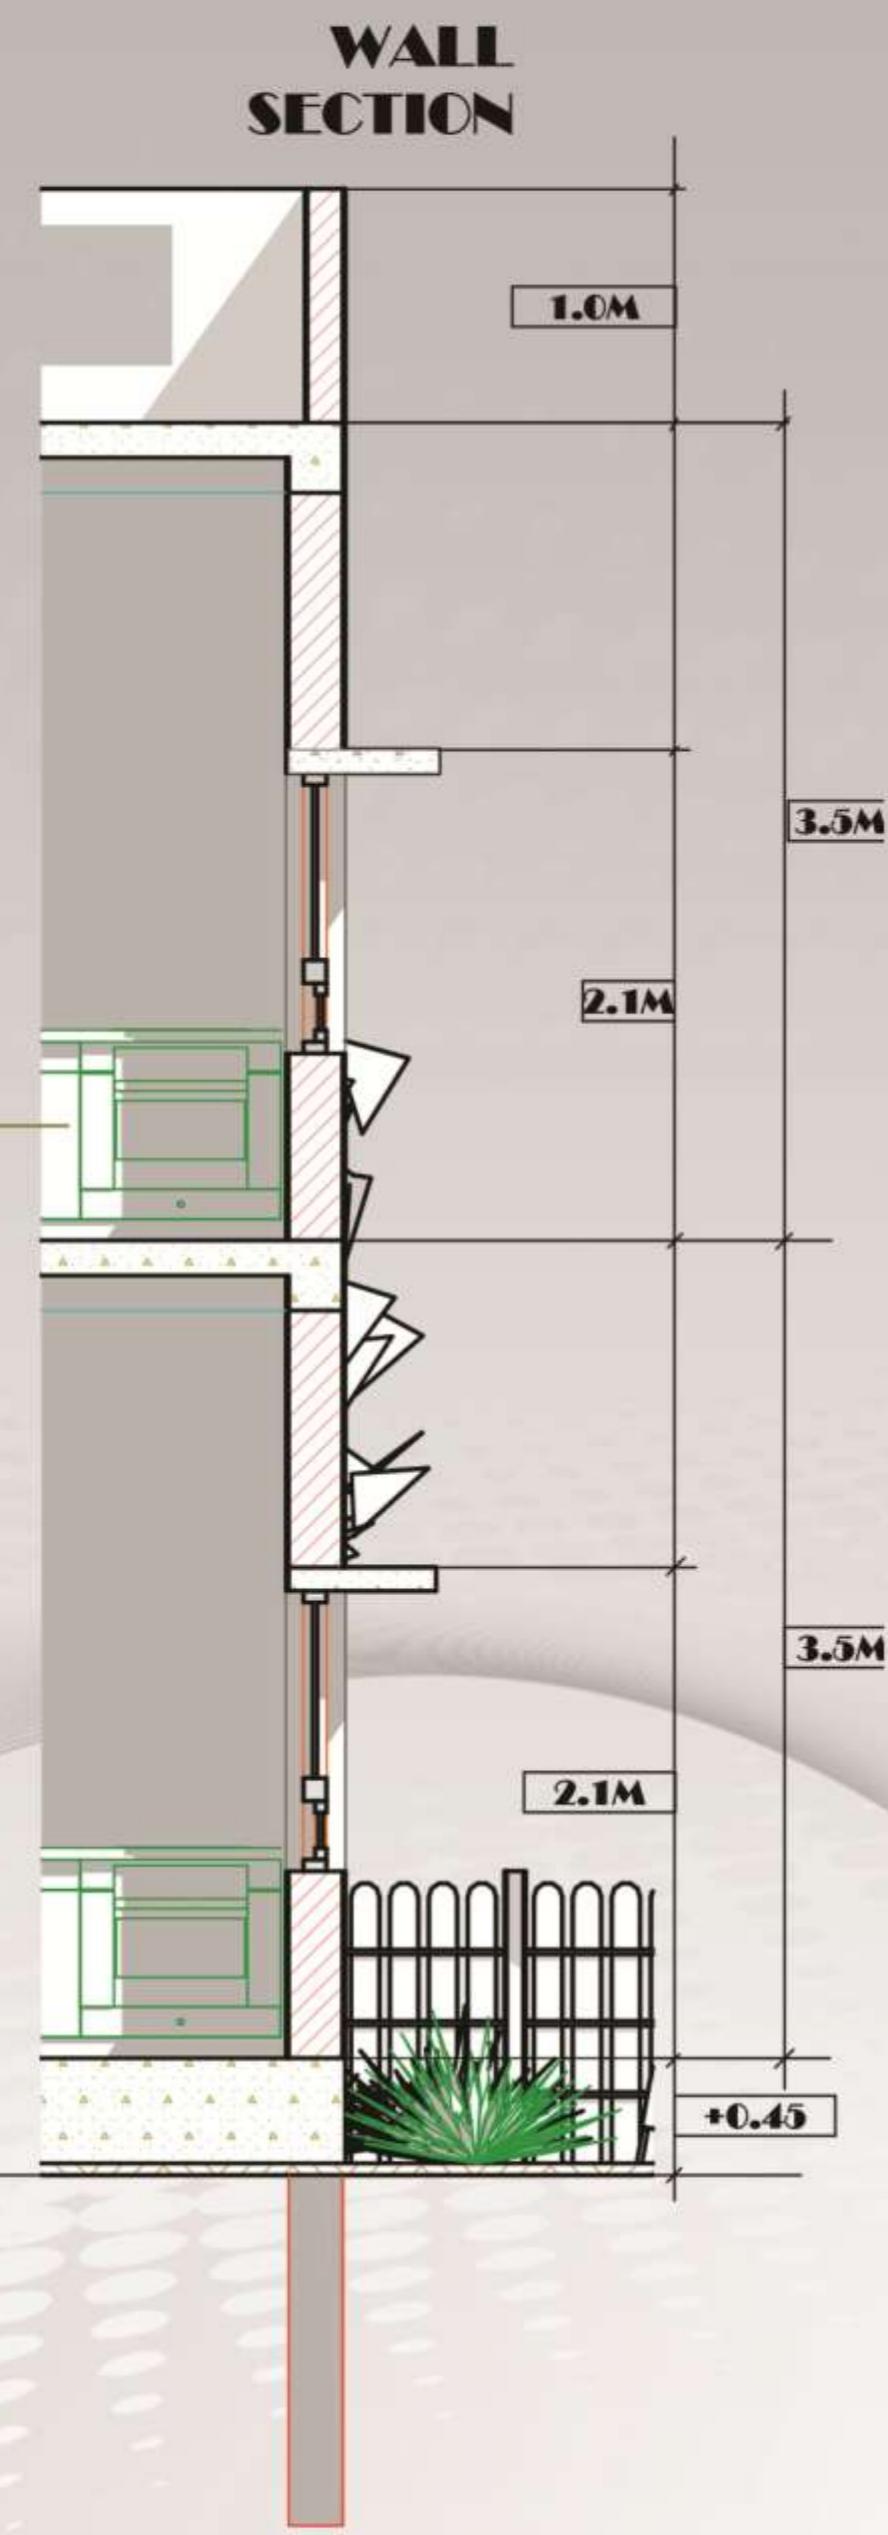


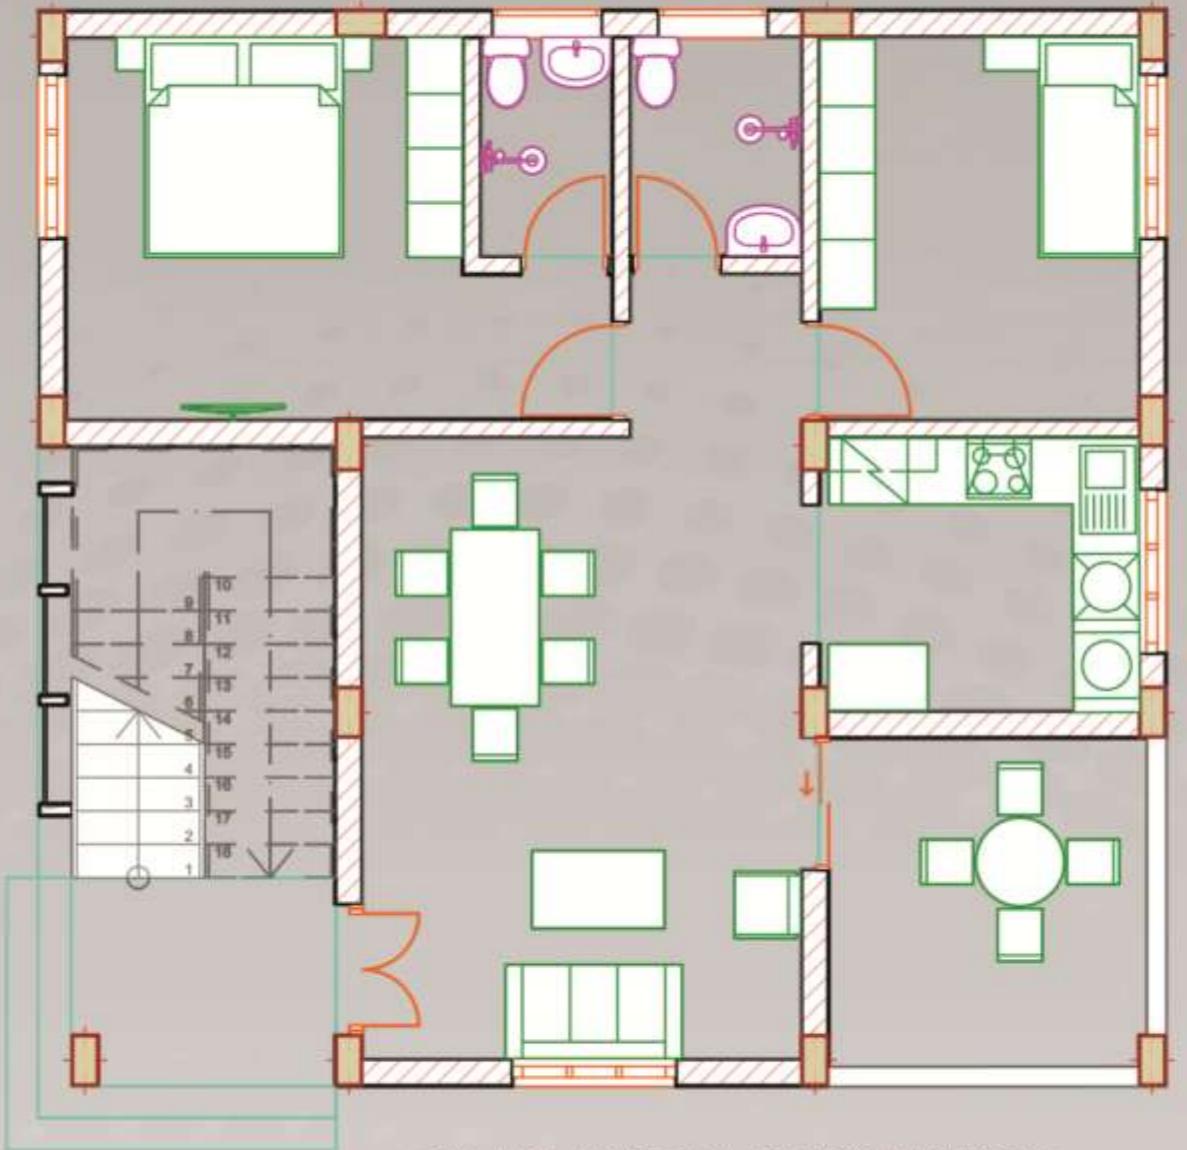

PLAN WITH FURNITURE



ZONAL PLAN

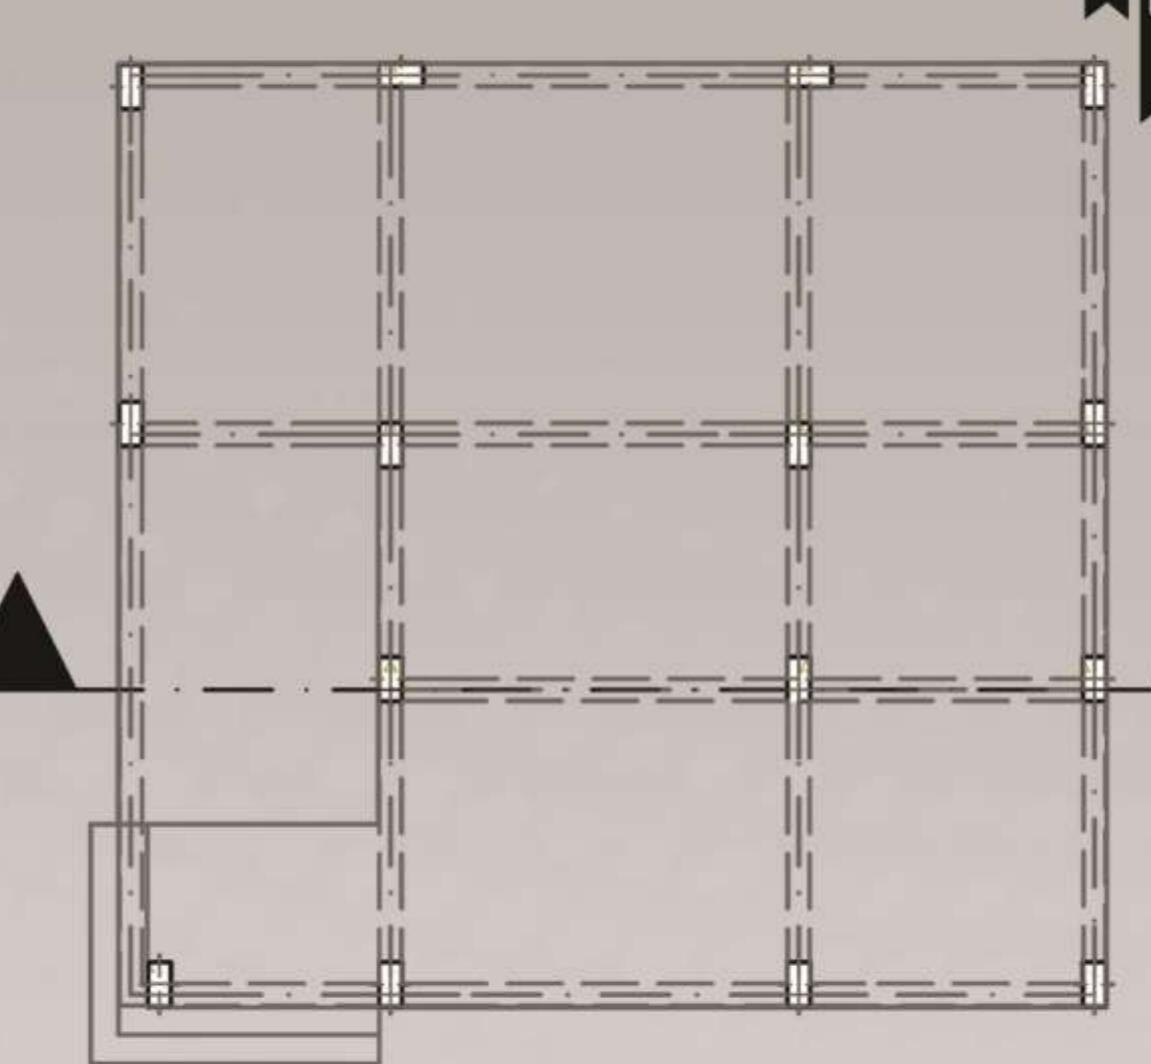


STRUCTURAL PLAN




INTERIORS



STRUCTURAL
VIEW

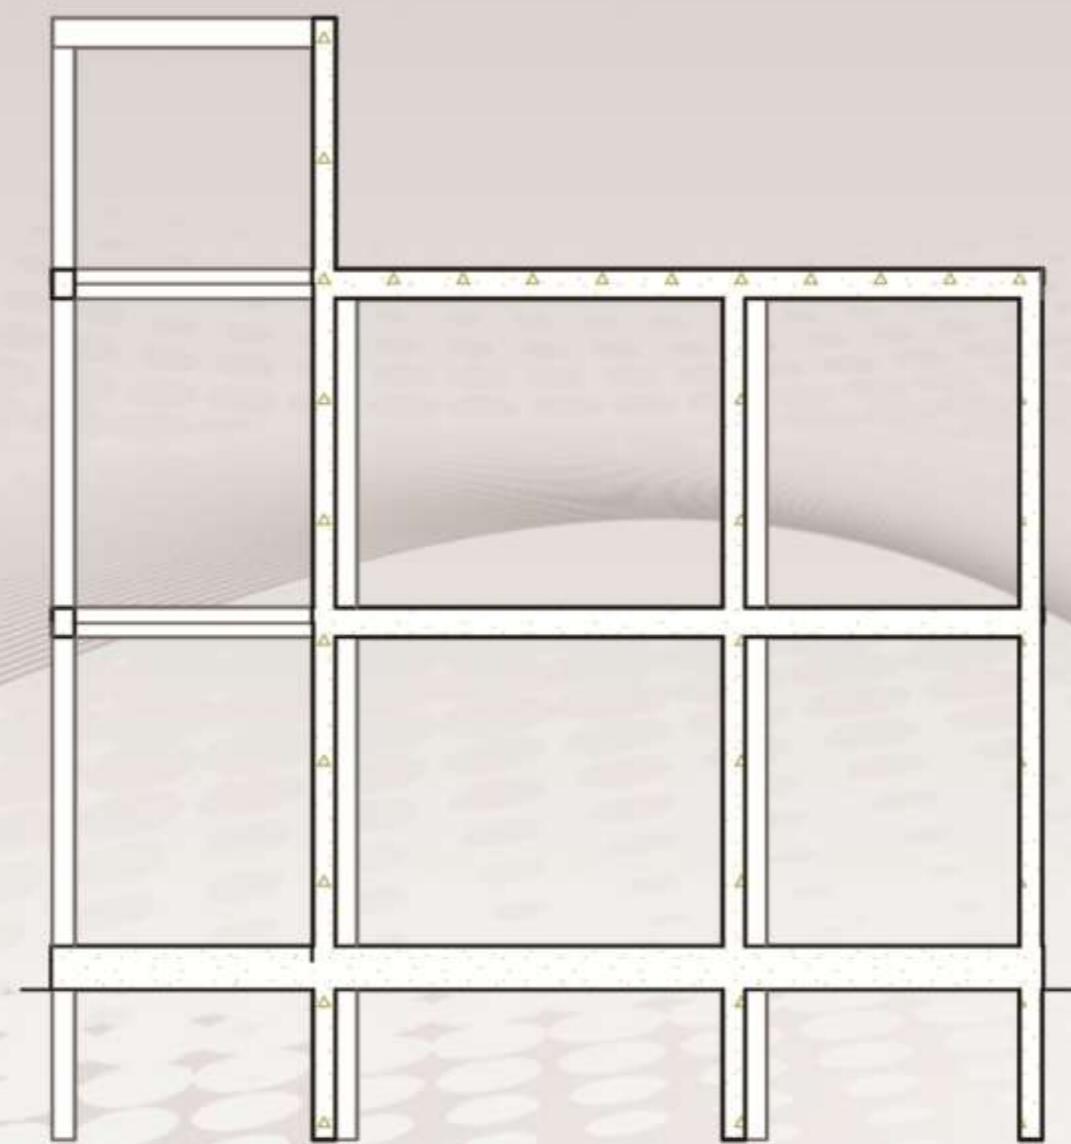

SECTION

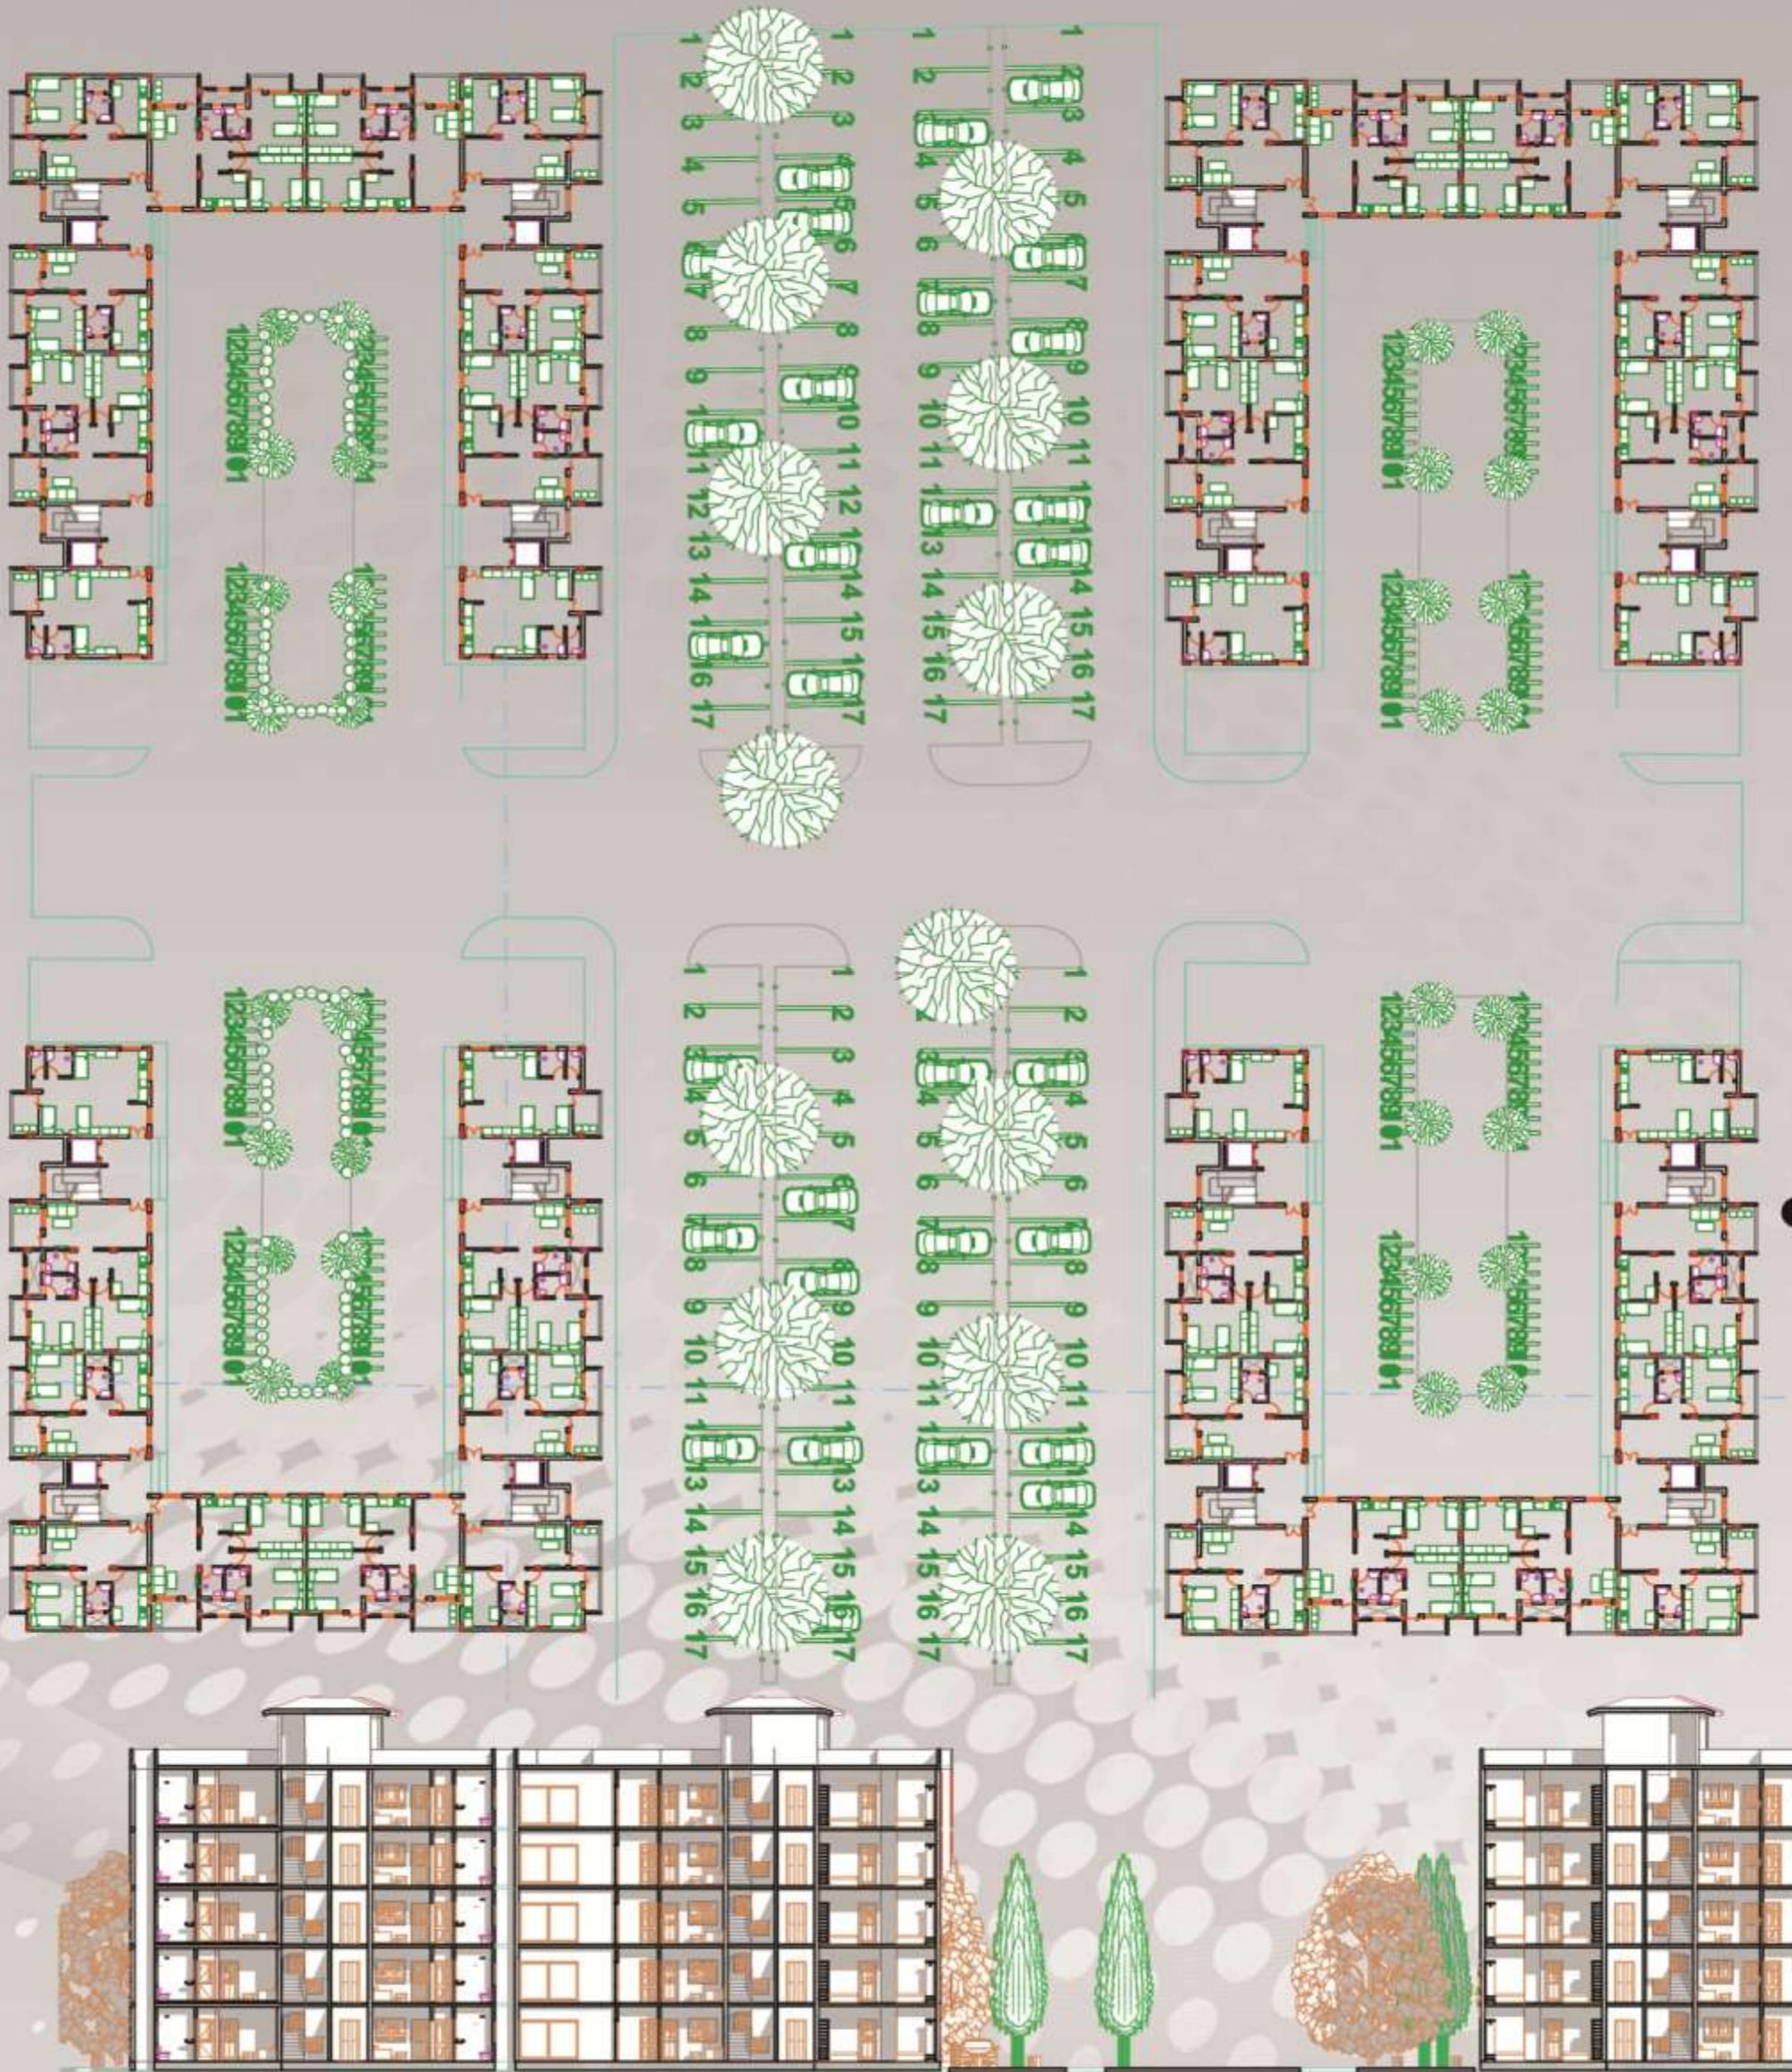

CLUSTER SECTION


CLUSTER ELEVATION

**CONSTABLE
UNITS.
CLUSTER
PLAN.**

**VIEW FROM A
WINDOW**




BIRD EYE VIEW

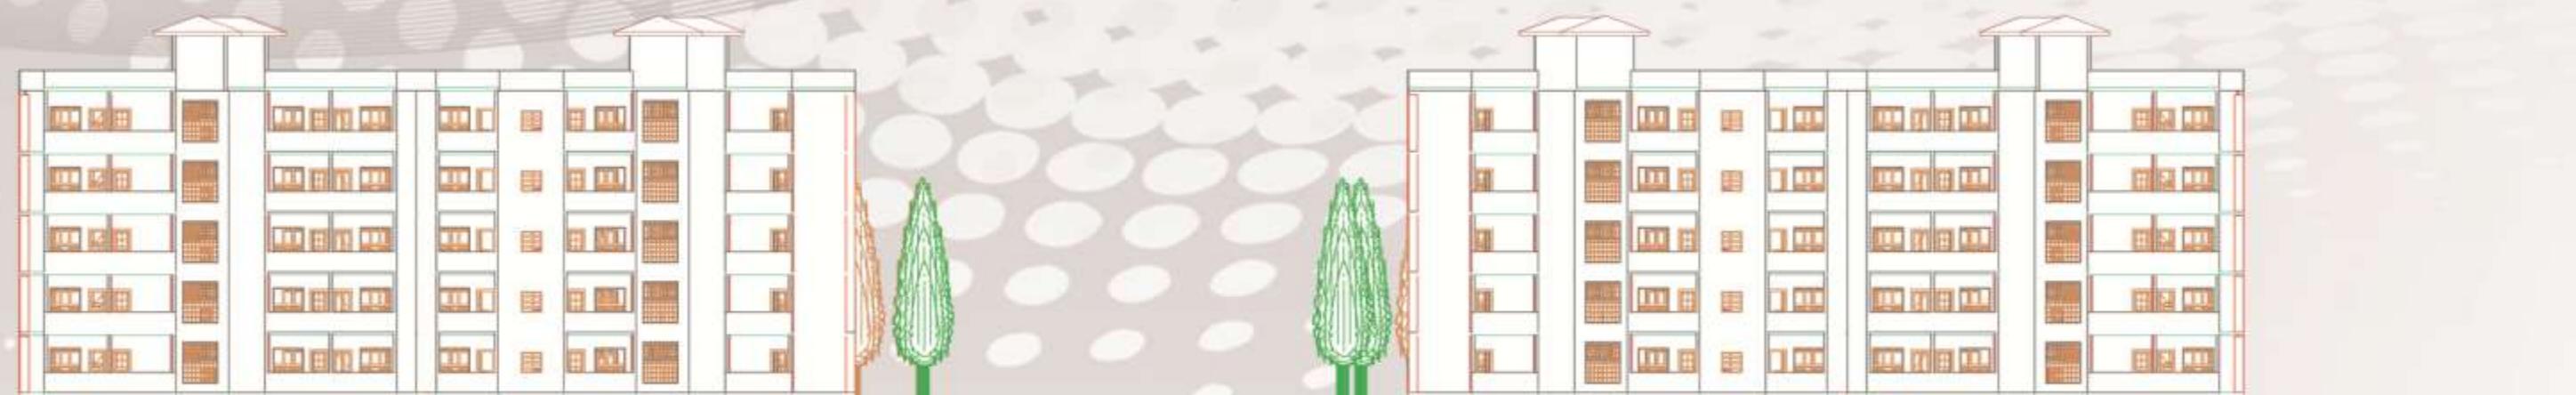


ART GALLERY.

**PROJECT- AN ART GALLERY WITH A PUBLIC
PLAZA FOR PUNE CITY IN ONE OF ITS MOST PRIME
LOCATIONS, BUND GARDEN ROAD
BUILTPUP AREA- 3214 SQ.M**







DESIGN APPROACH- THE AIM OF THIS DESIGN WAS TO HOLD TIGHTLY TO THE CULTURAL HERITAGE OF THE CITY WHICH IS BEING LOST IN THE PROGRESSIVE LIFESTYLE OF TODAY. THE CHAOTIC SPACES ARE HELD TIGHTLY BY A RIGID SQUARE WHICH DOES NOT LET THE CHOS OUT.

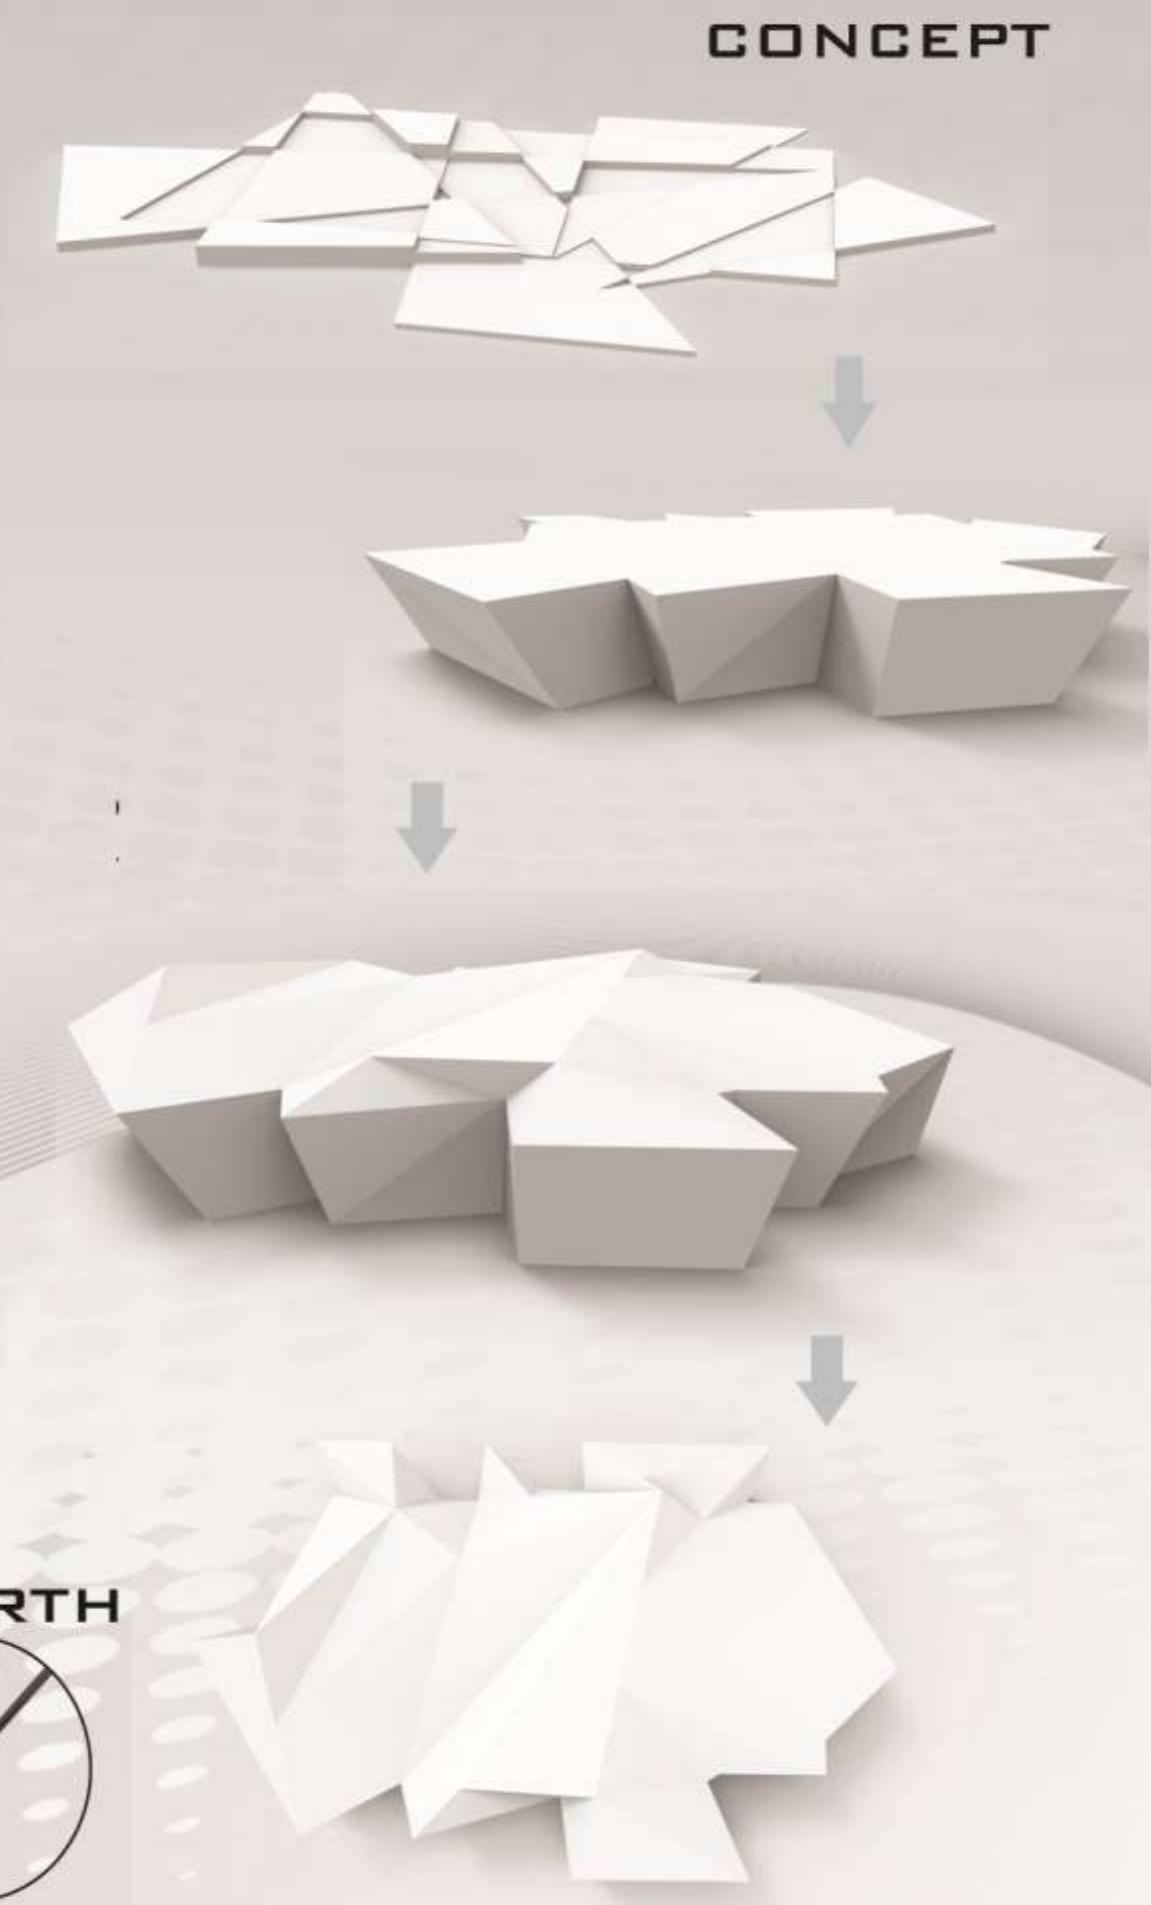

SITE PLAN- ART GALLERY.

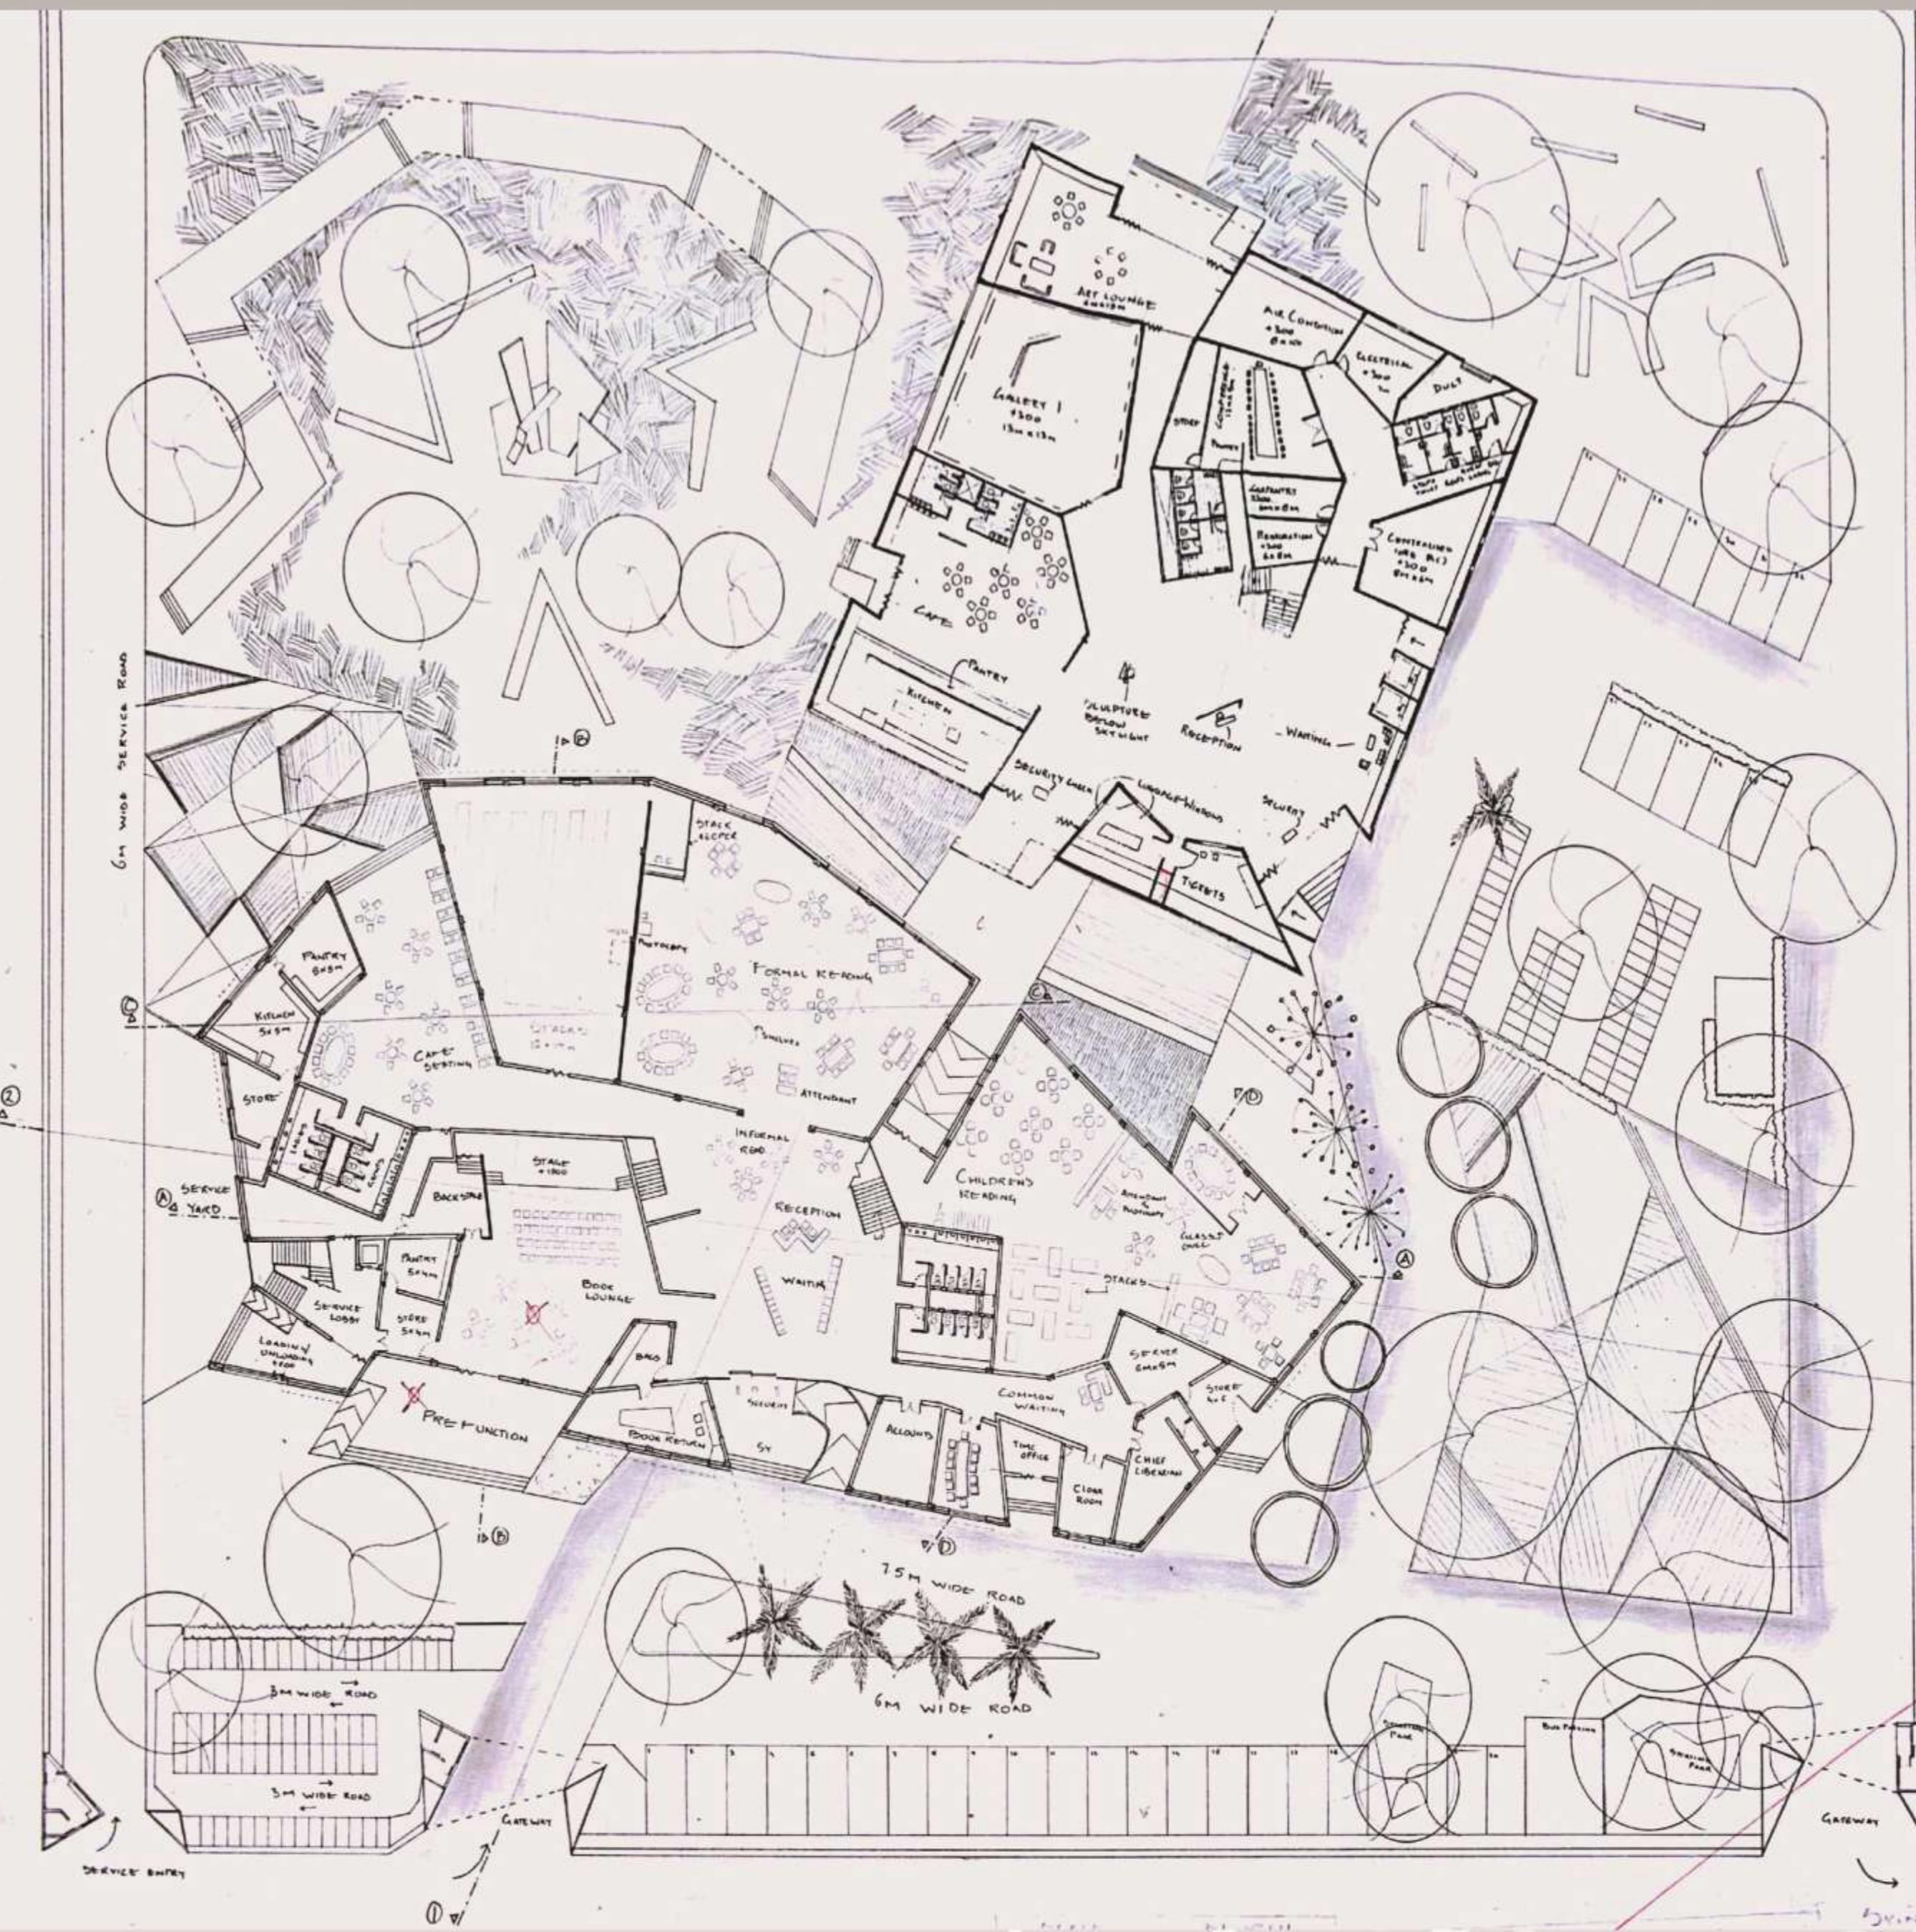


BIRDS EYE VIEW

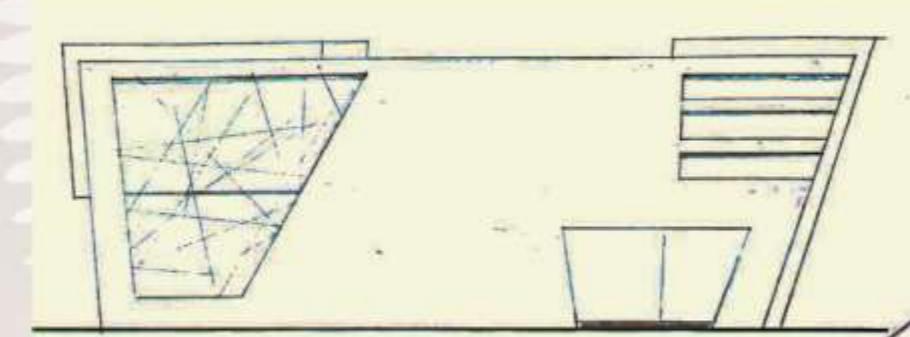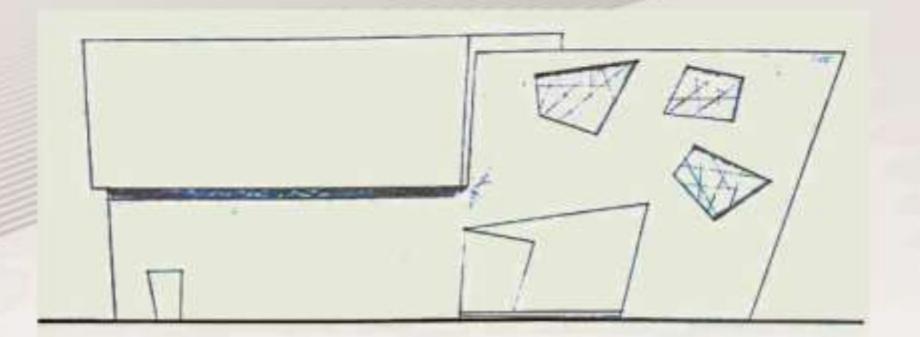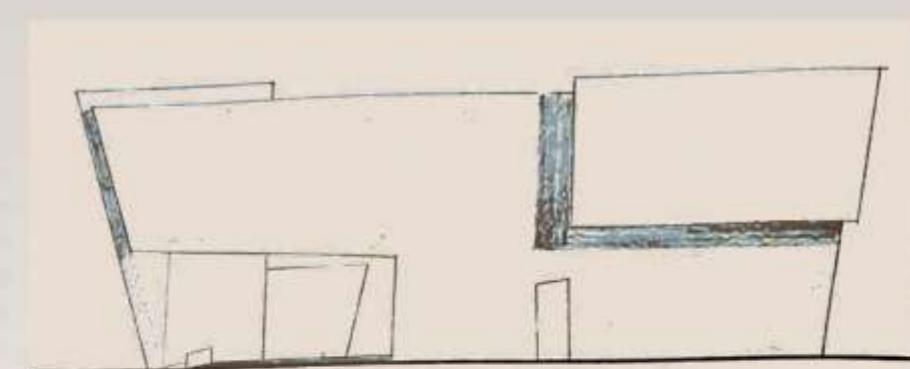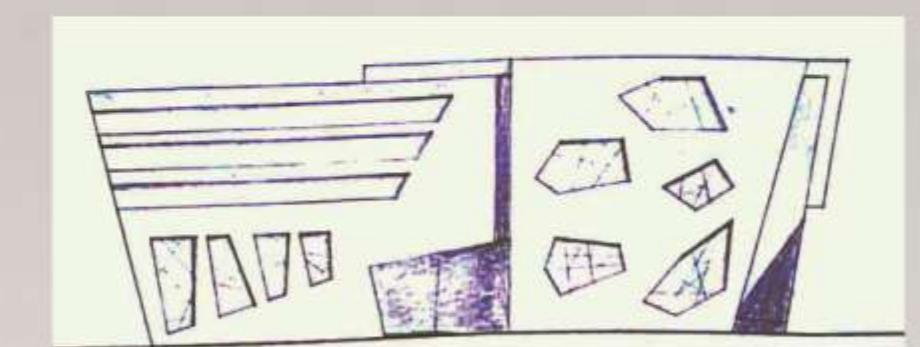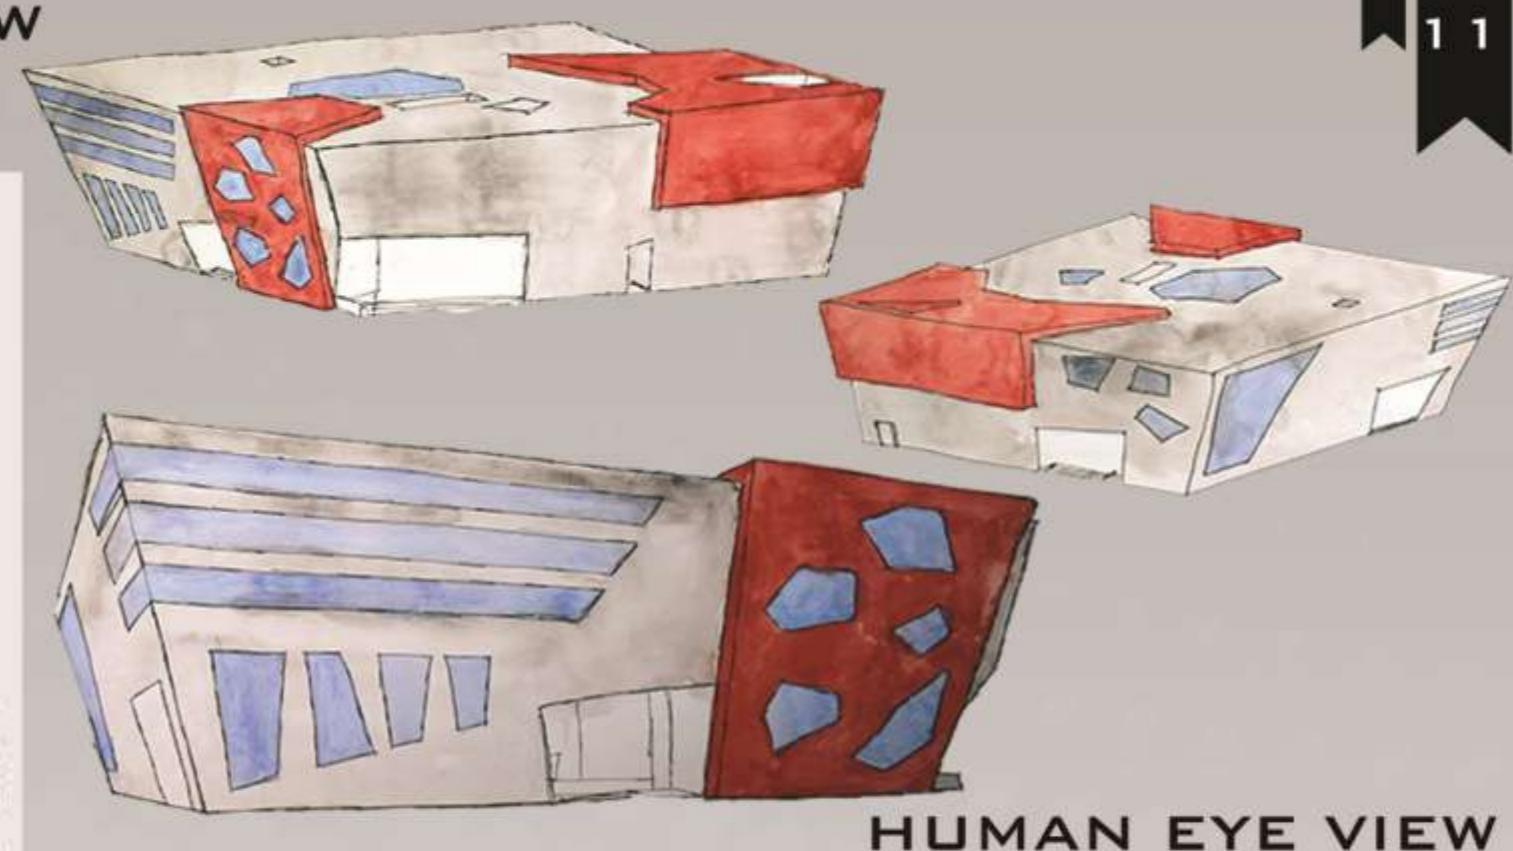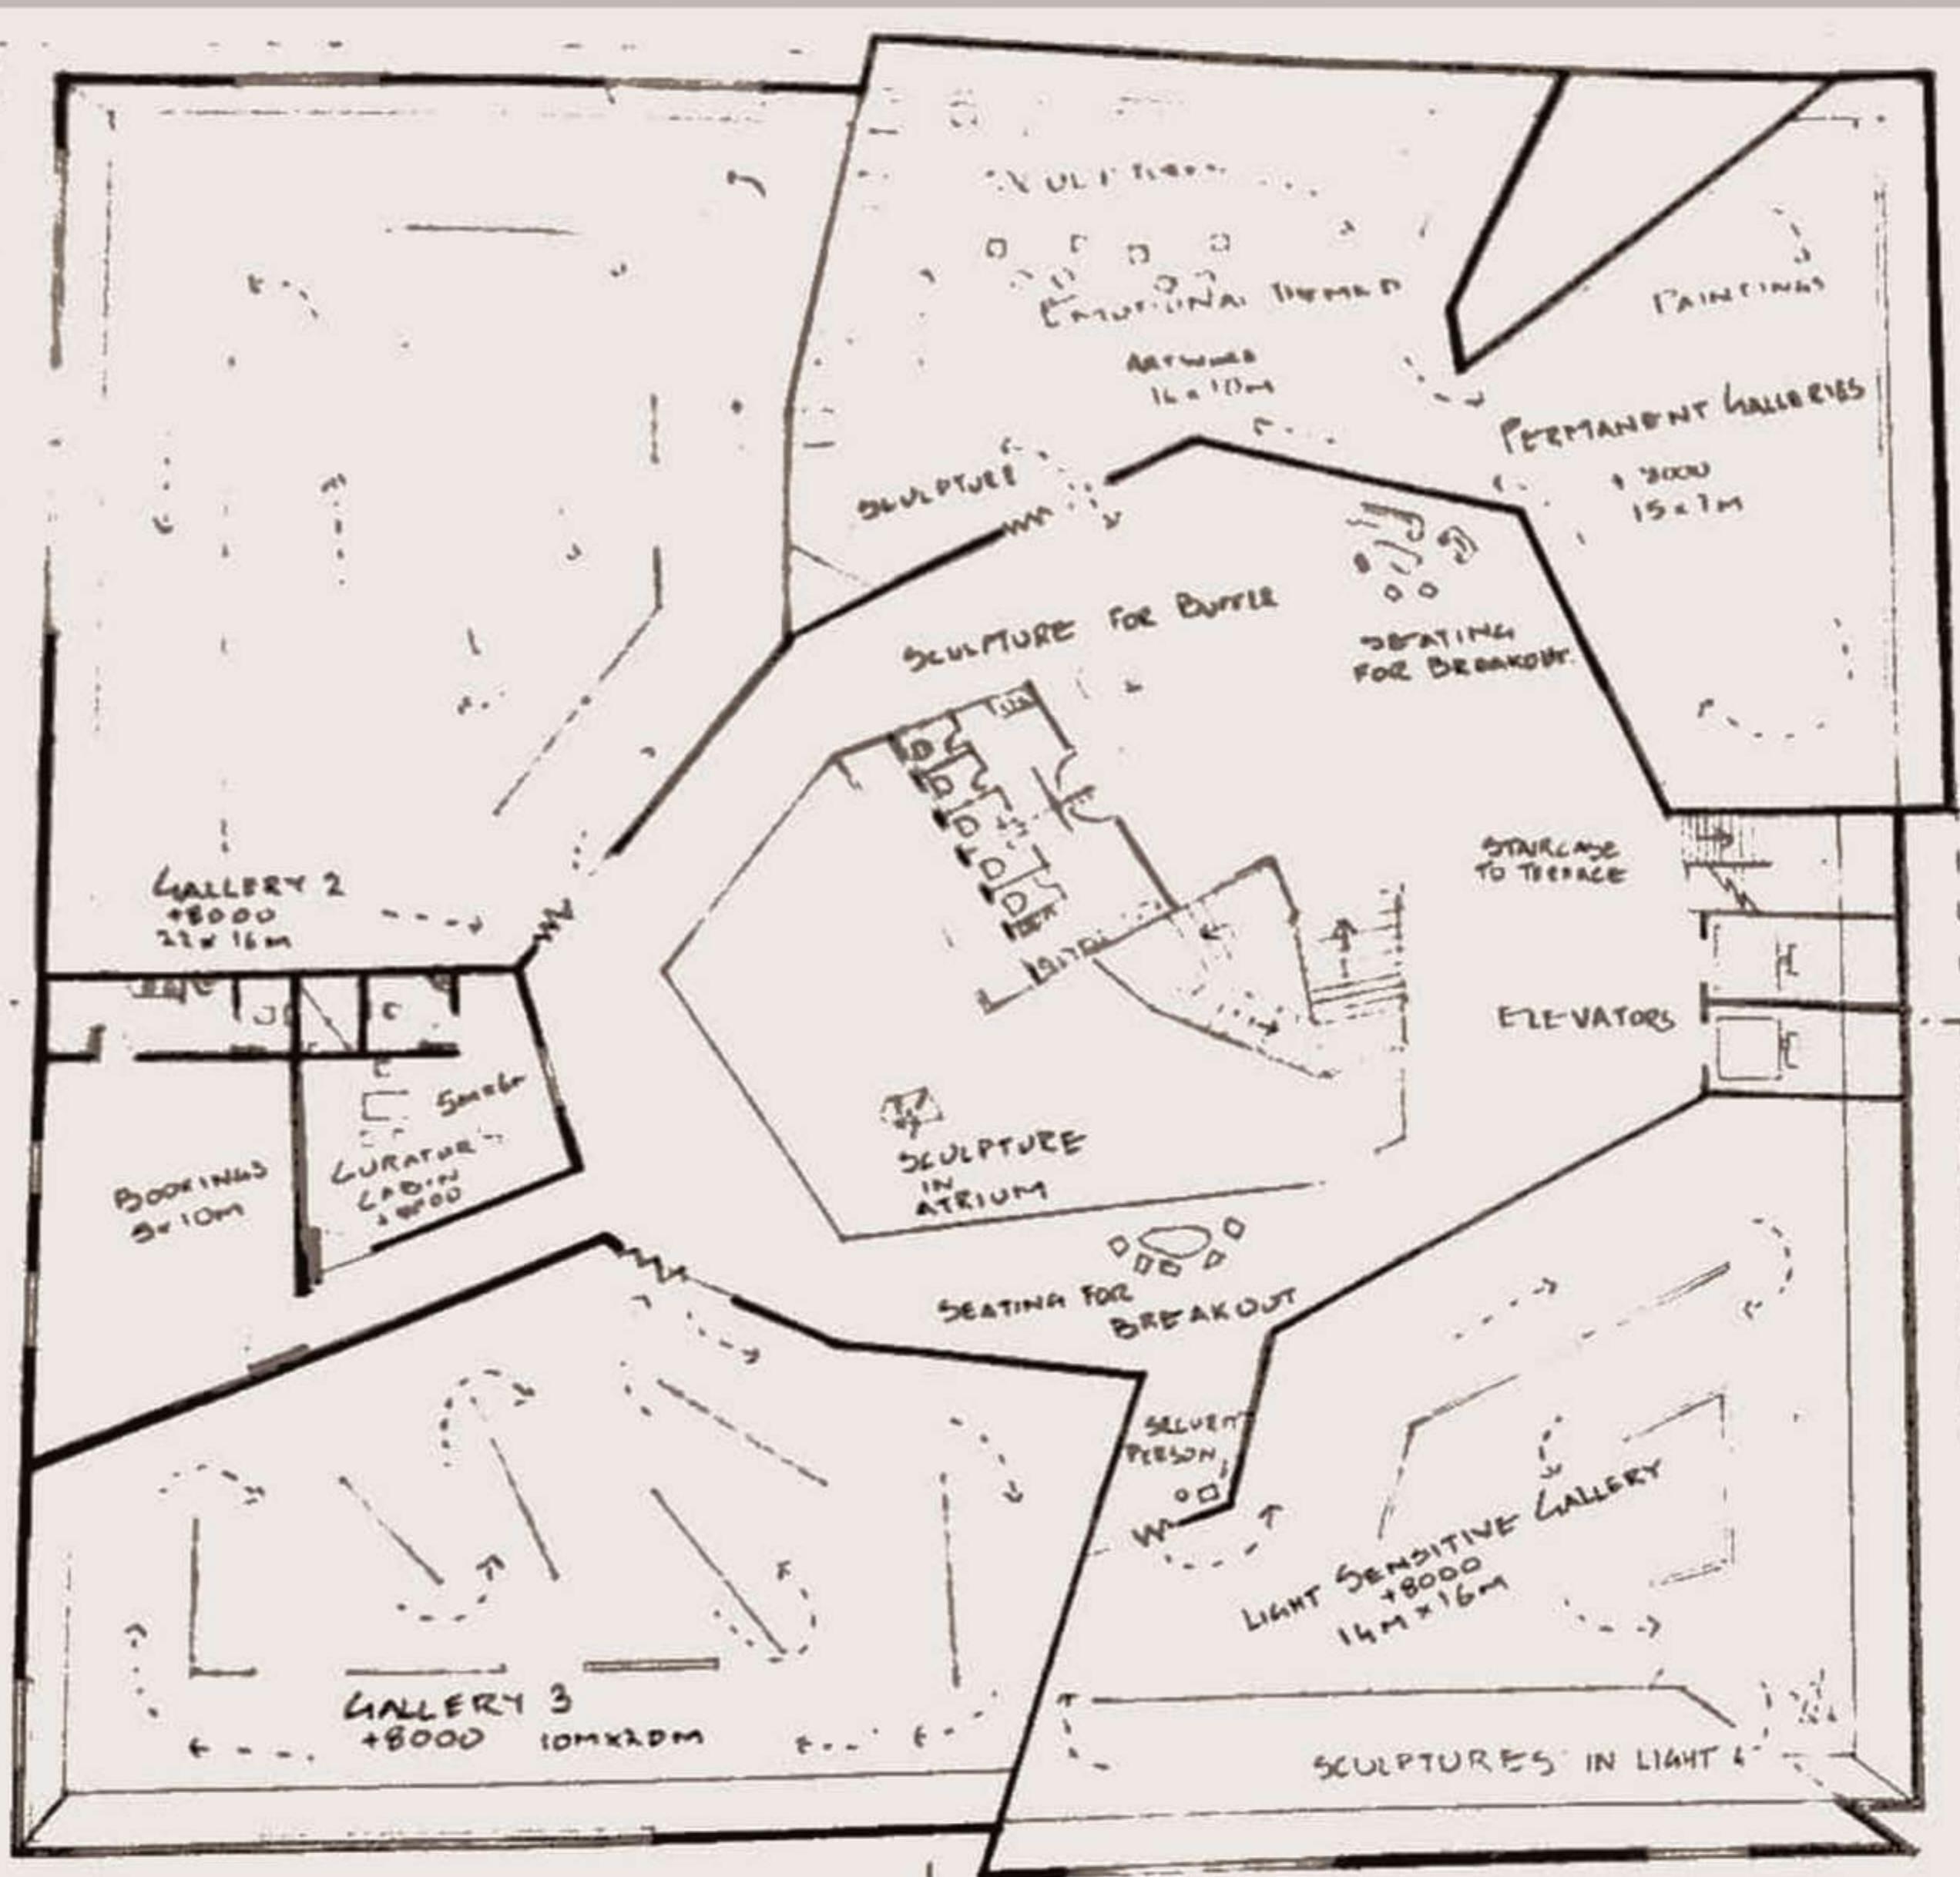





SECTION AA

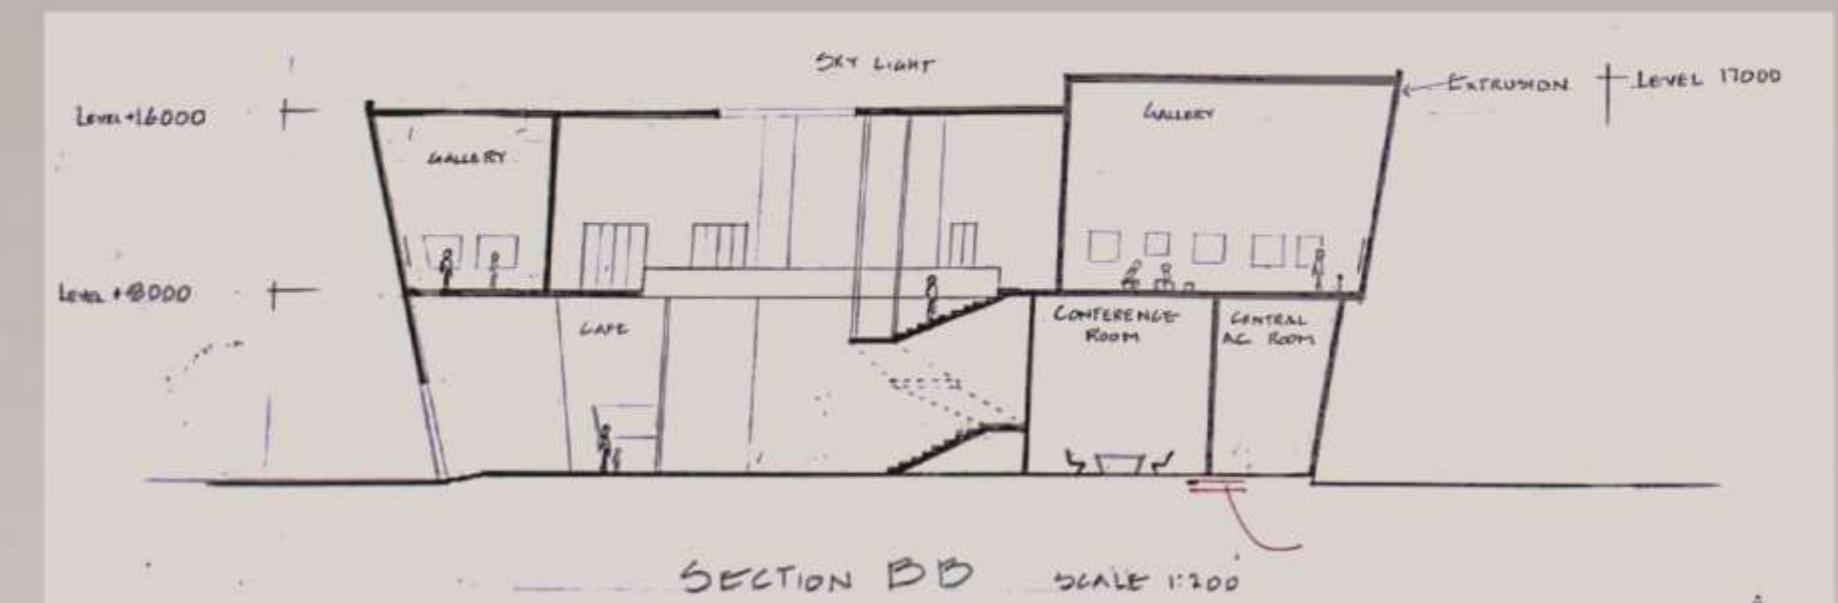


SECTION BB

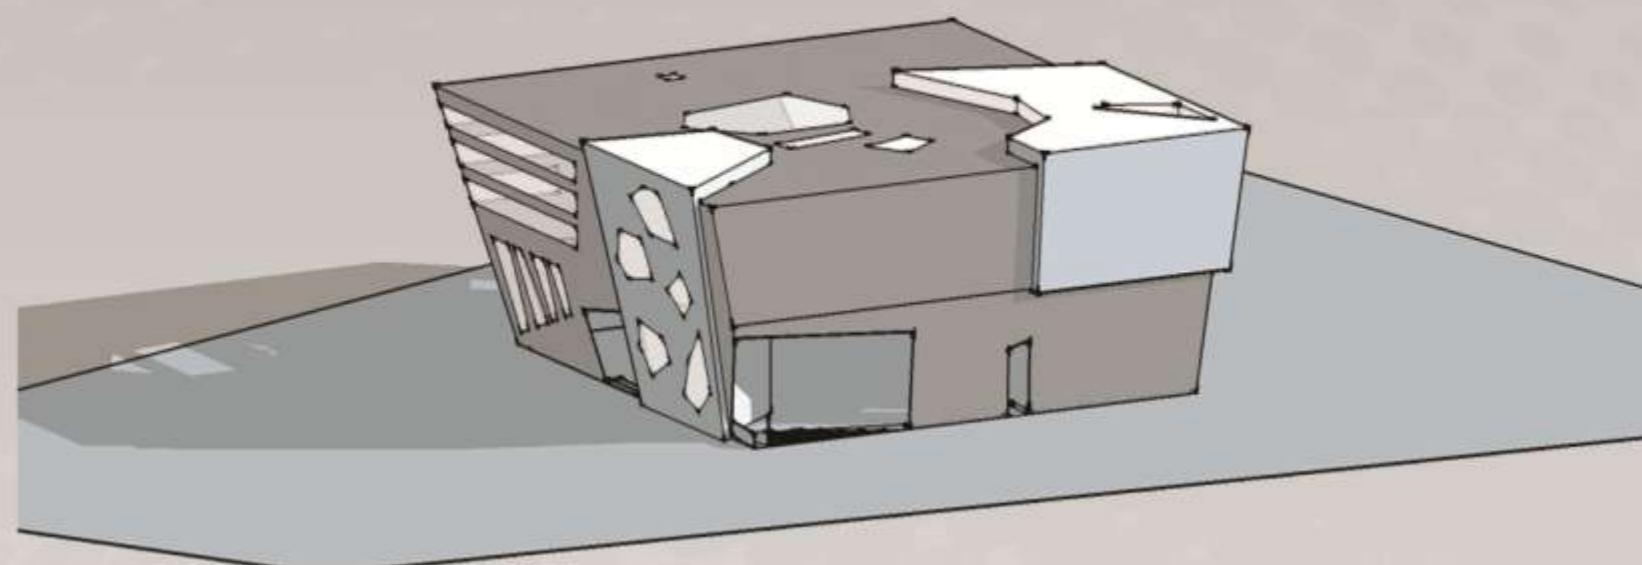


VIEW

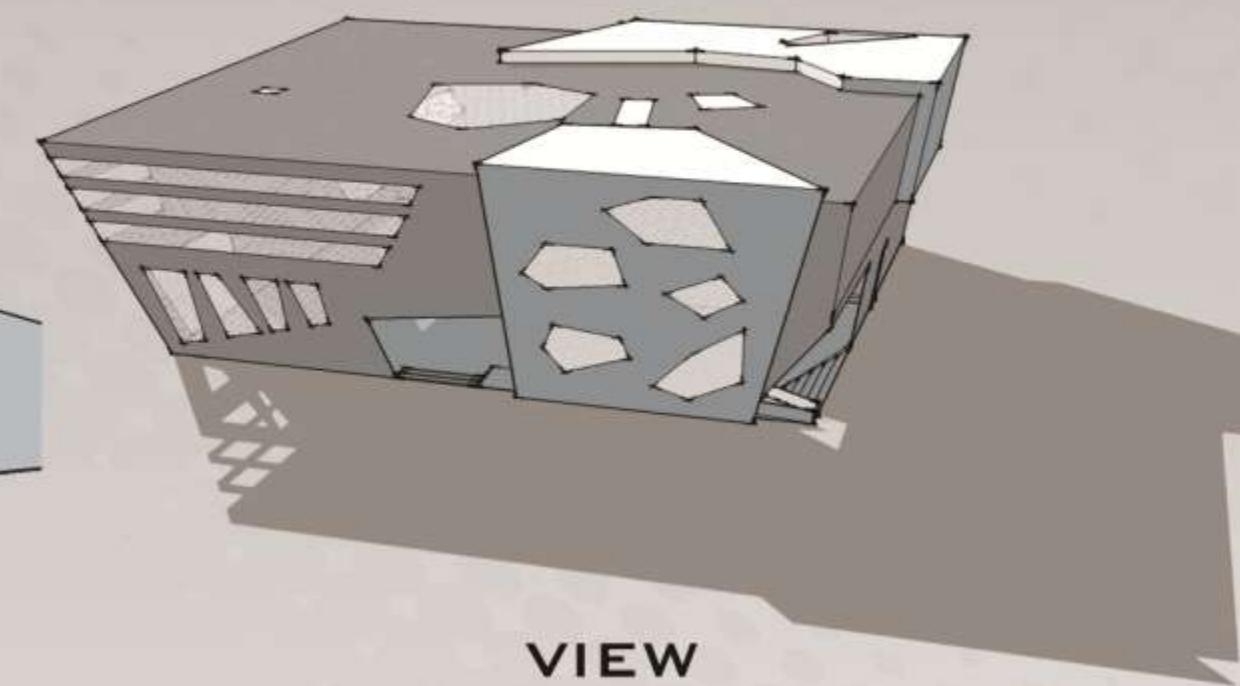


VIEW

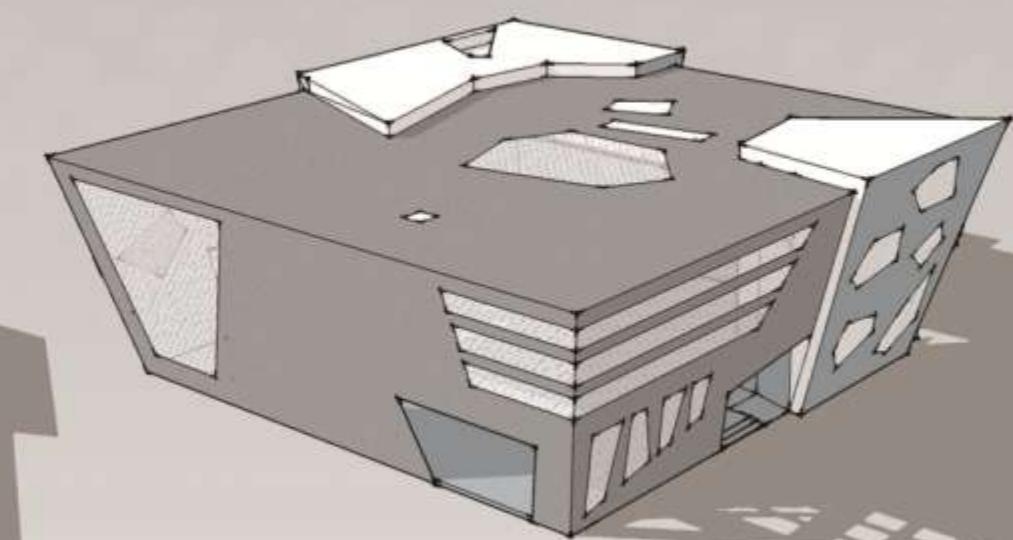


VIEW

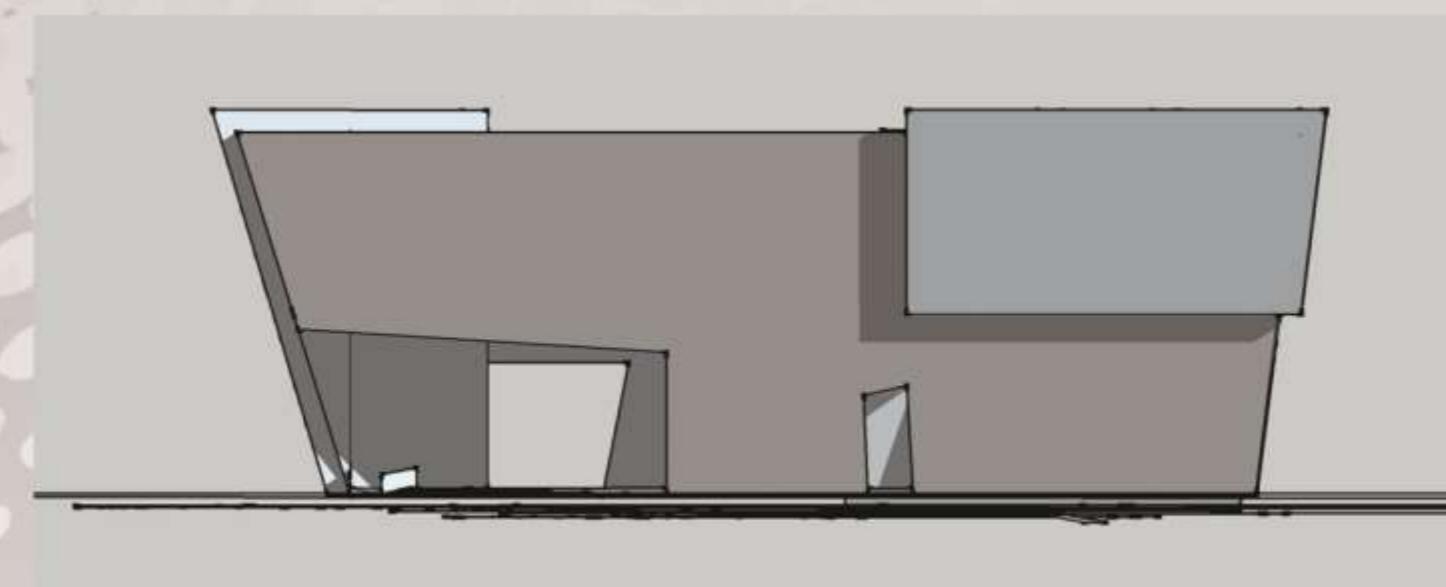


WEST SIDE ELEVATION

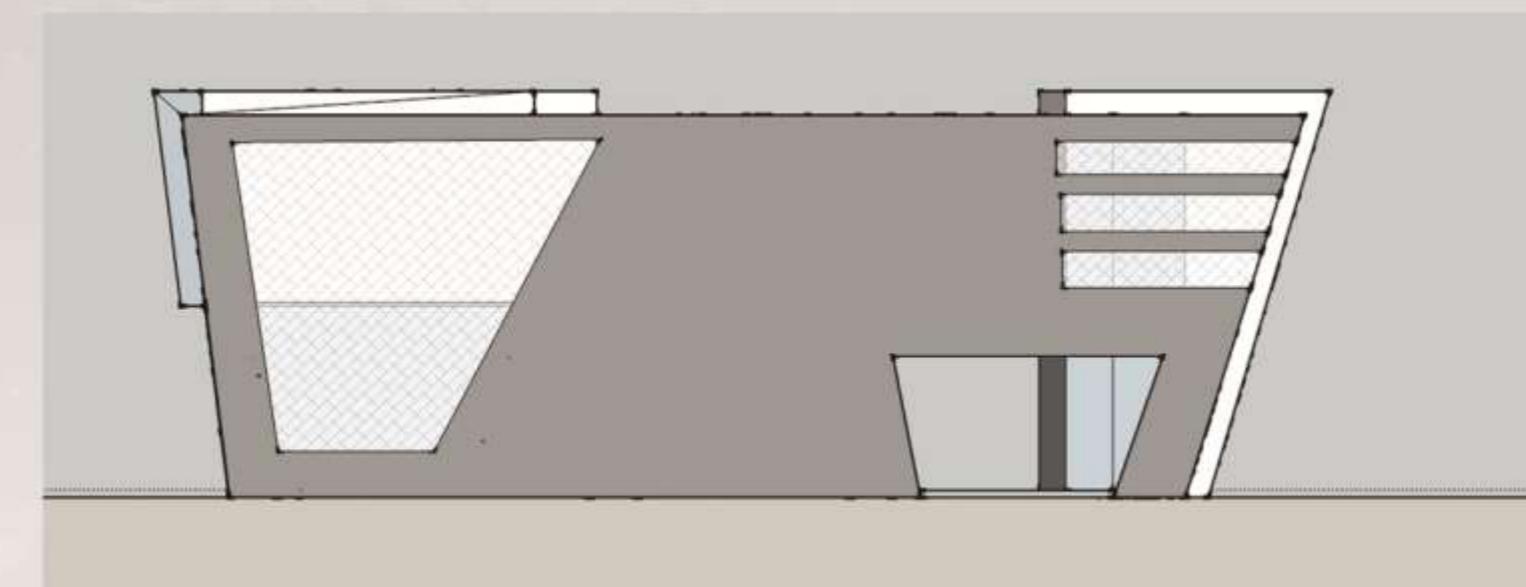

EAST SIDE ELEVATION

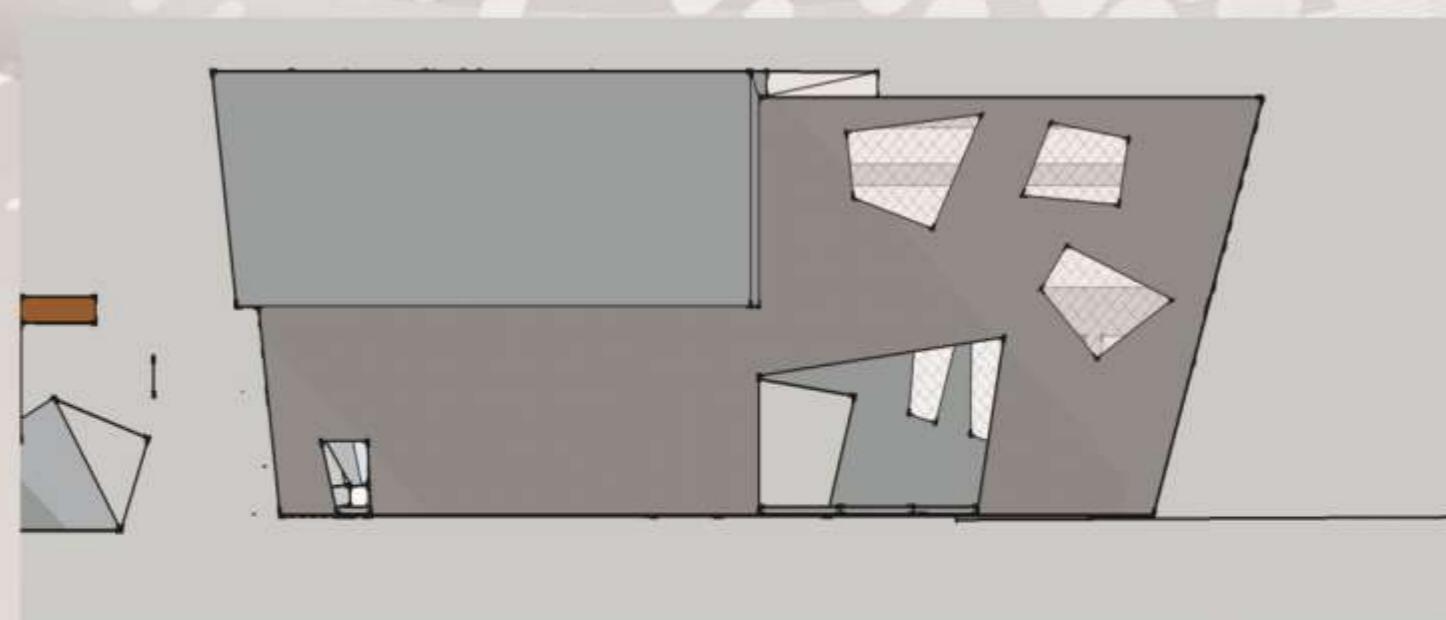

SOUTH SIDE ELEVATION


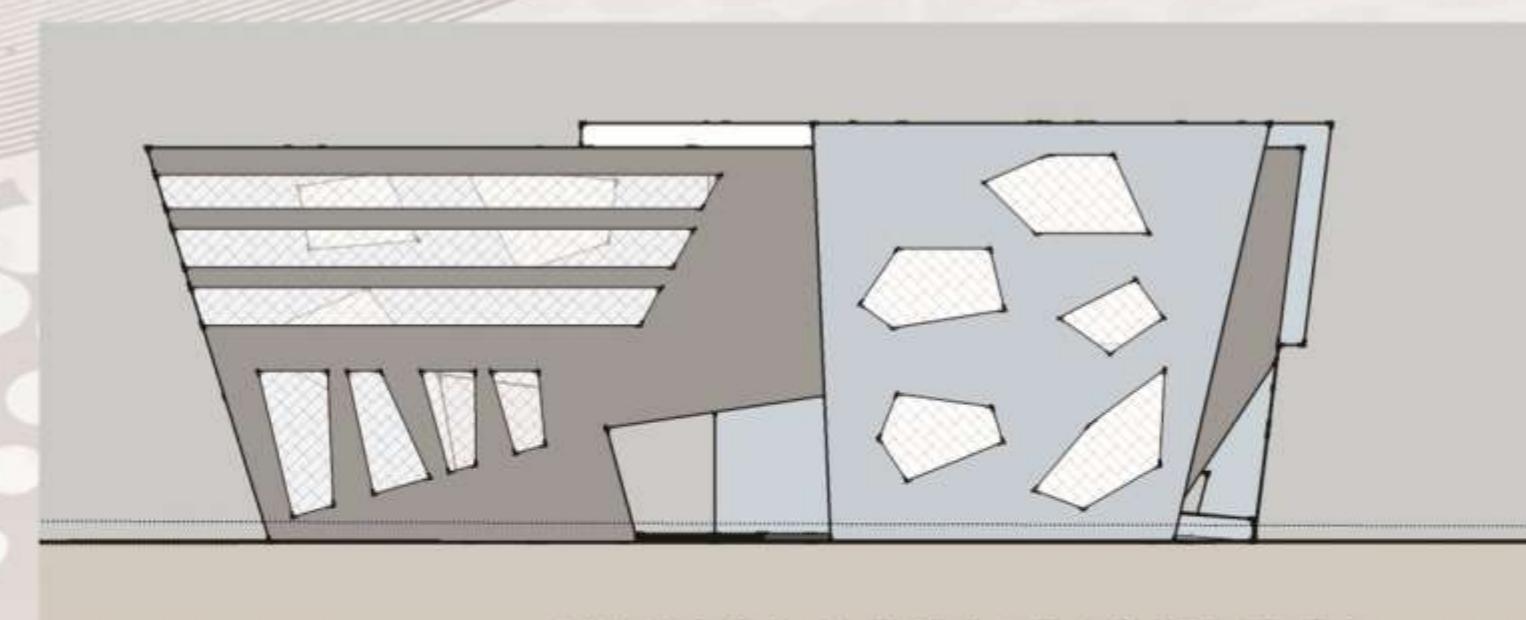


NORTH SIDE ELEVATION

CITY LIBRARY.

BUILUP AREA- 5560 SQ.M


DESIGN APPROACH- THE AIM WAS TO BUILD A CITY LIBRARY WHICH ATTRACTS THE YOUTH & TO INculcate THE HABIT OF READING IN THE YOUNG GENERATION. THE ORIGAMI ROOF AD THE DYNAMIC WINDOWS HELP DESIGNING A CONTEMPORARY BUILDING WHICH WILL SERVE THE AIM.



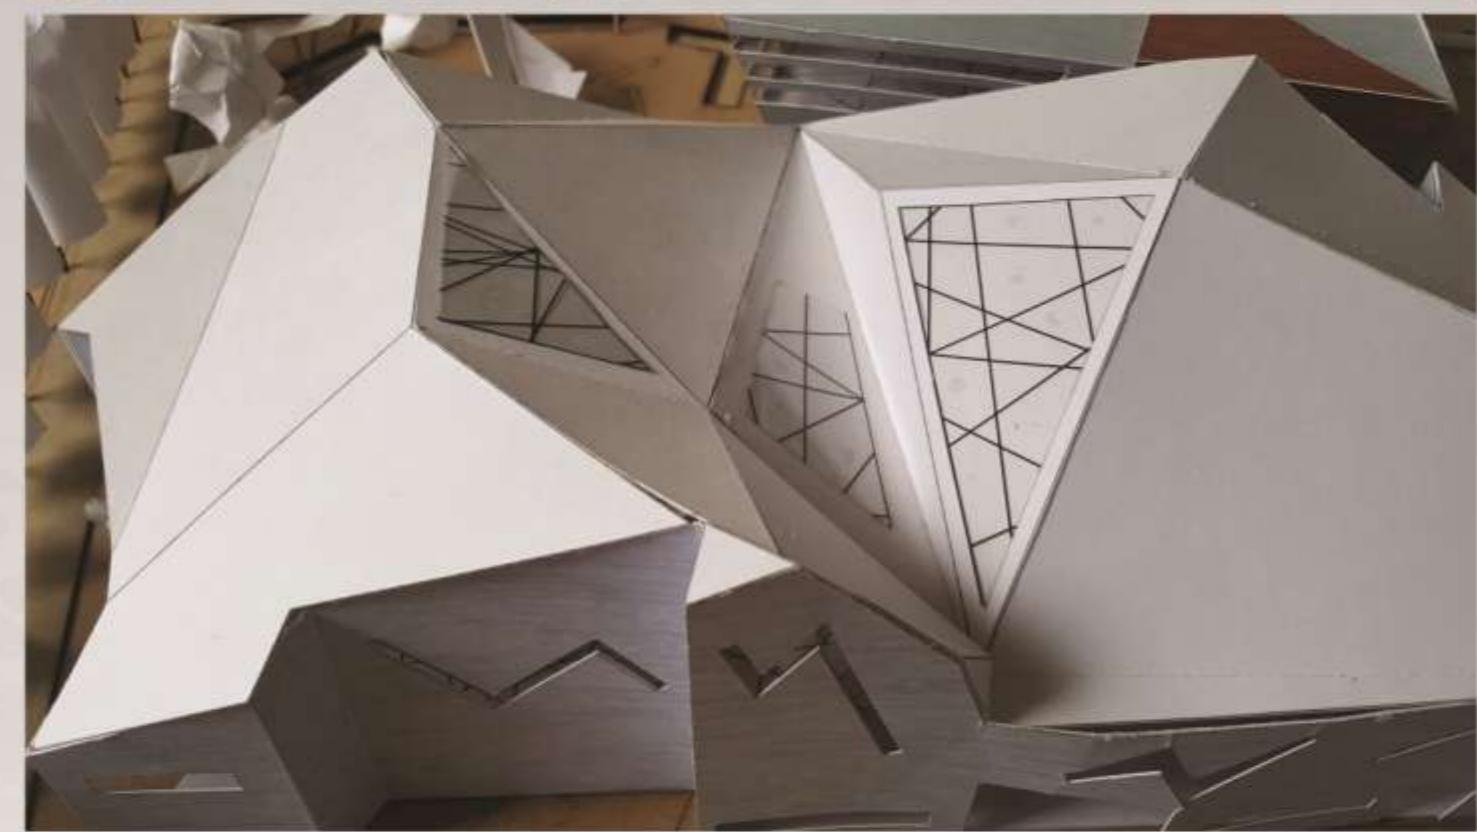
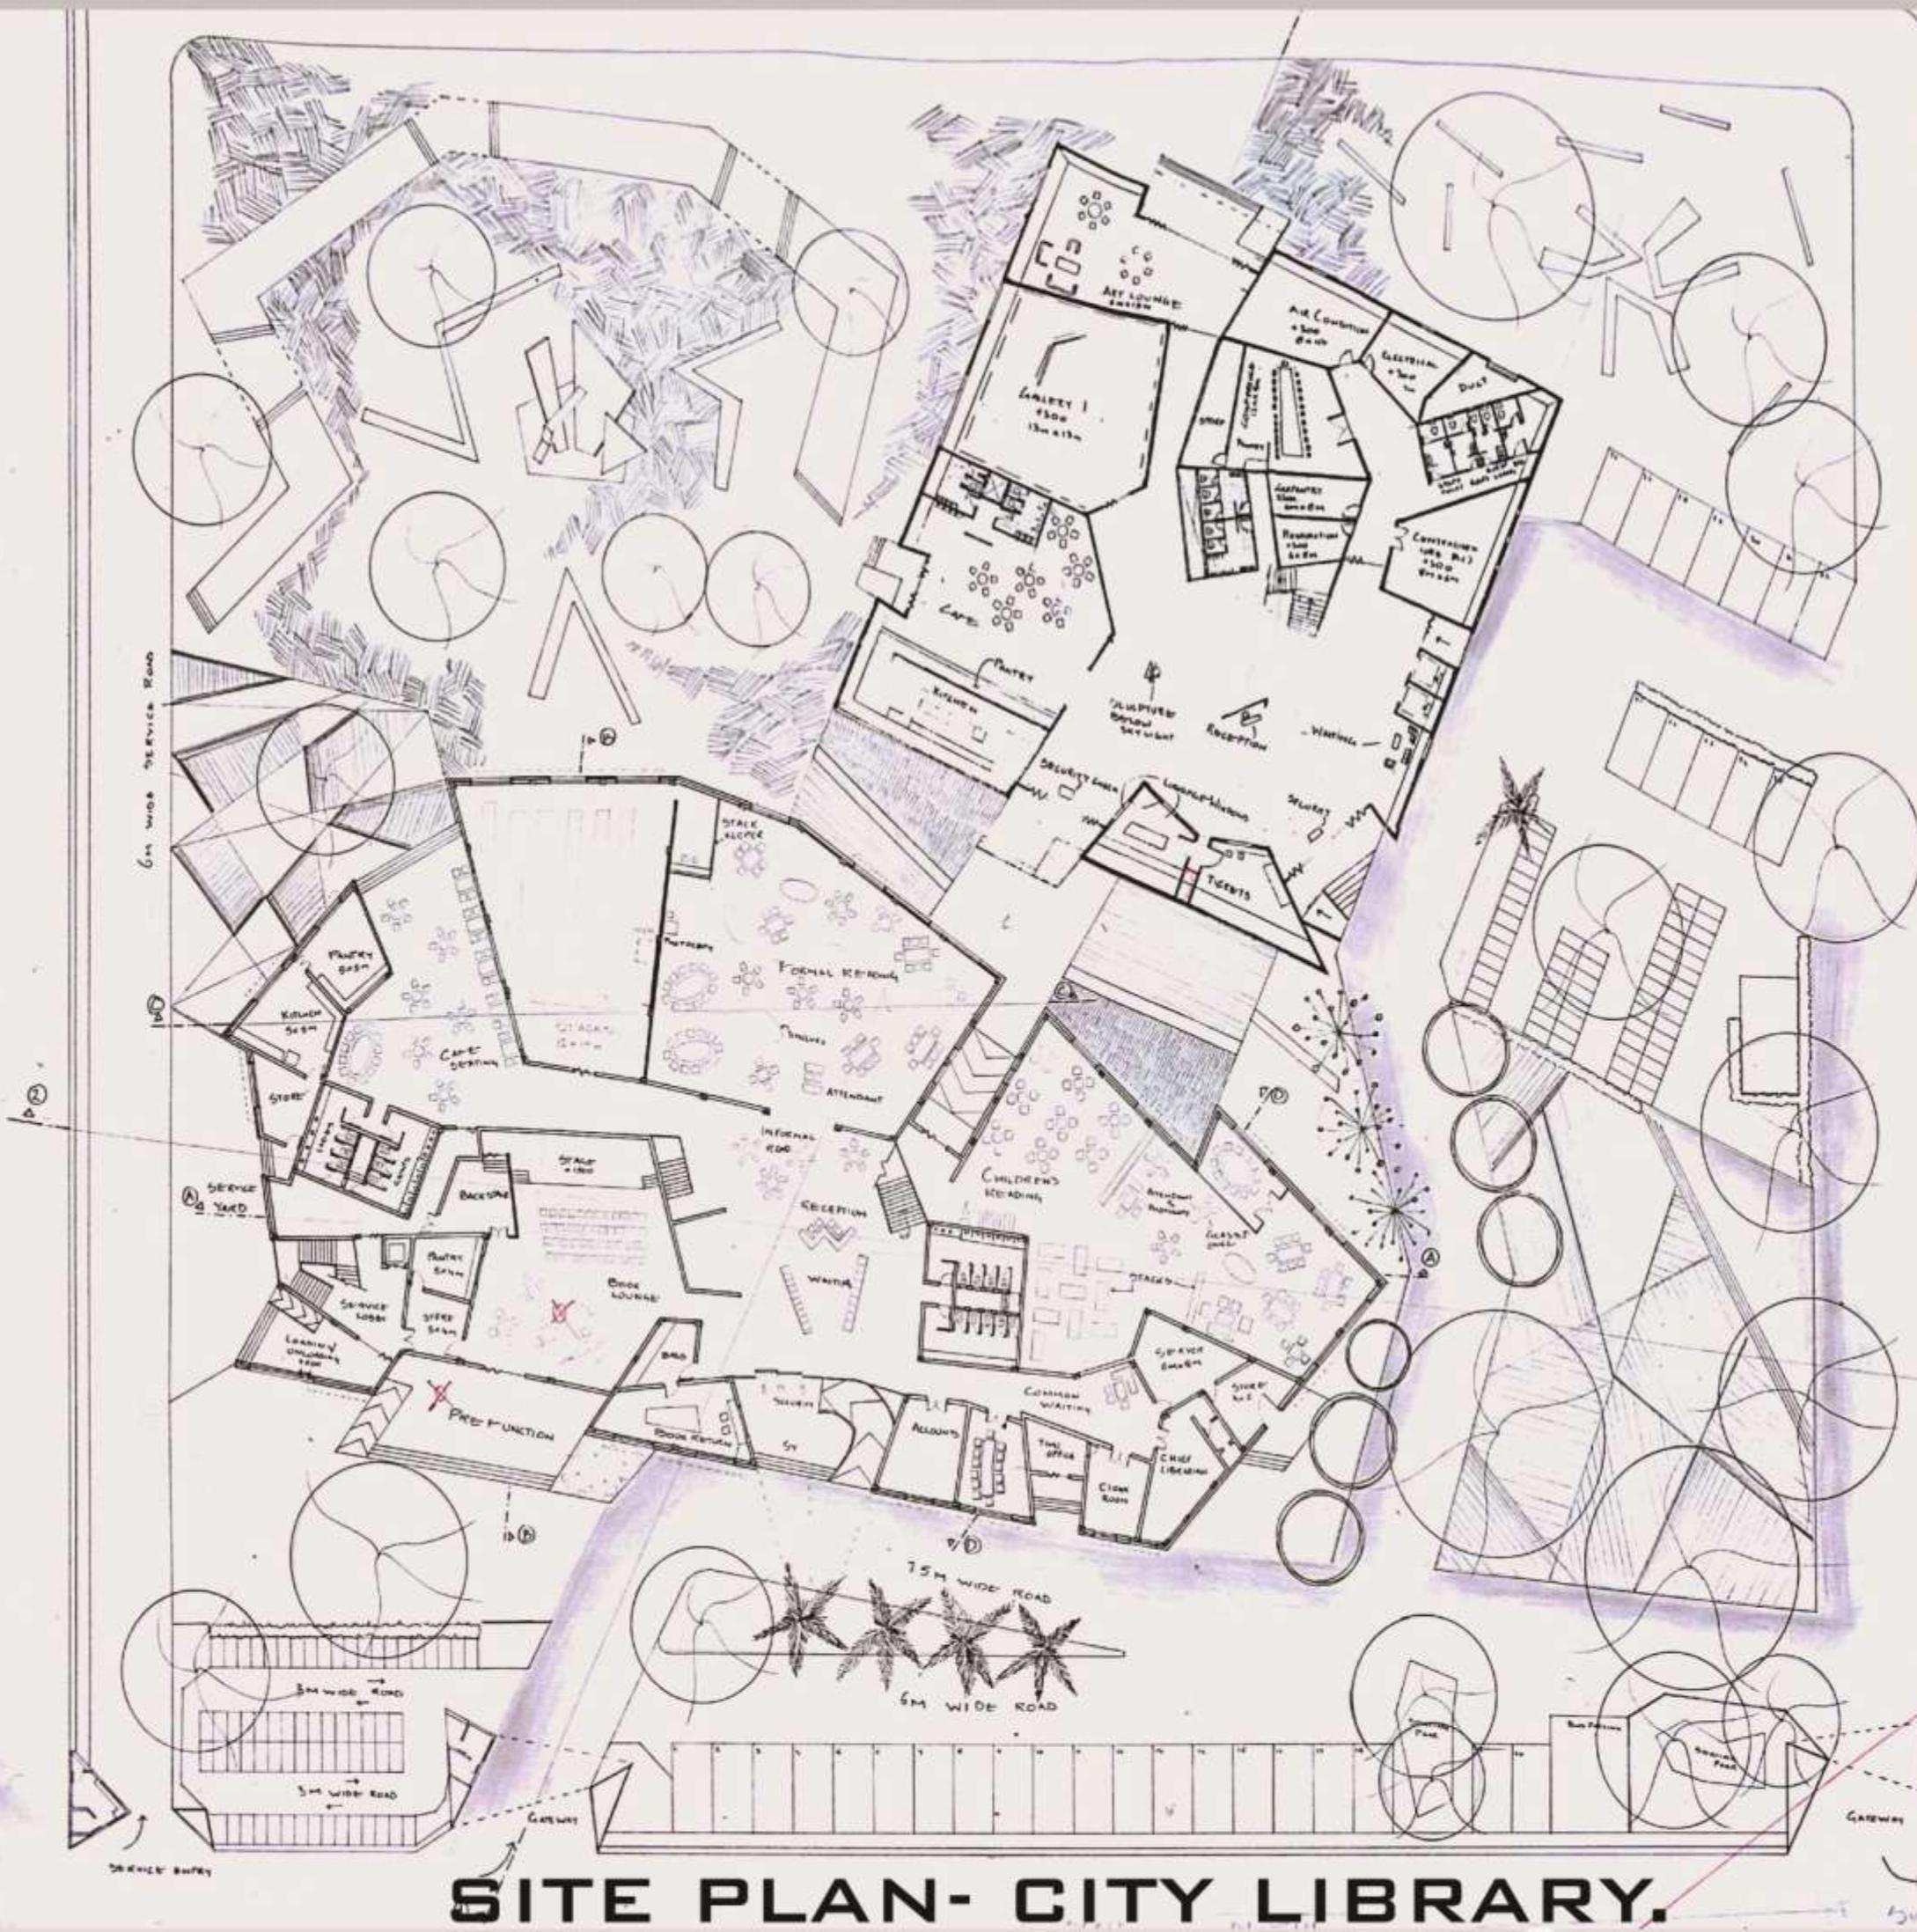


NORTH



MODEL PICTURES.

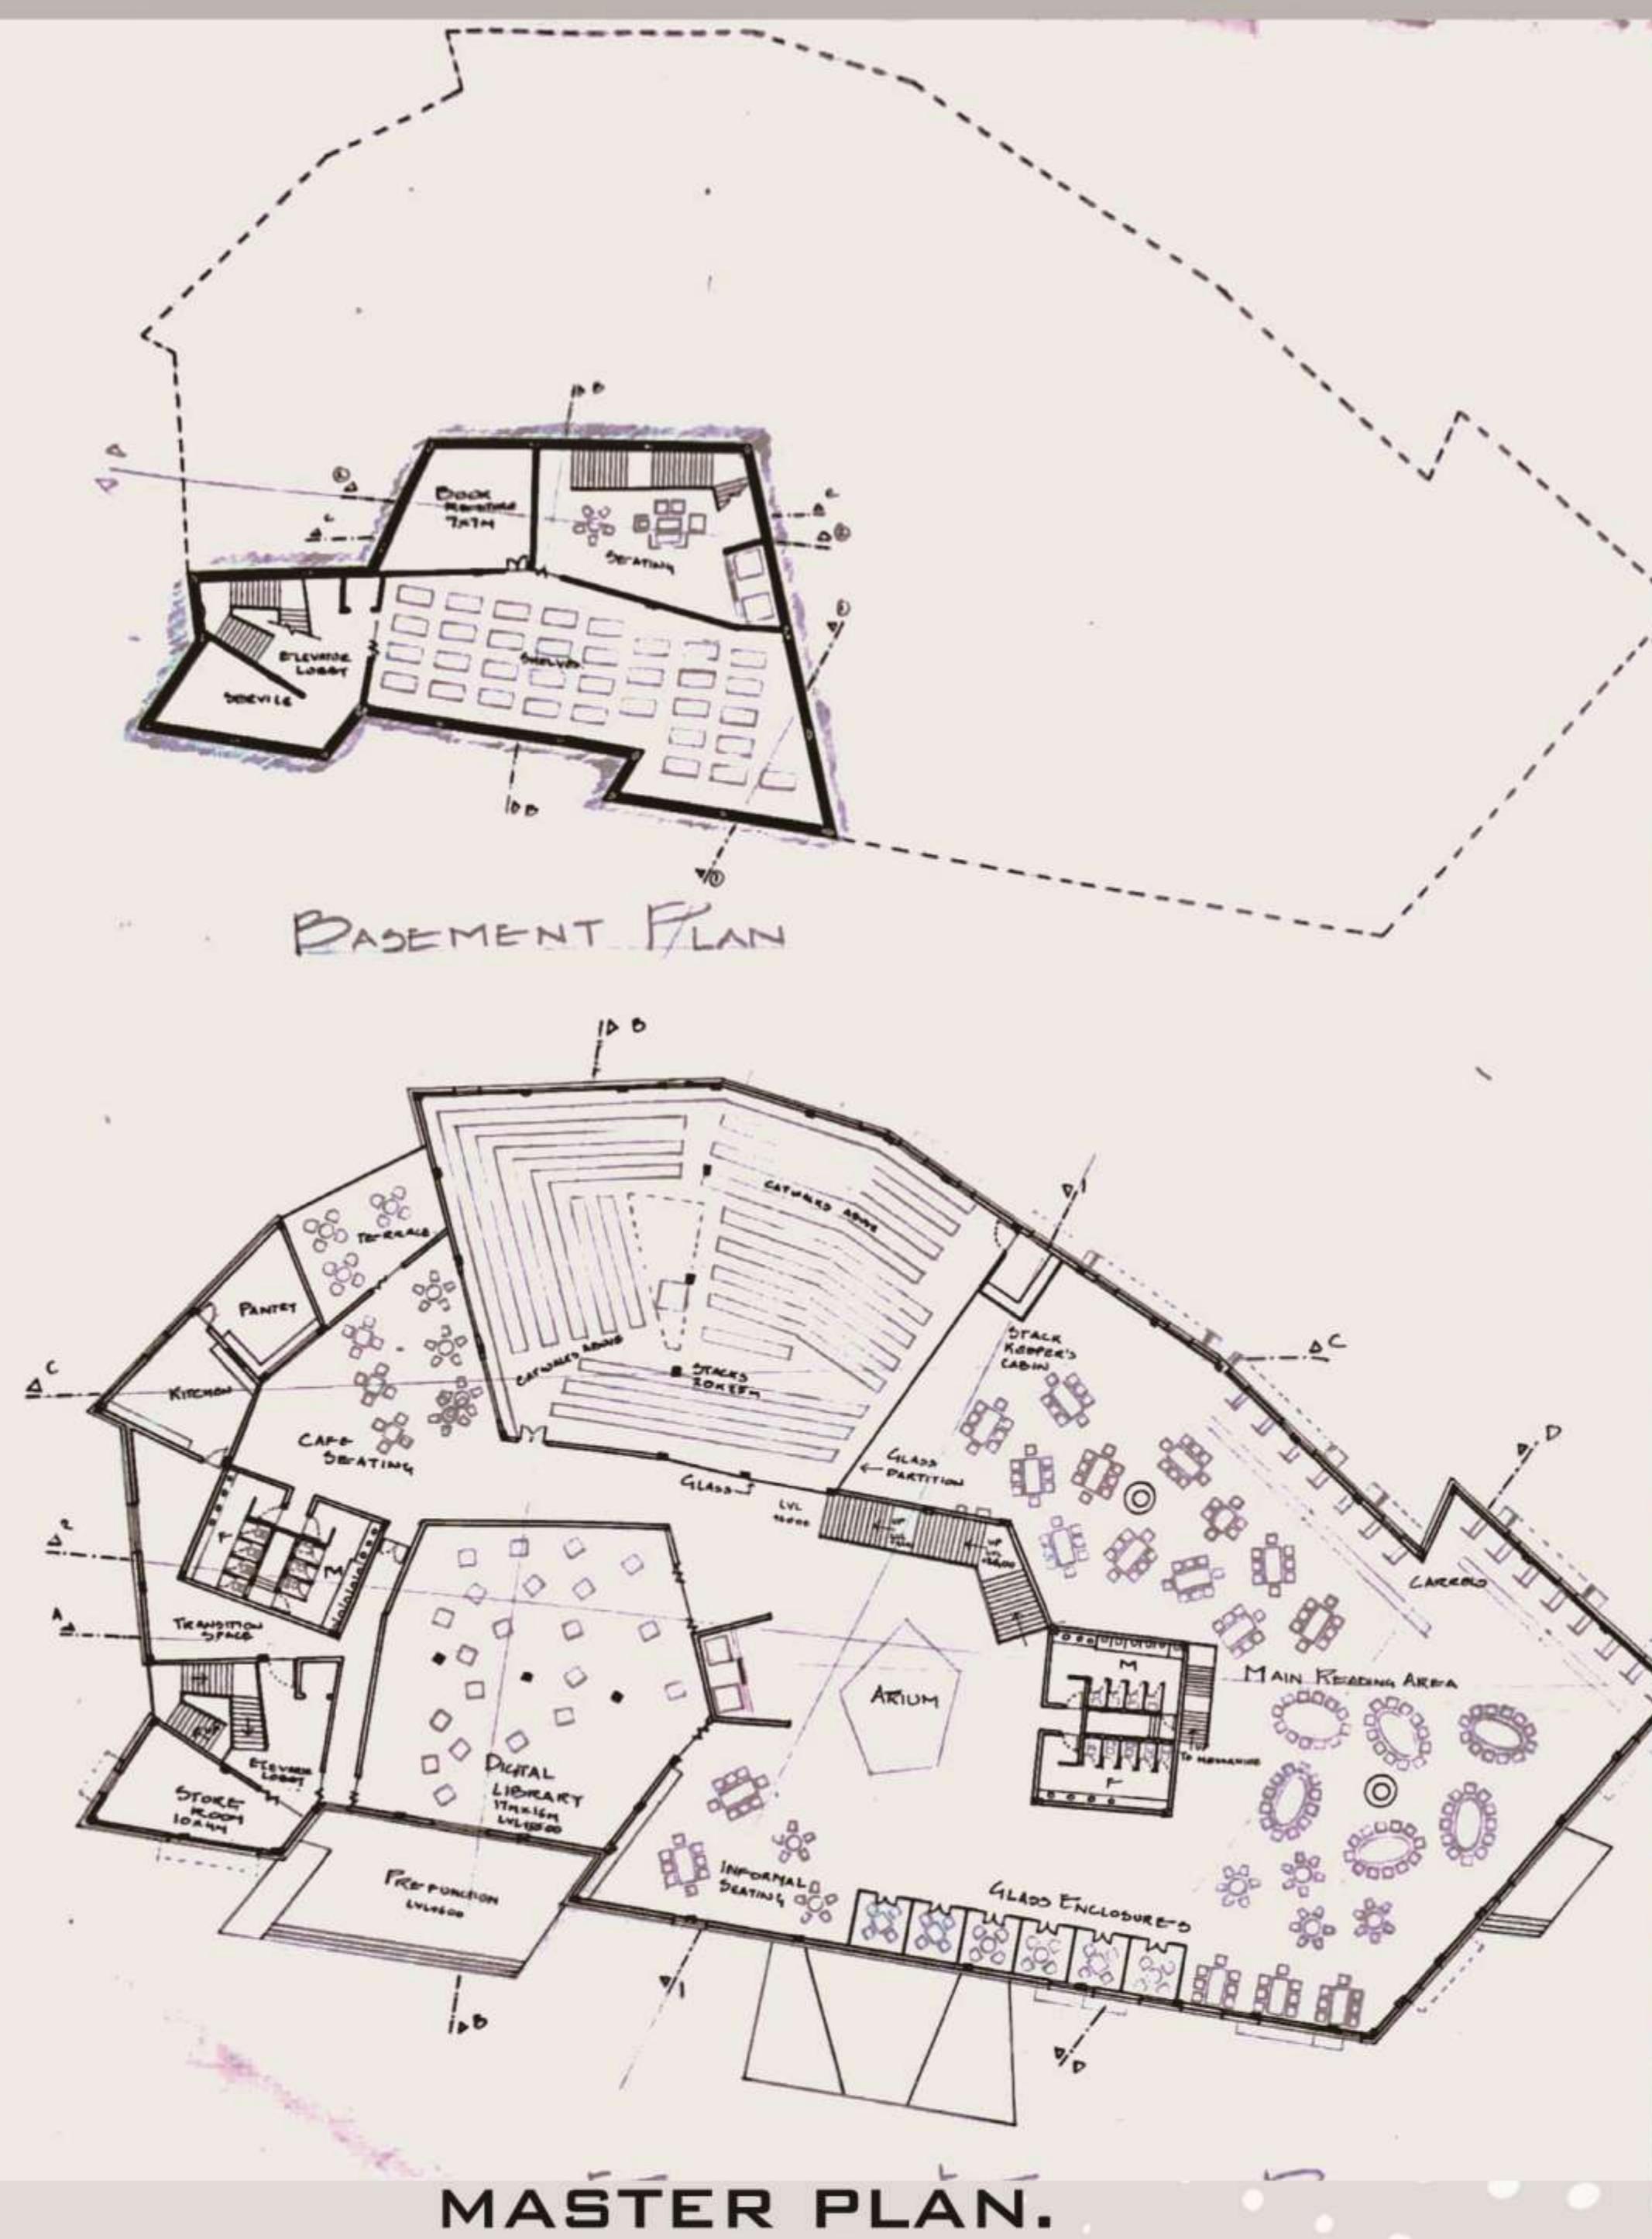

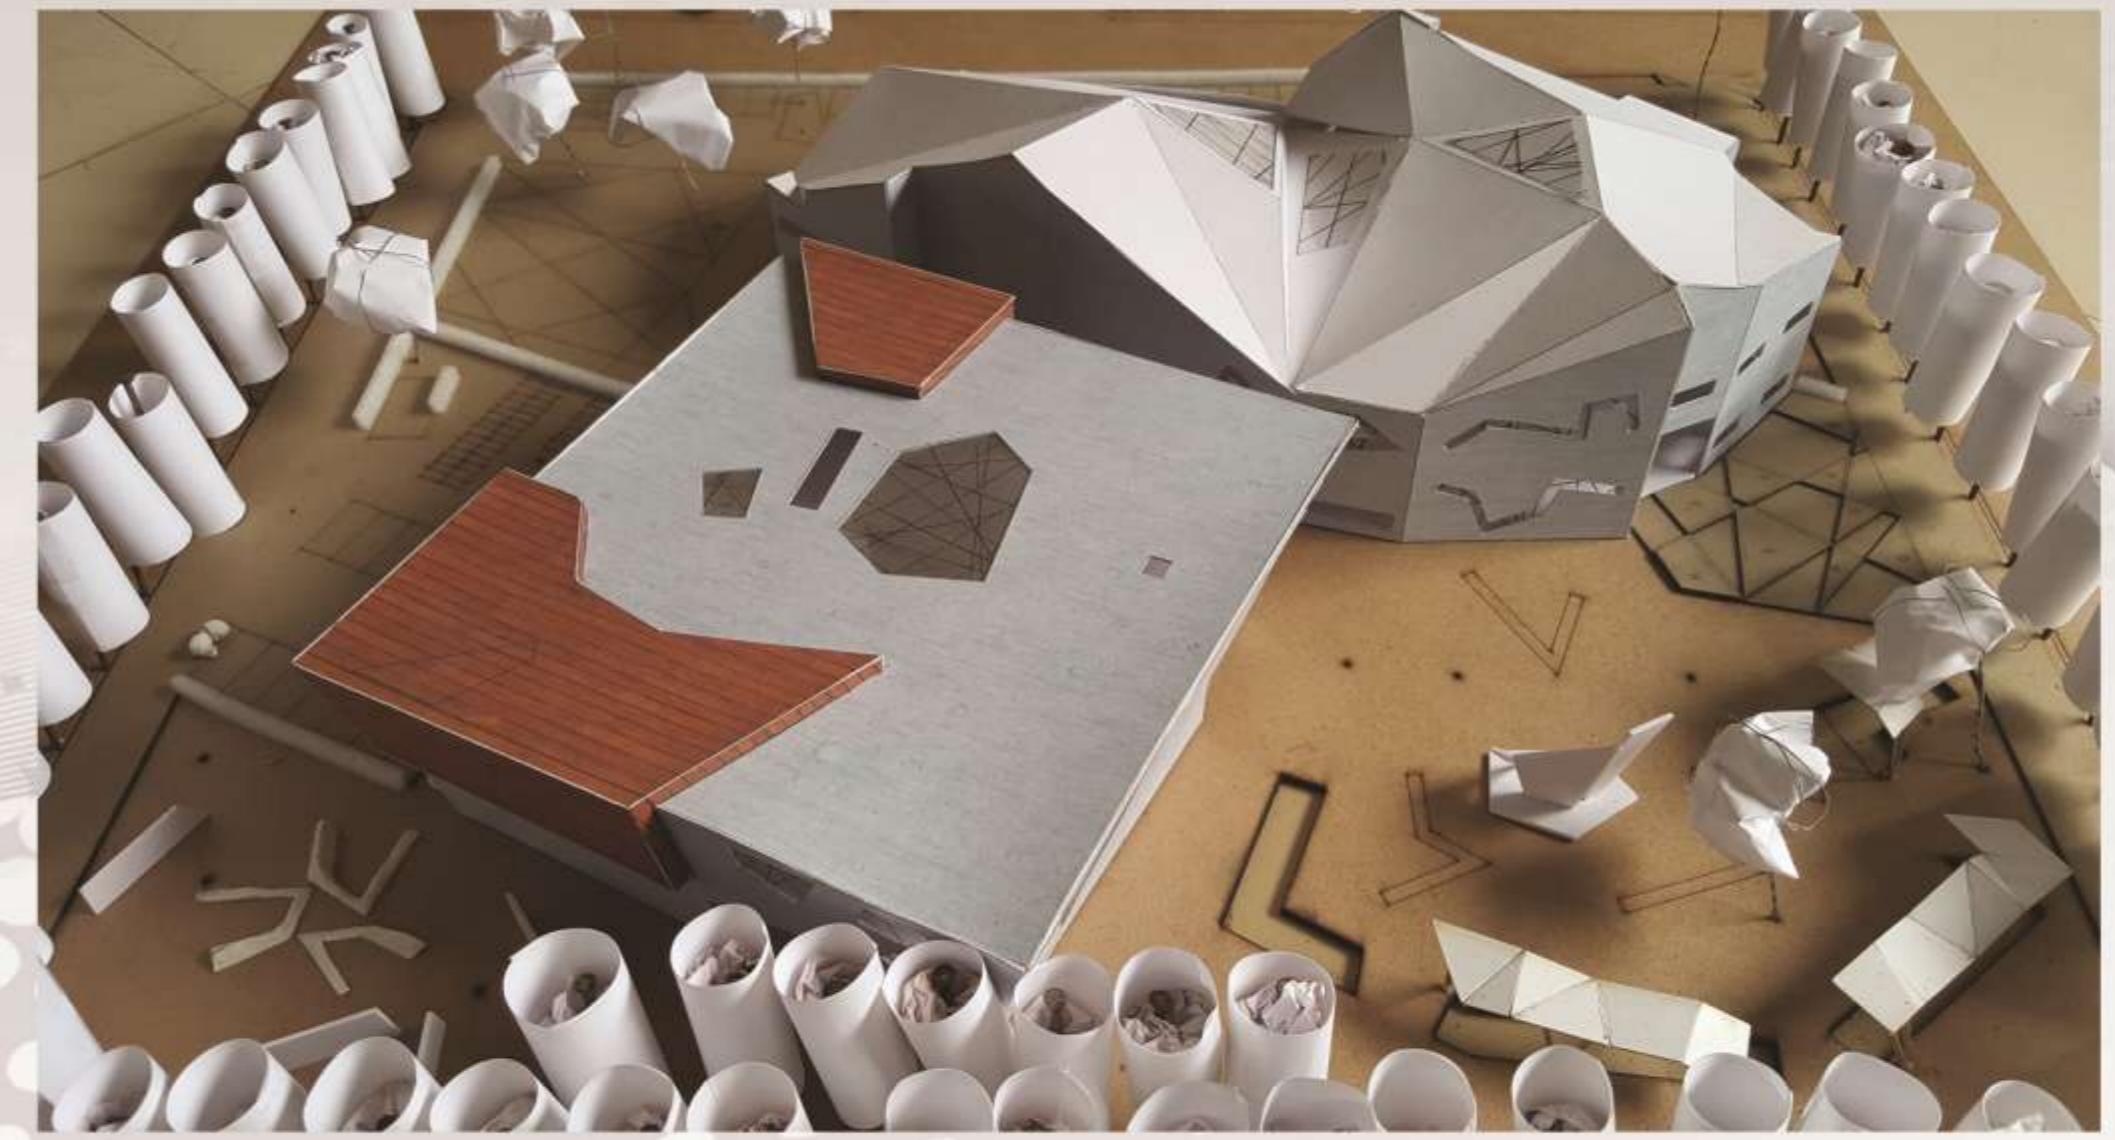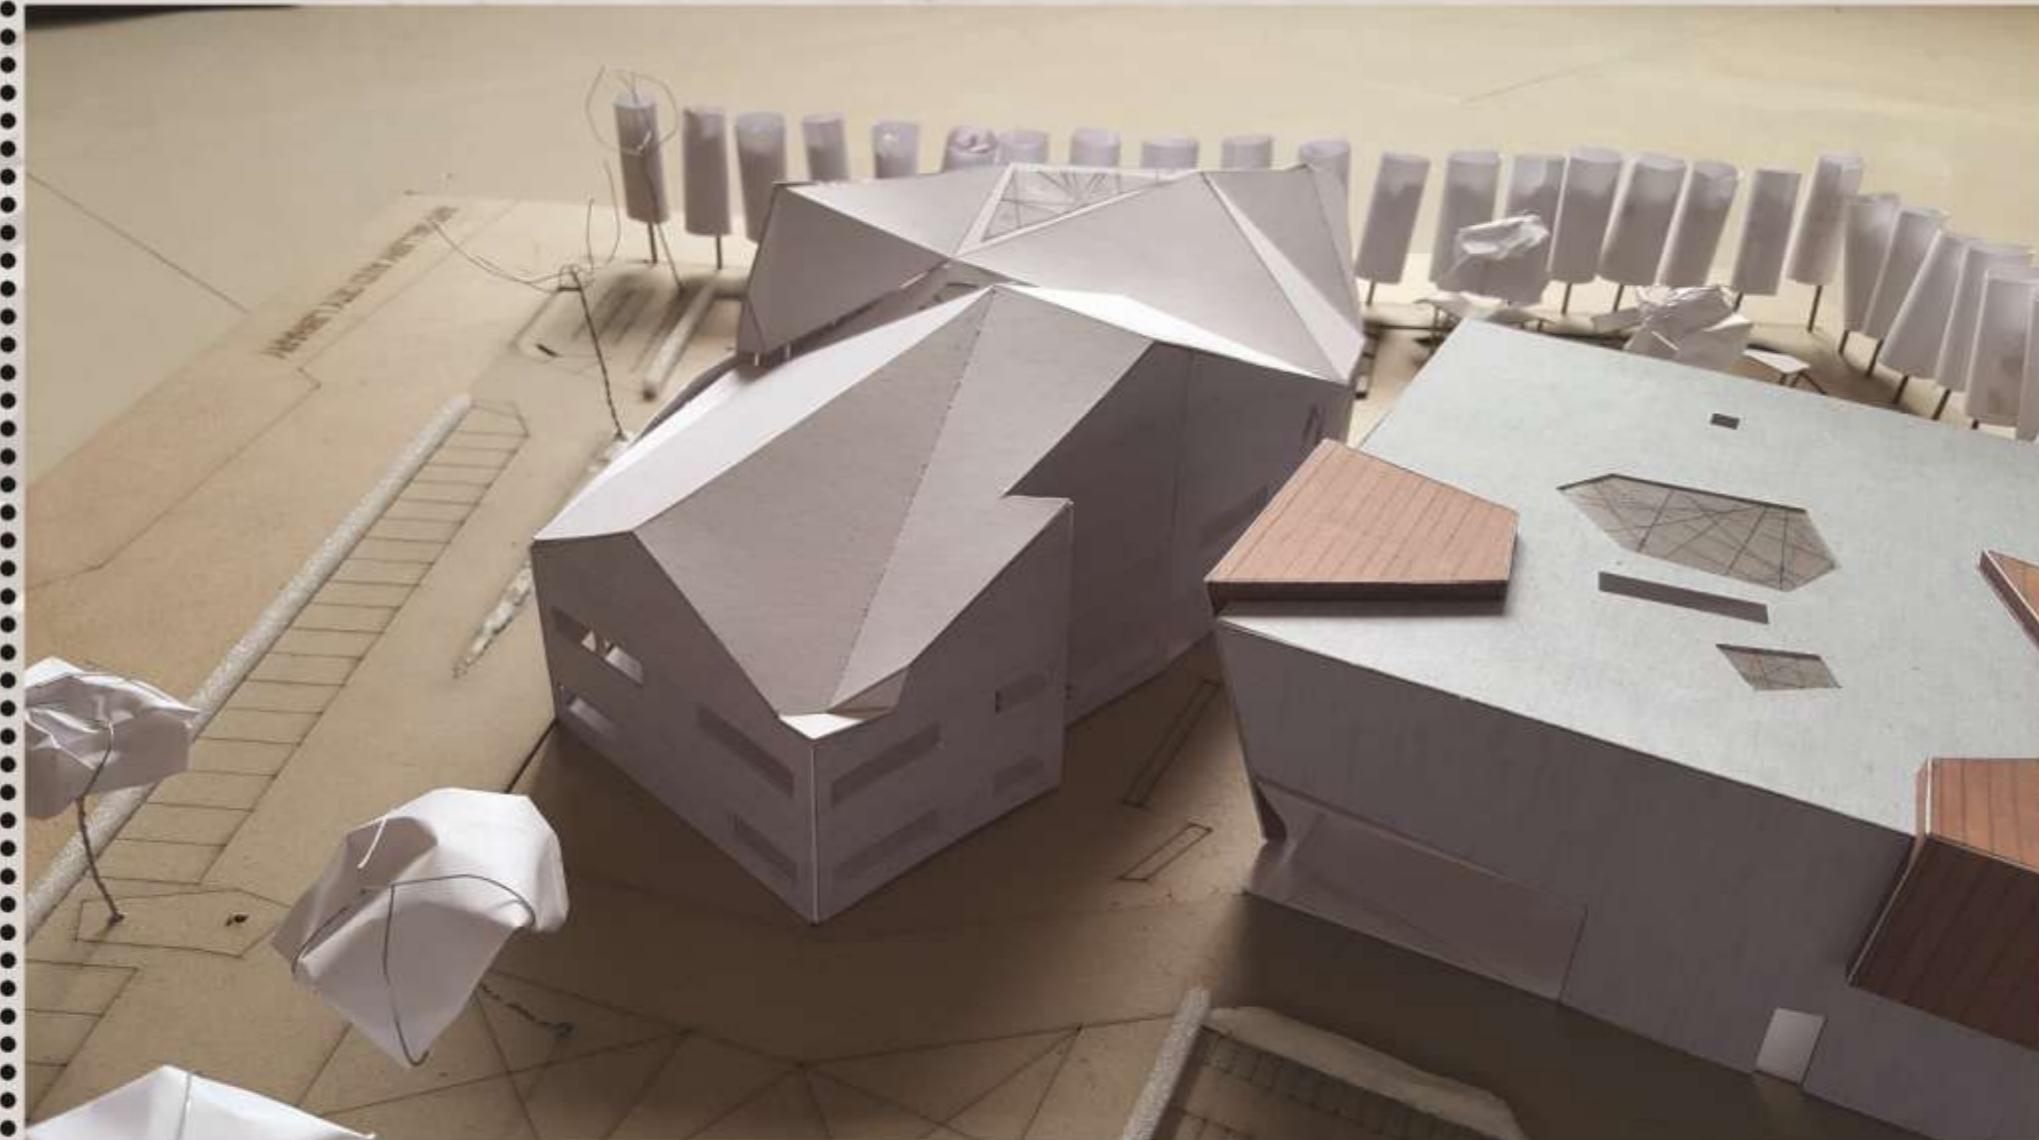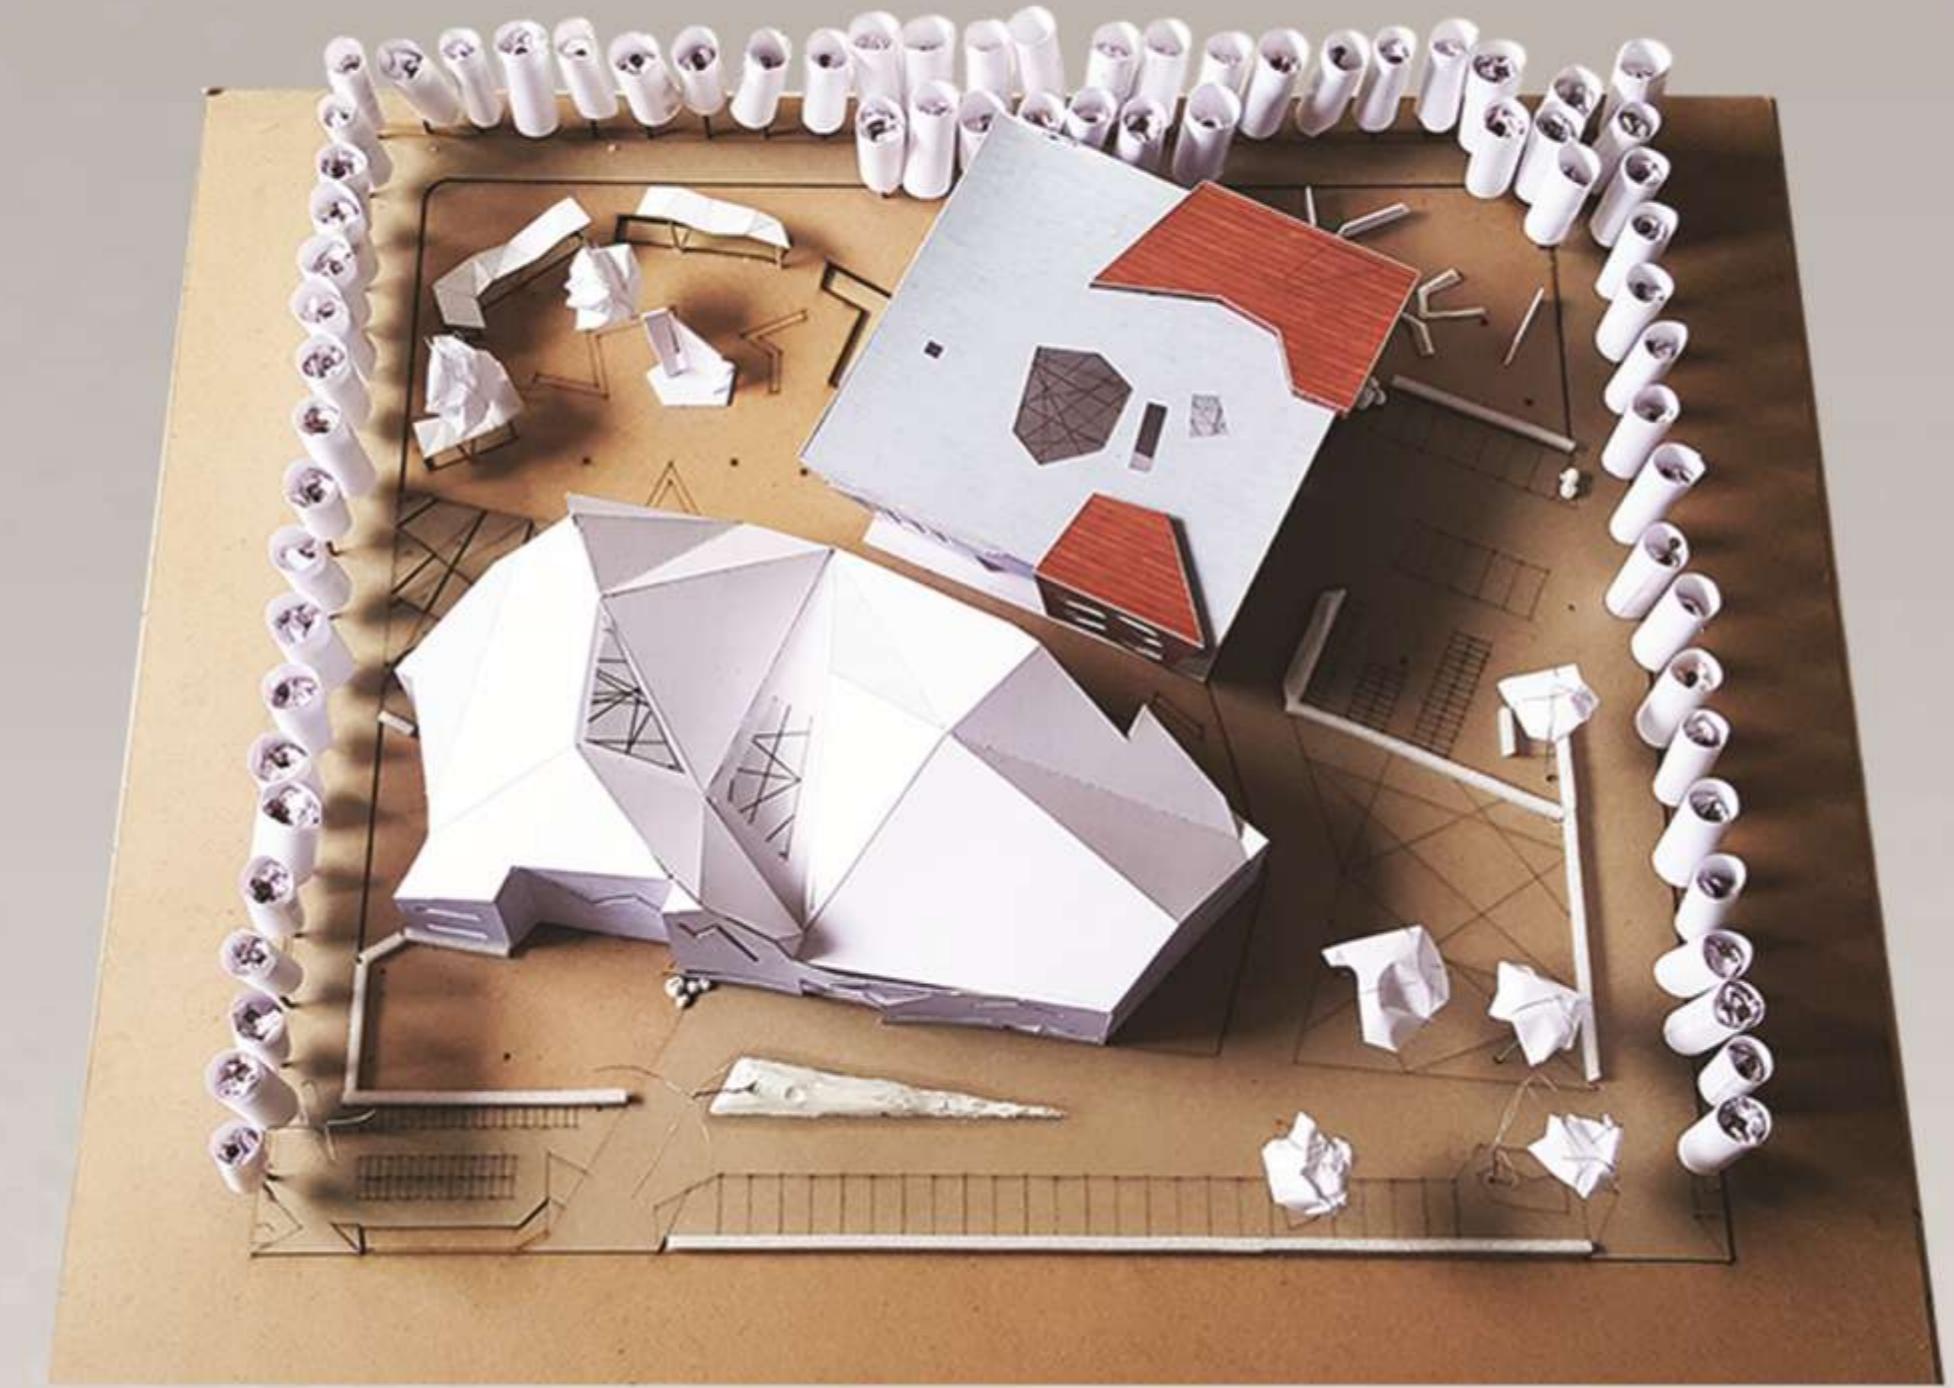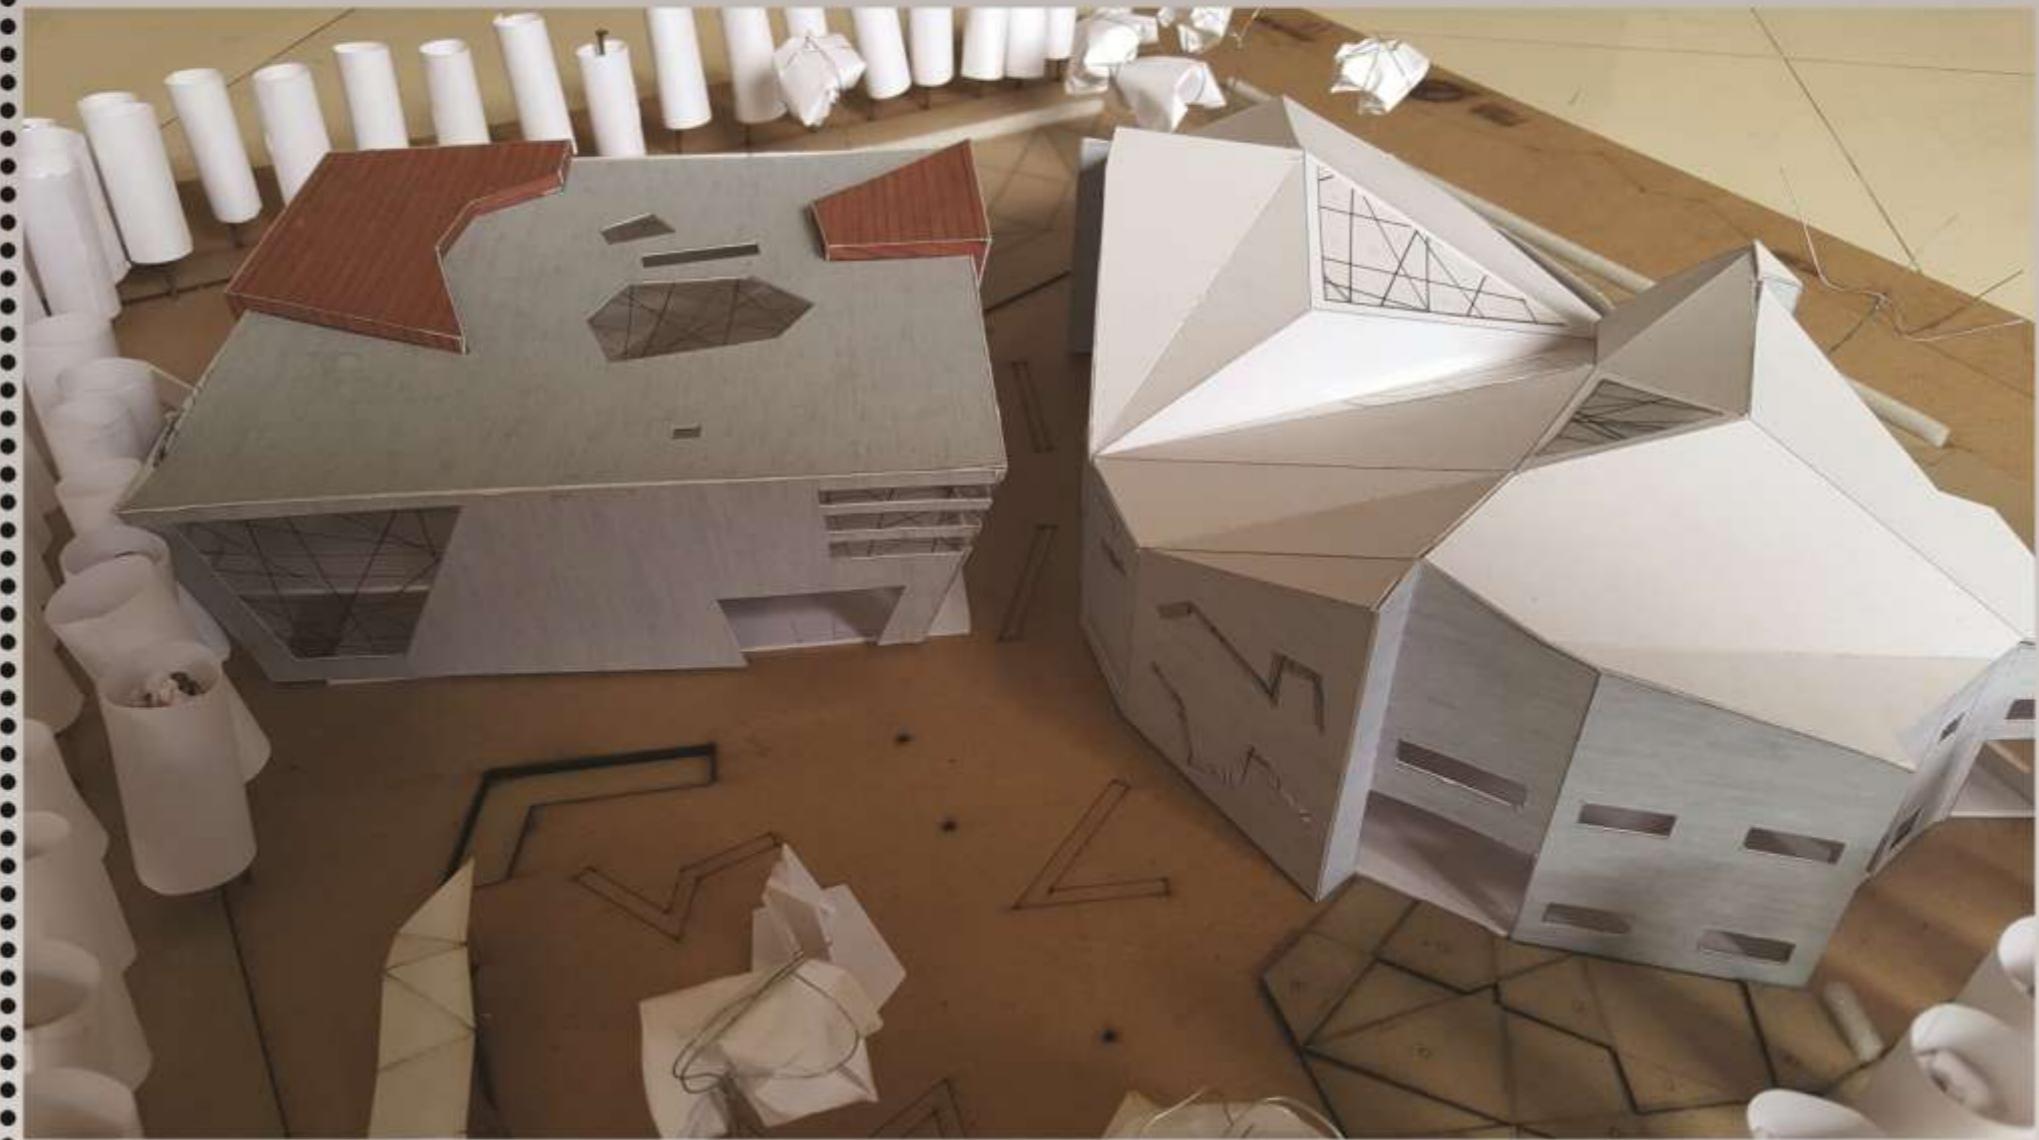

MODEL PICTURES OF ART GALLERY AND CITY LIBRARY.


WINERY RESORT.




PROJECT- WINERY RESORT, AKLUJ, MHARASHTRA.

THE PROGRAM WAS TO DESIGN A WINERY WHICH WOULD ALSO HAVE BOUTIQUE HOTEL TO SERVE THE TOURISTS. THE SITE IS ON A HILLOCK WITH SLOPE IN ALL FOUR DIRECTIONS.

BUILTPUP AREA- 7800 SQ.M


DESIGN APPROACH- THE MOST IMPORTANT FACTOR IN DESIGNING THIS INDUSTRIAL DESIGN PROJECT WAS THE ZONING OF THE SPACES WHICH WAS DONE TO PERFECTION. THE VEHICULAR MOVEMENTS OF THE FACTORY VEHICLES AND OF THE GUESTS IN THE RESORT DOES NOT INTERSECT. THE CLUB HOUSE POSITIONED AT THE TOP MOST POINT OF THE SITE THE INFINITY THEME TO IT & ALSO LOOKS THE BOUTIQUE HOTEL ROOMS. THE HOTELS ARE EXQUISITELY DESIGNED AND ARE OF FANCY THEMES, ONE OF WHICH TAKES THE FORM OF A WINE BARREL.

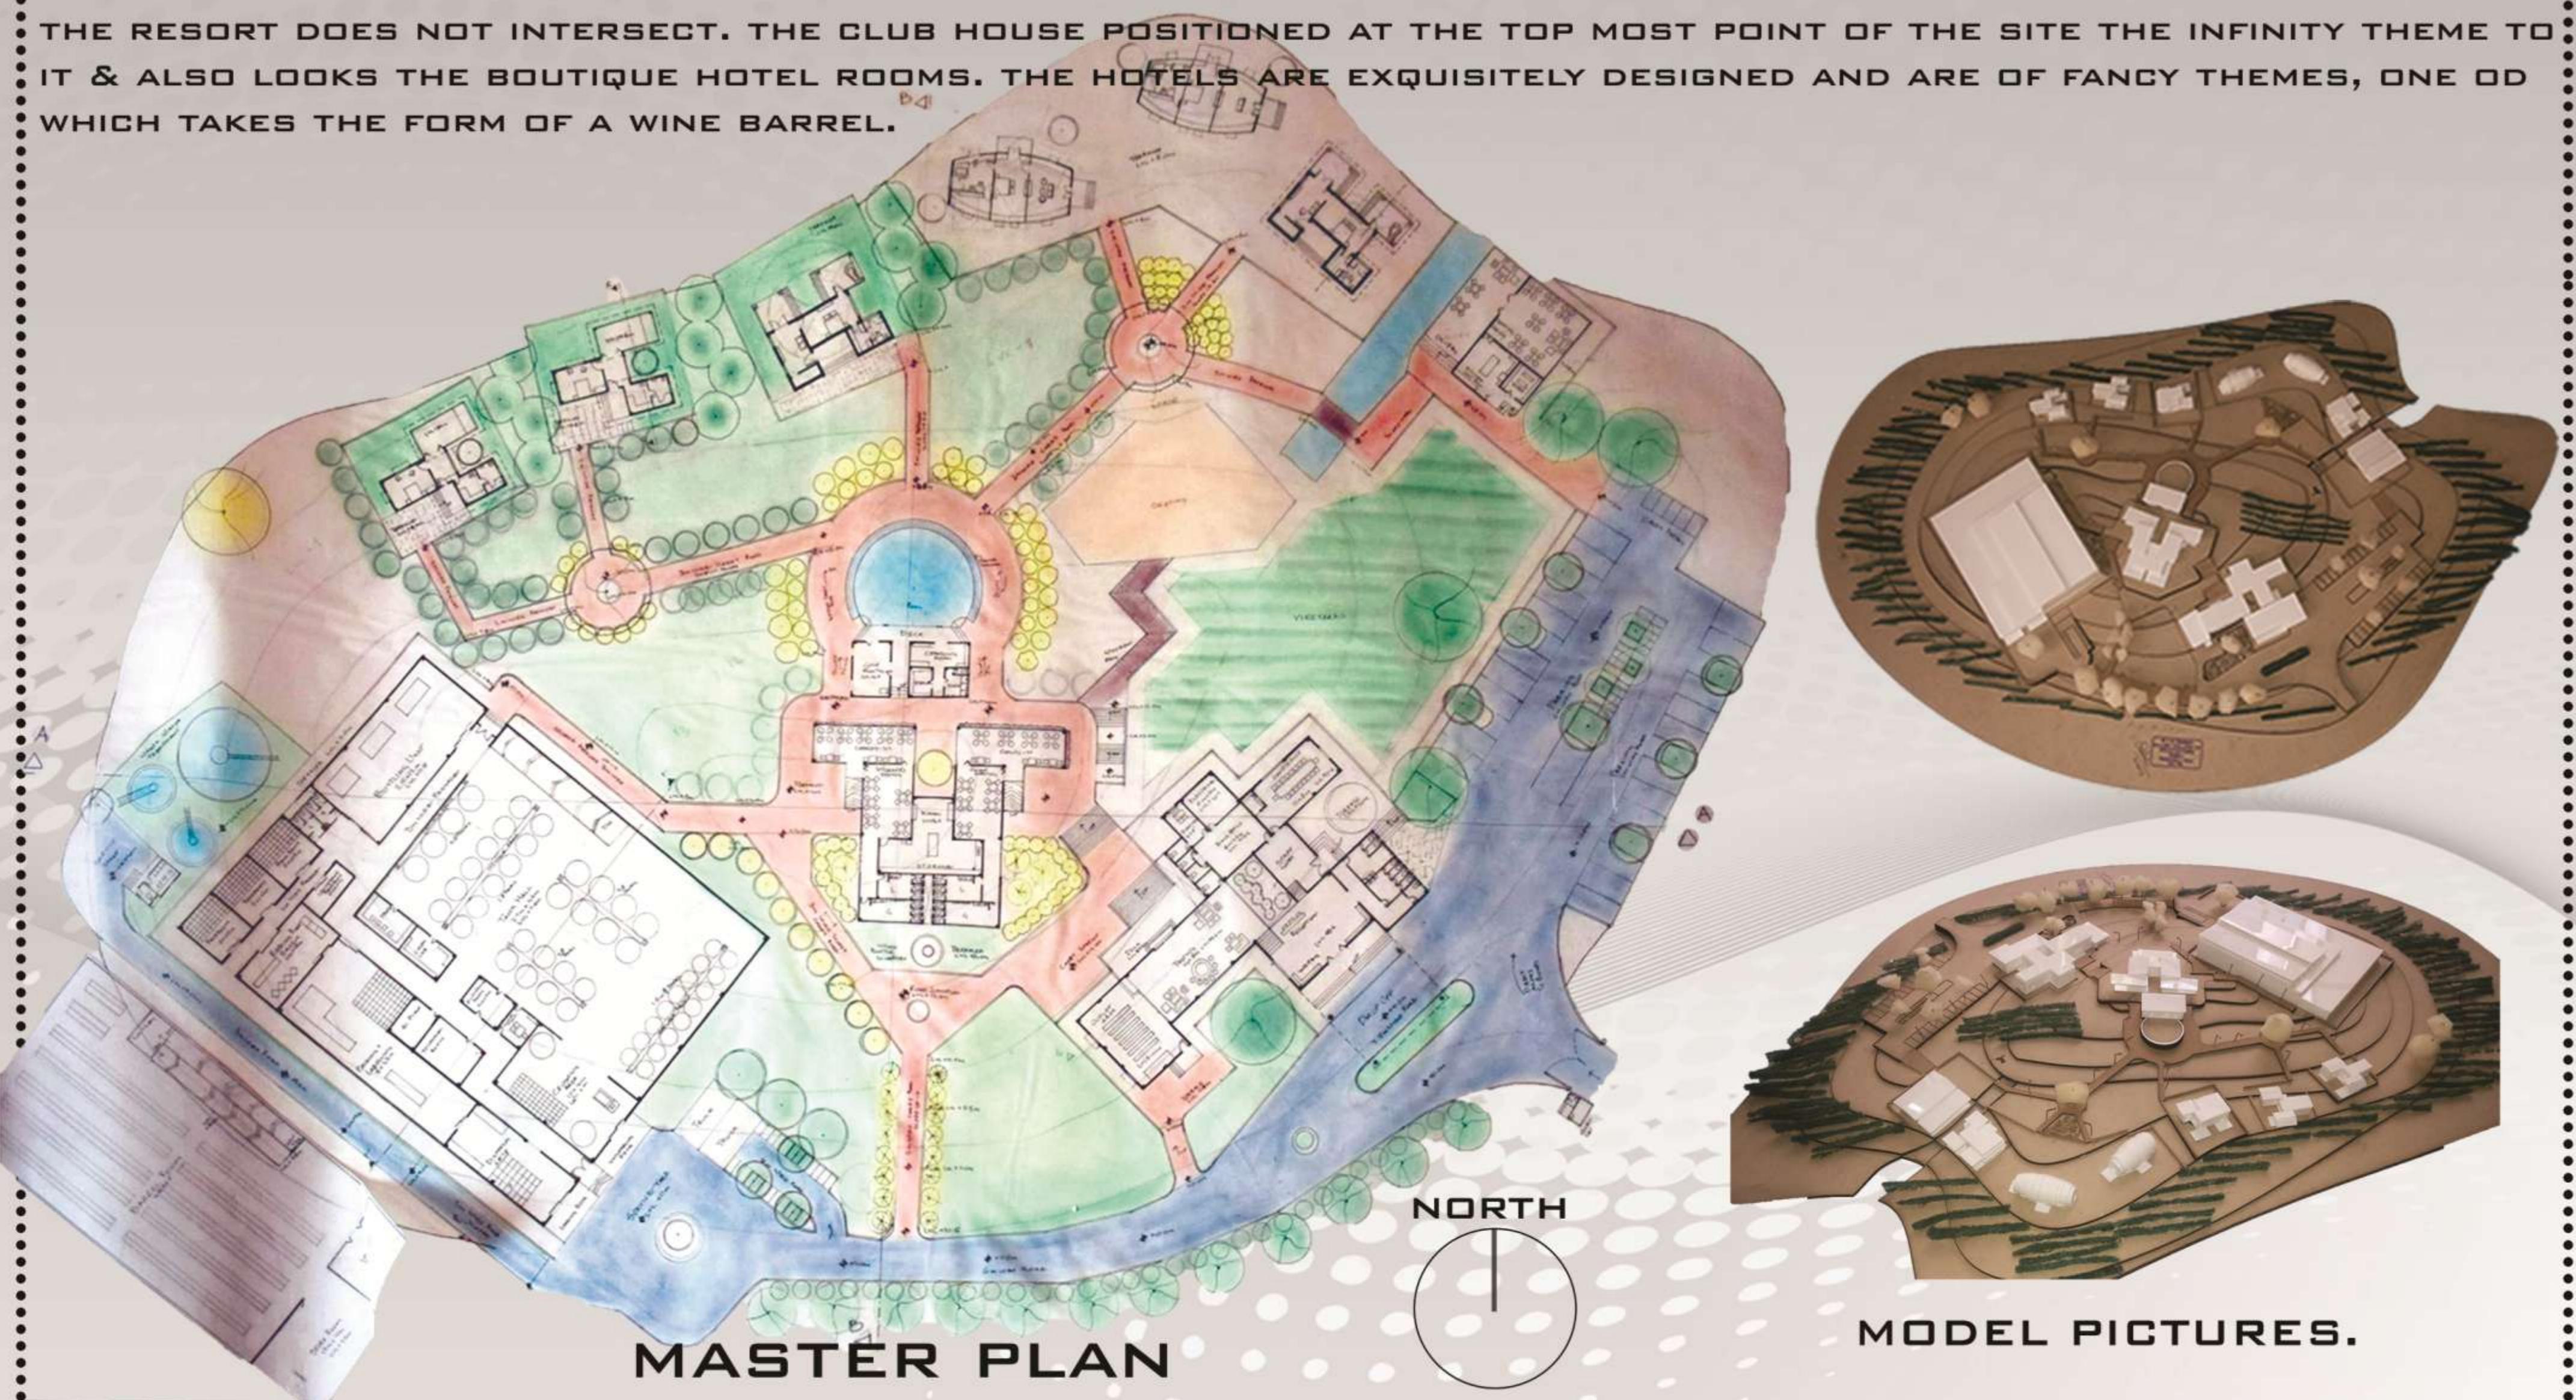

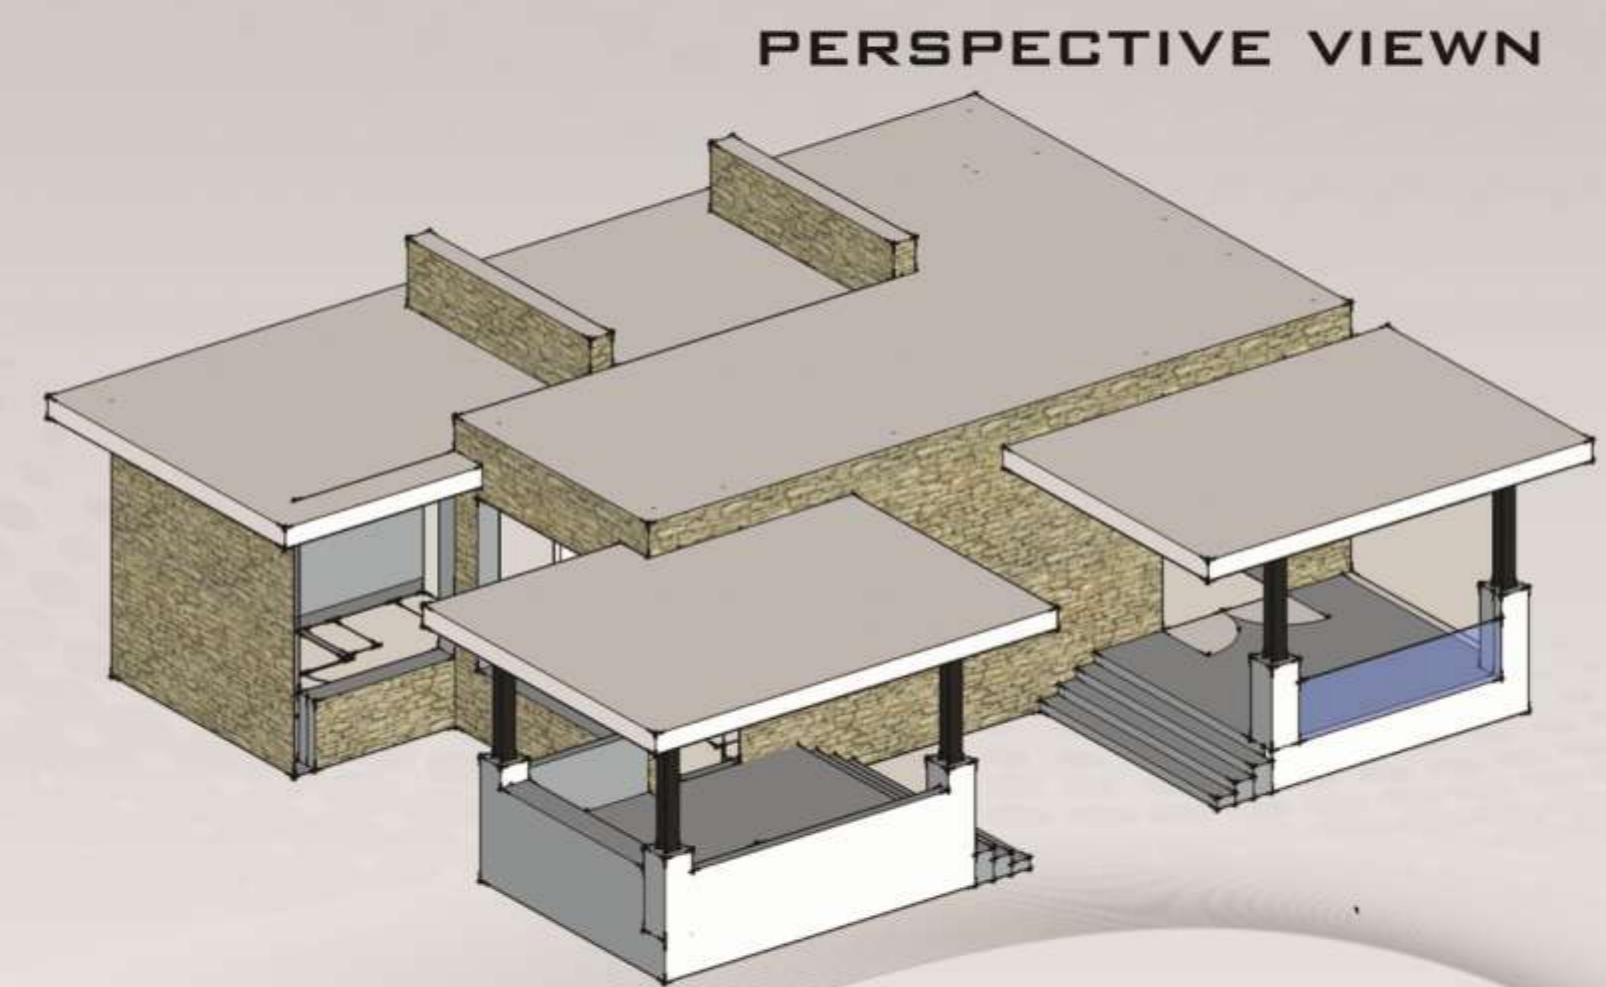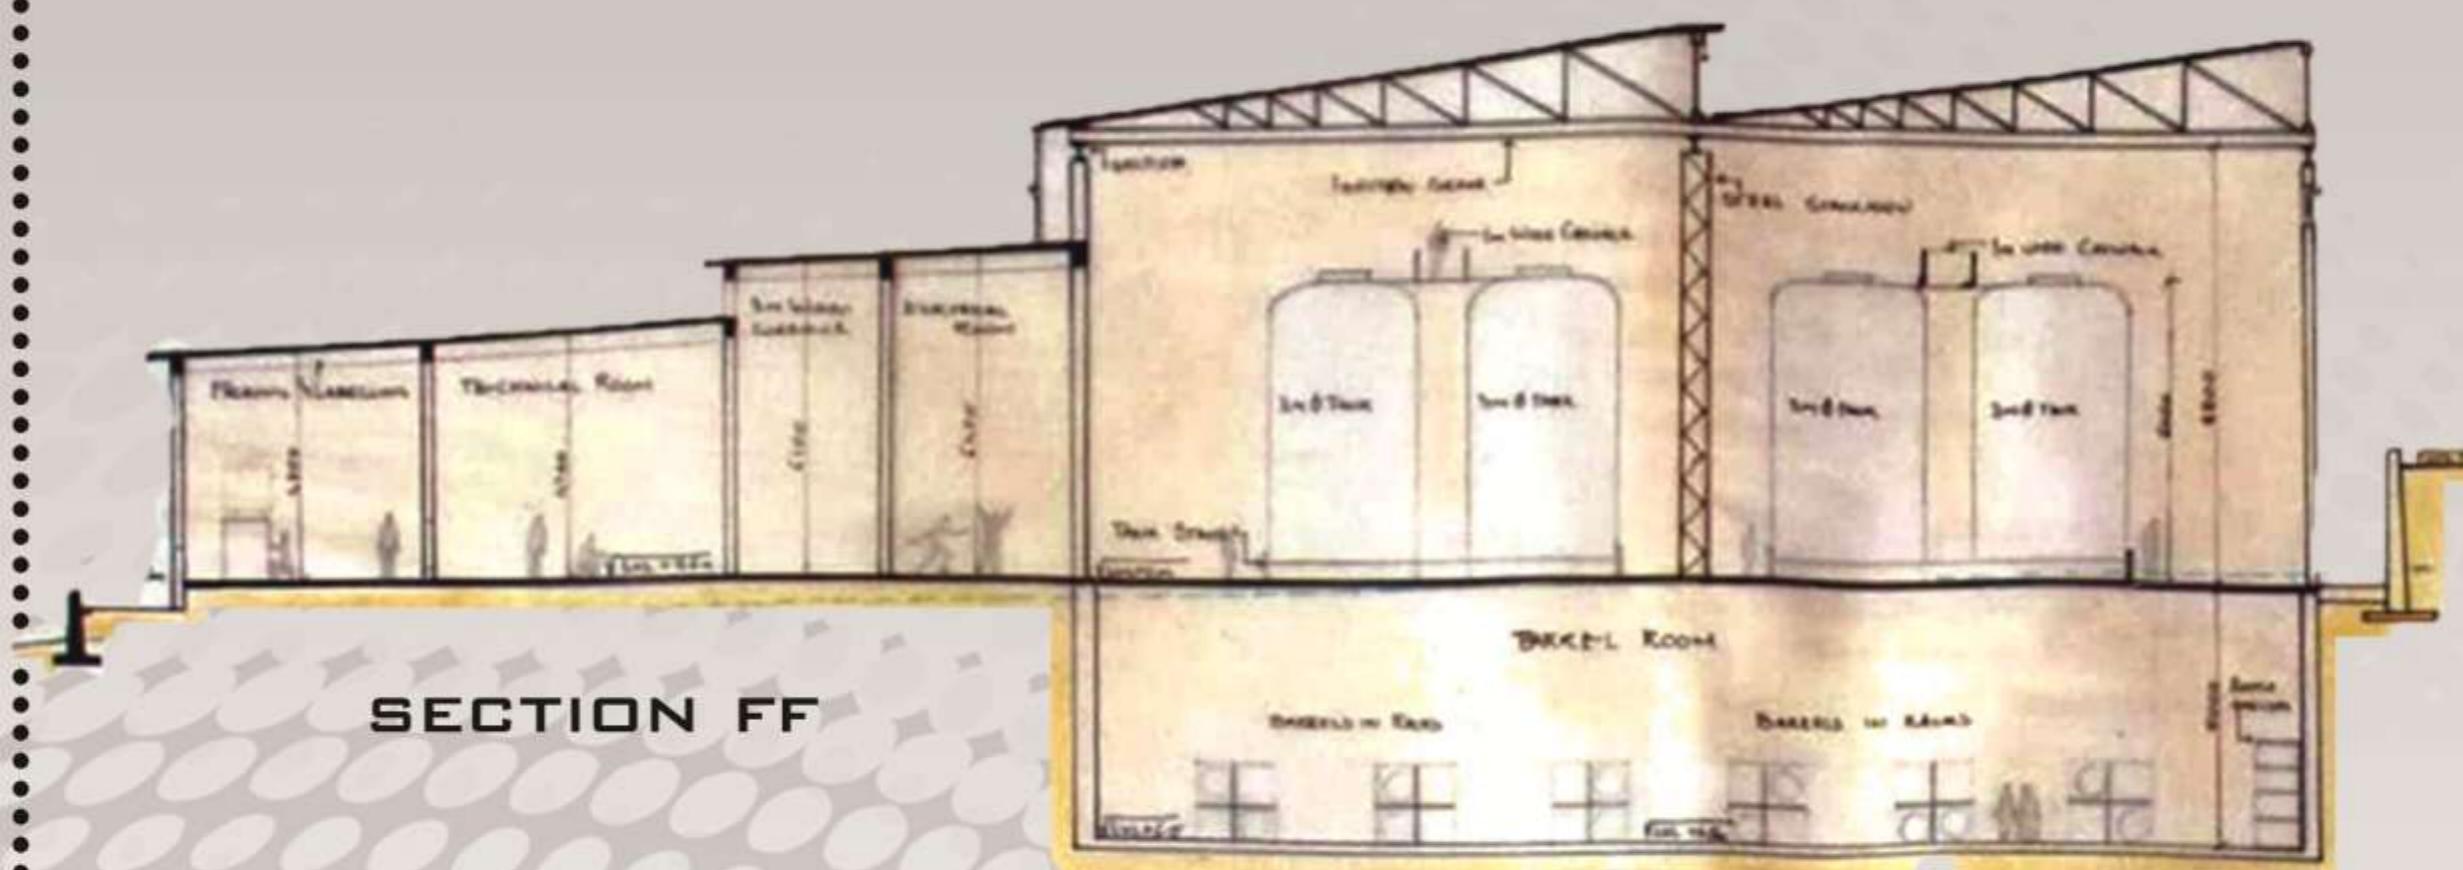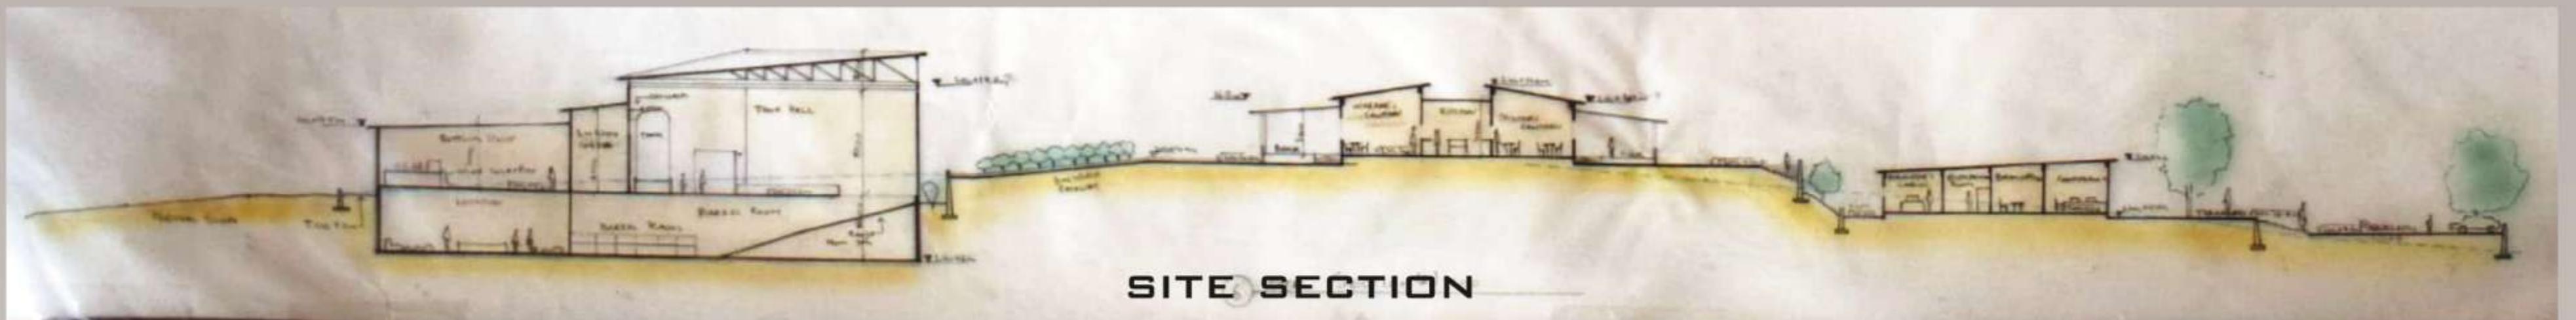


BOUTIQUE HOTEL


UNIT PLAN 1

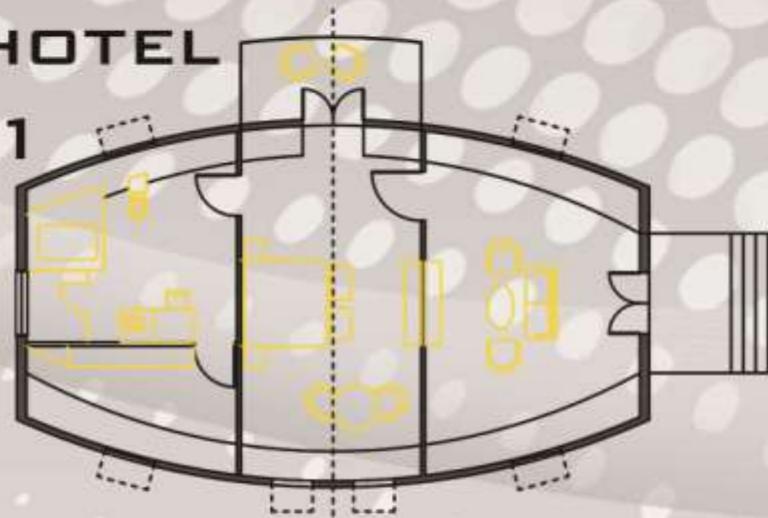


ELEVATION

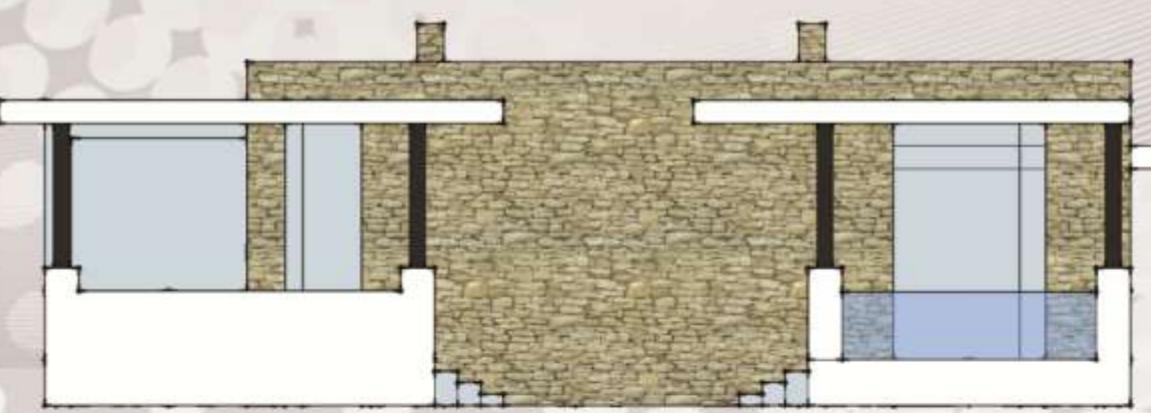


ELEVATION

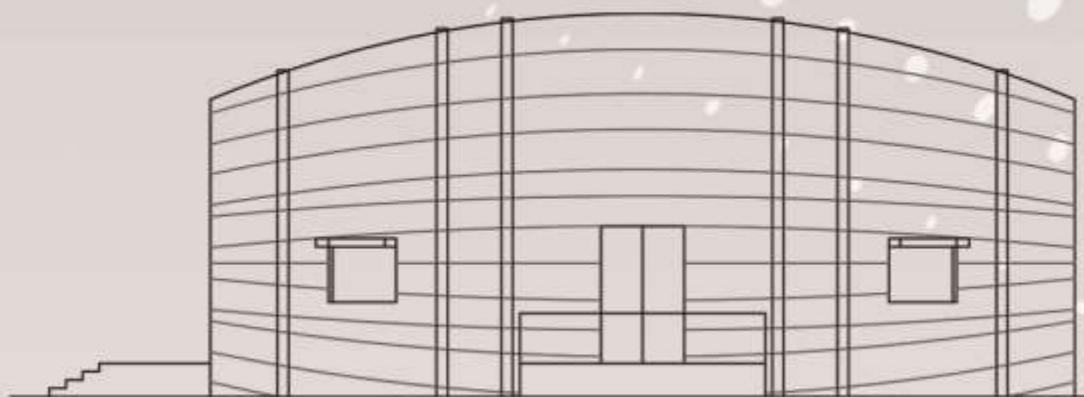

BOUTIQUE HOTEL
UNIT PLAN 2

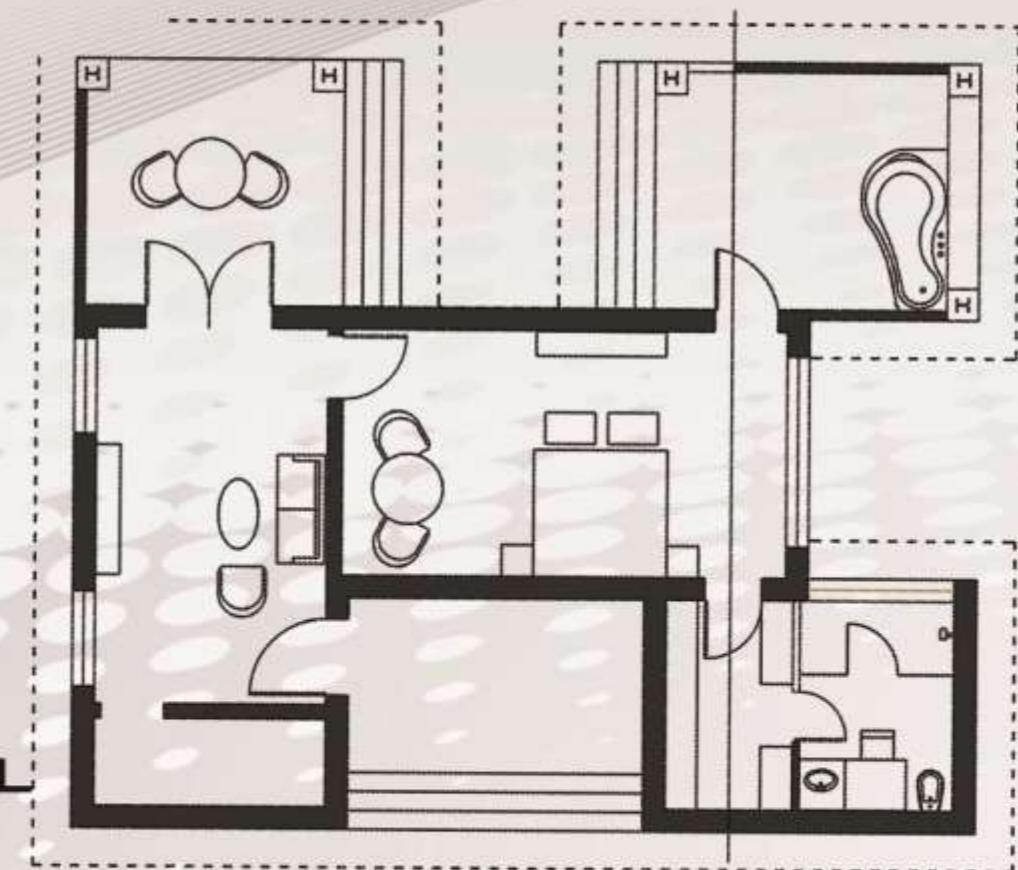


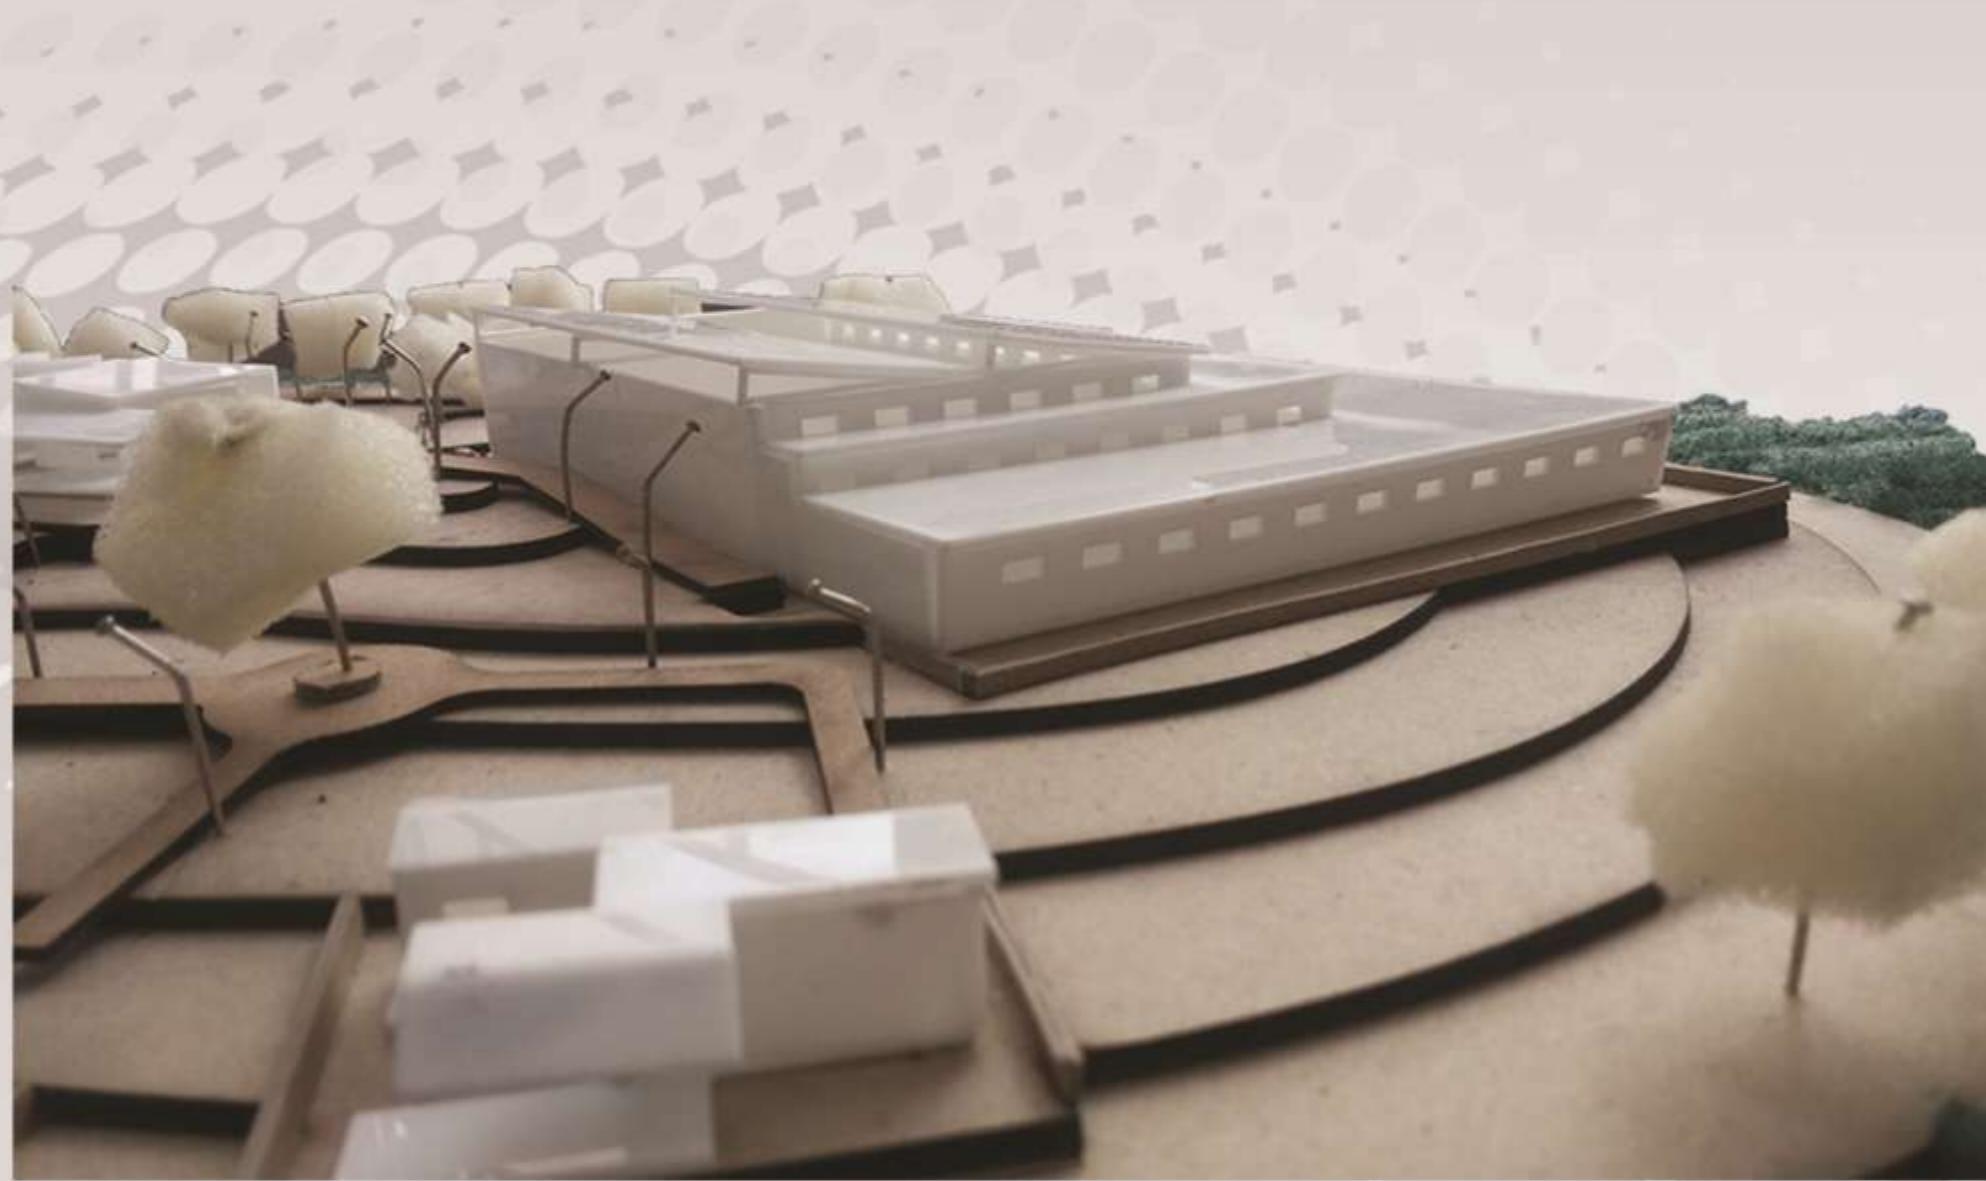


MODEL PICTURES OF WINERY

WORKING DRAWING


BUNGALOW

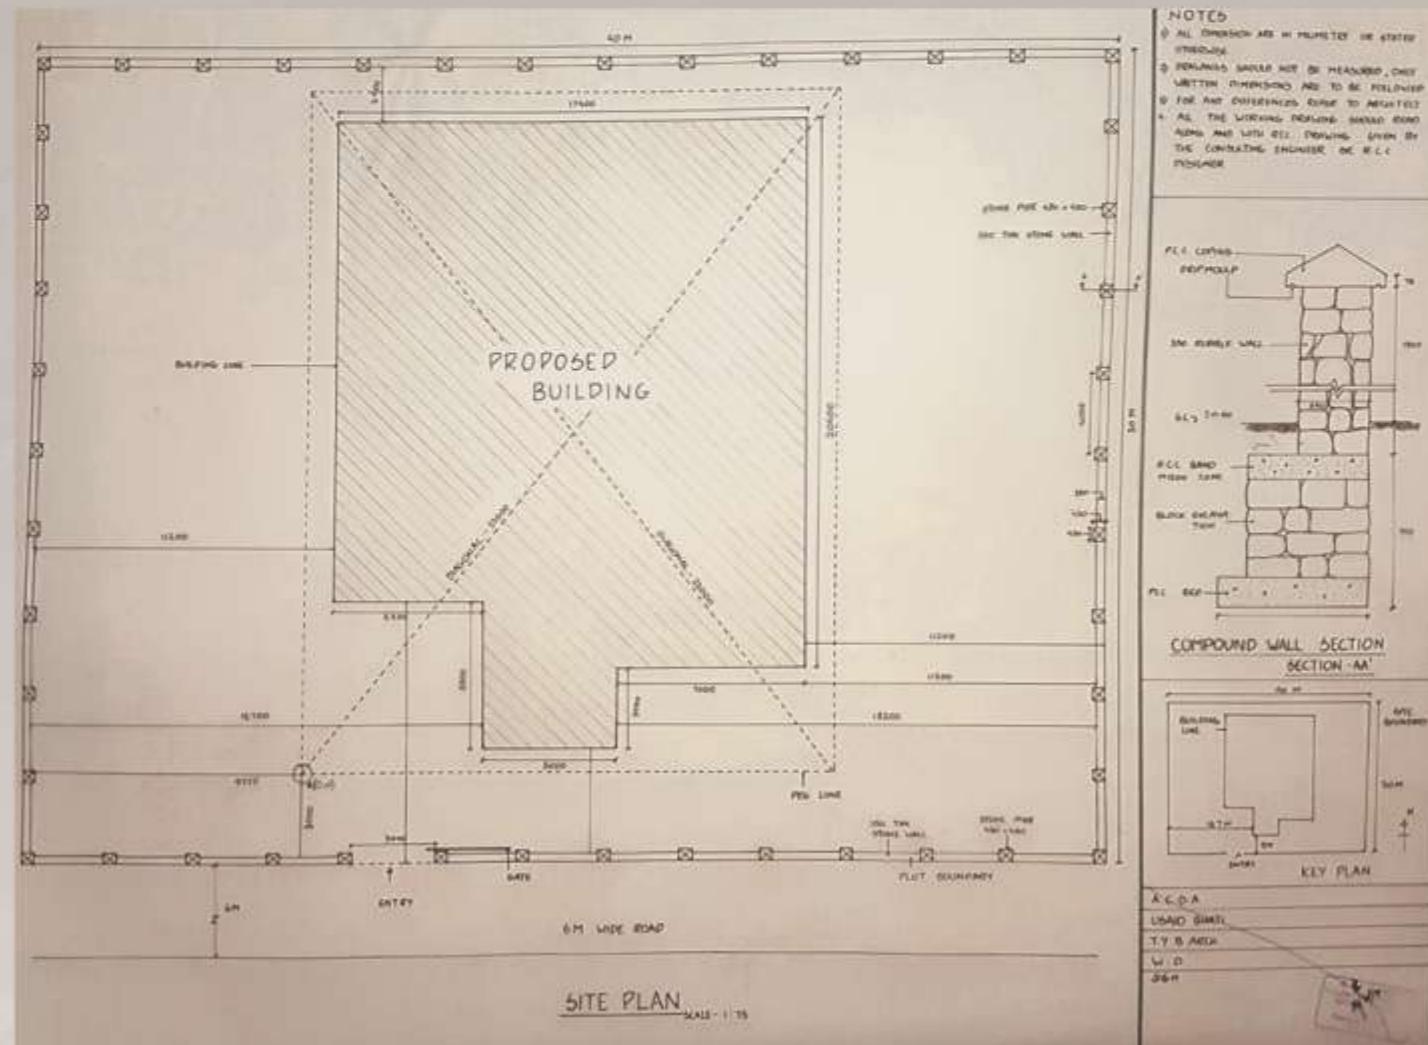

INDUSTRIAL SHED

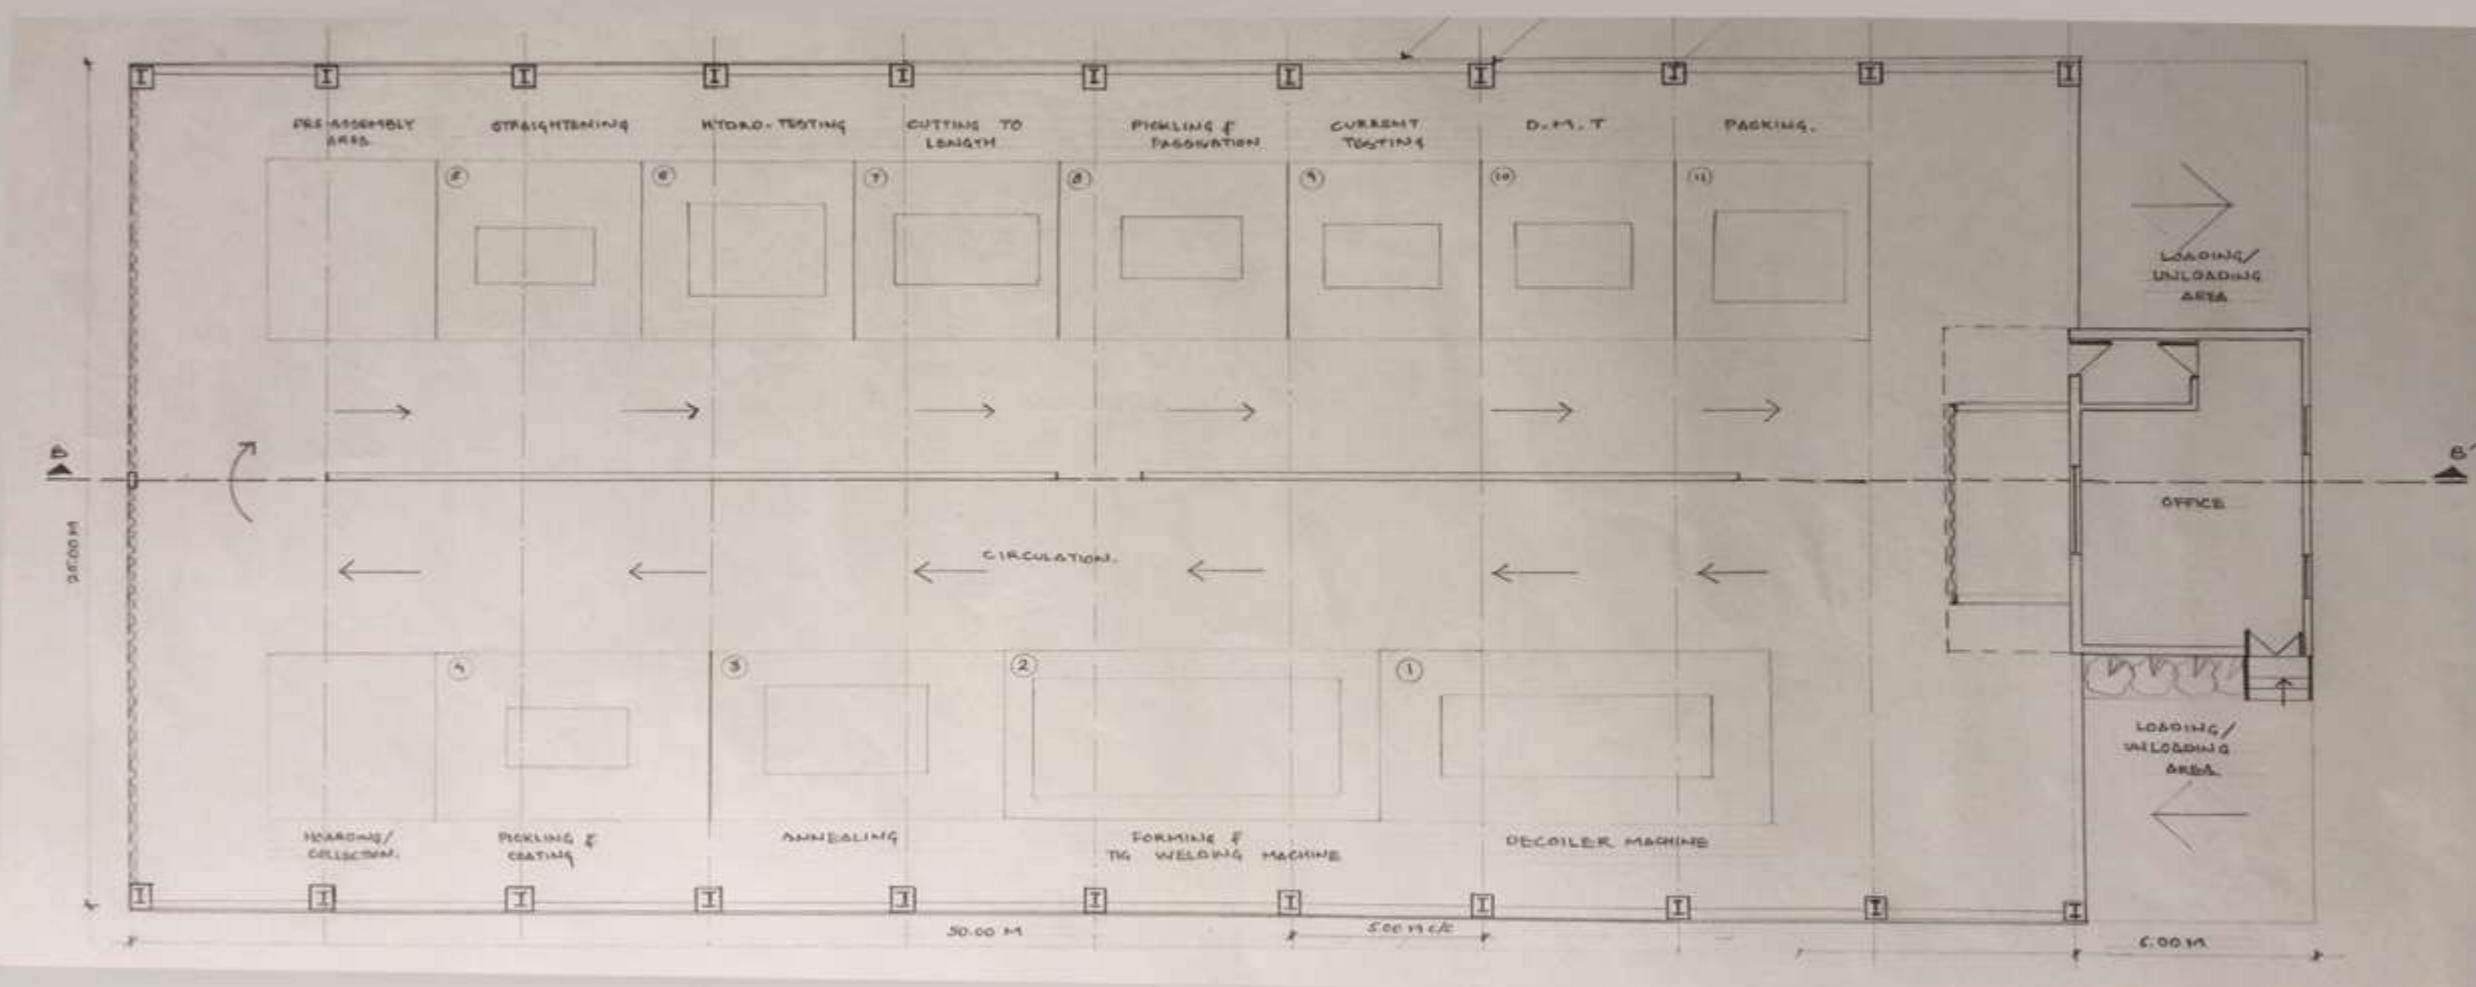


PLAN


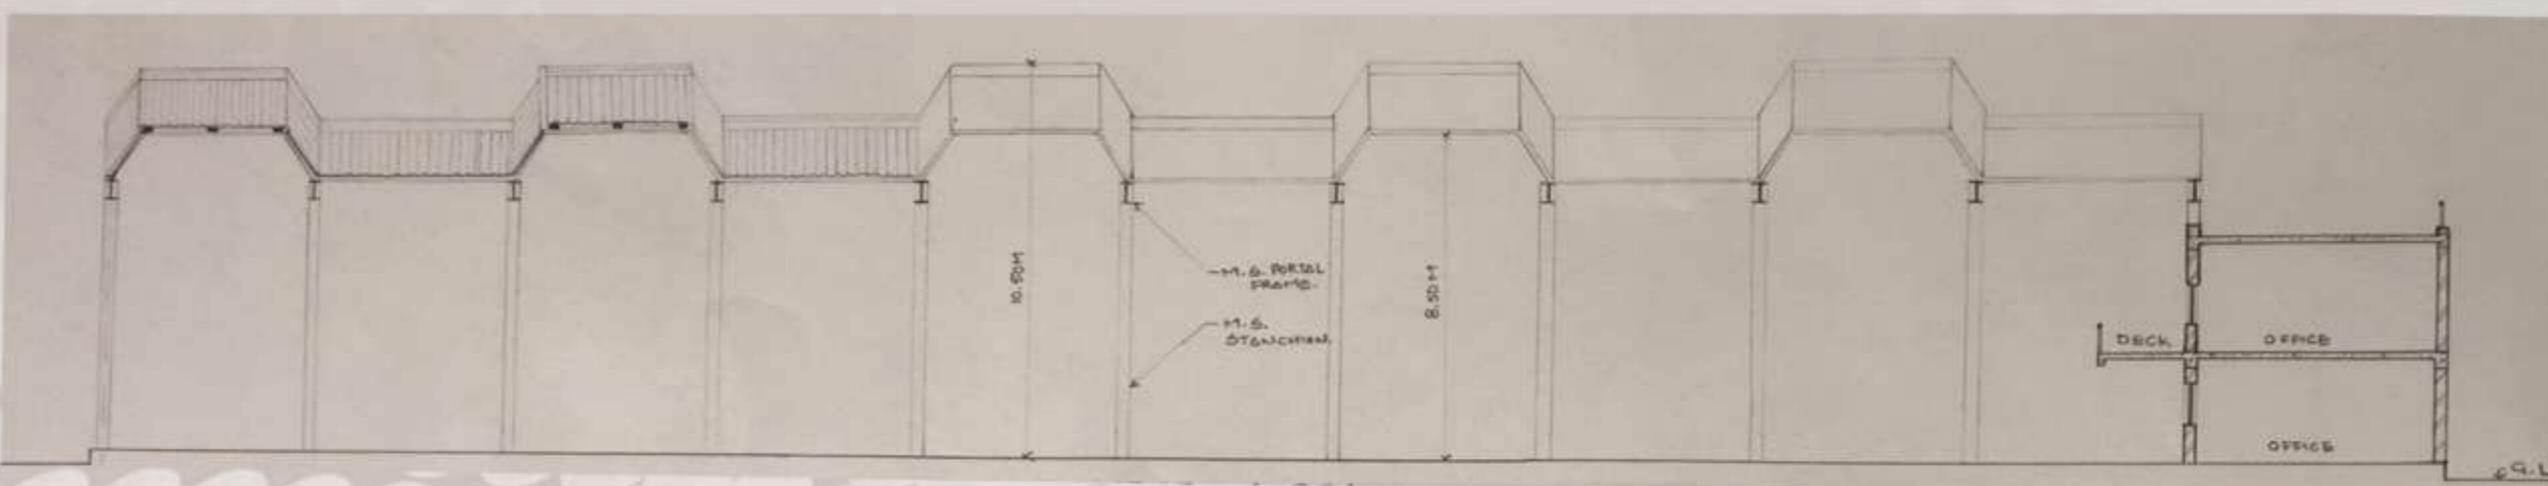


SECTION BB


PORTAL FRAME DETAIL

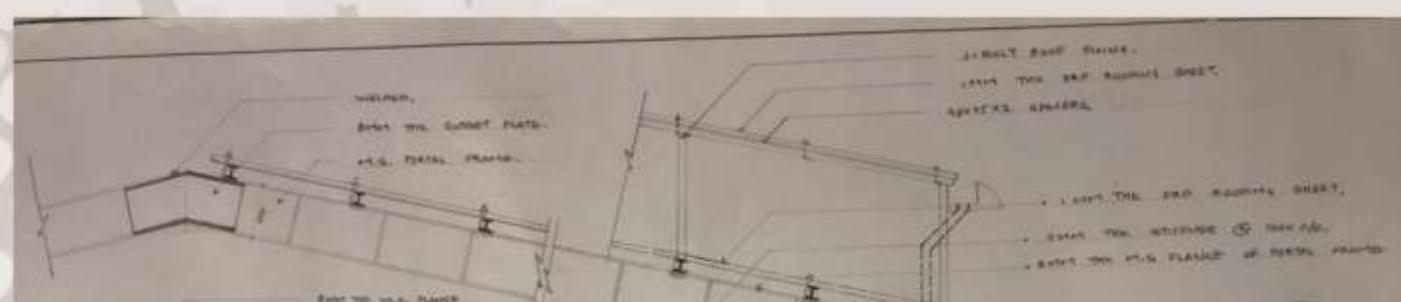

VERTICAL CLADDING FIXING DETAIL

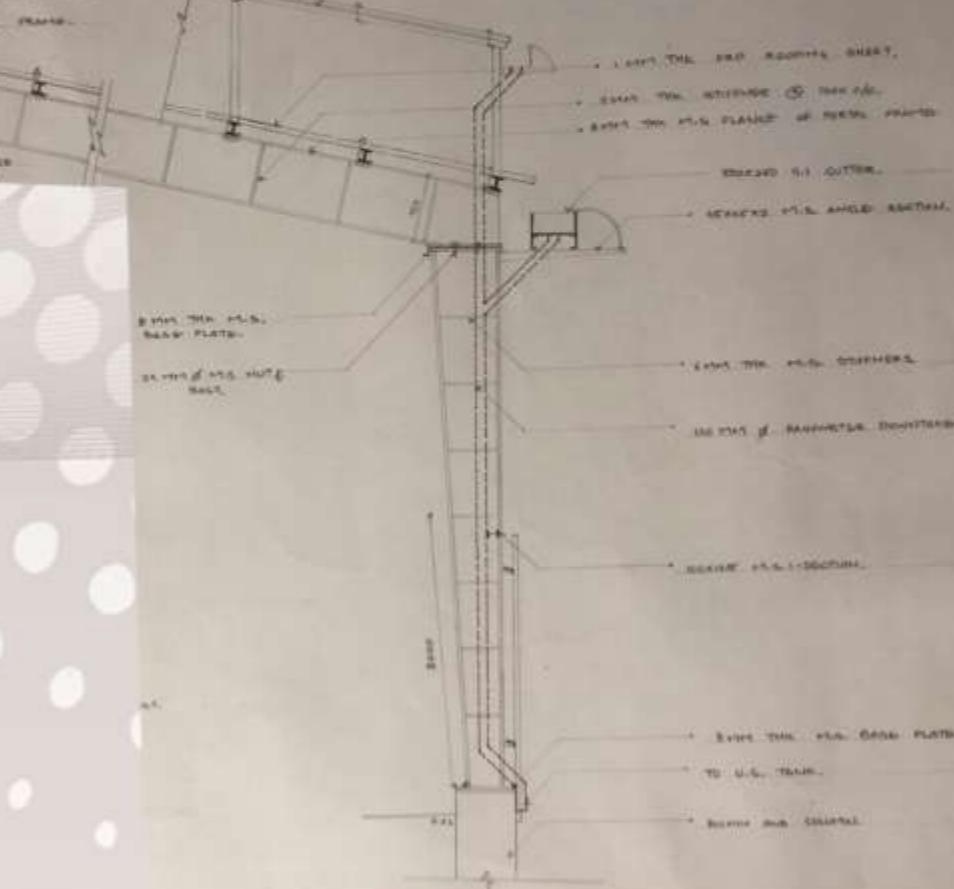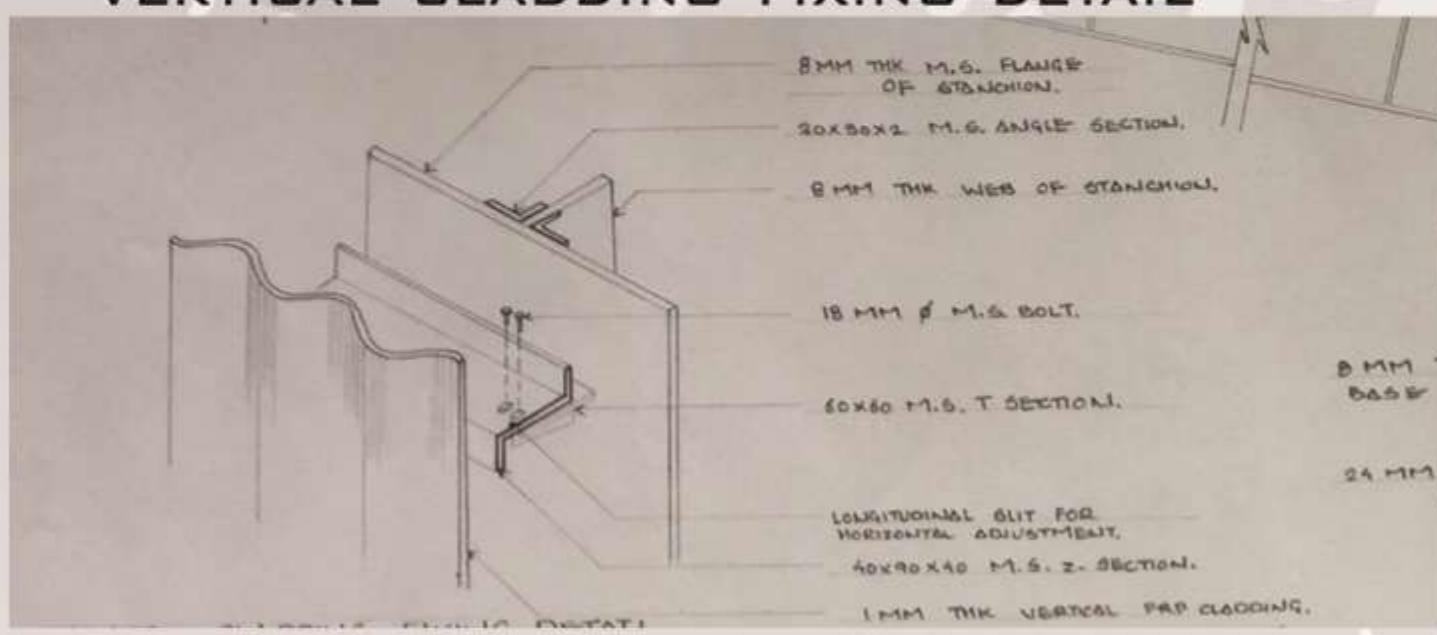

STRUCTURAL PLAN

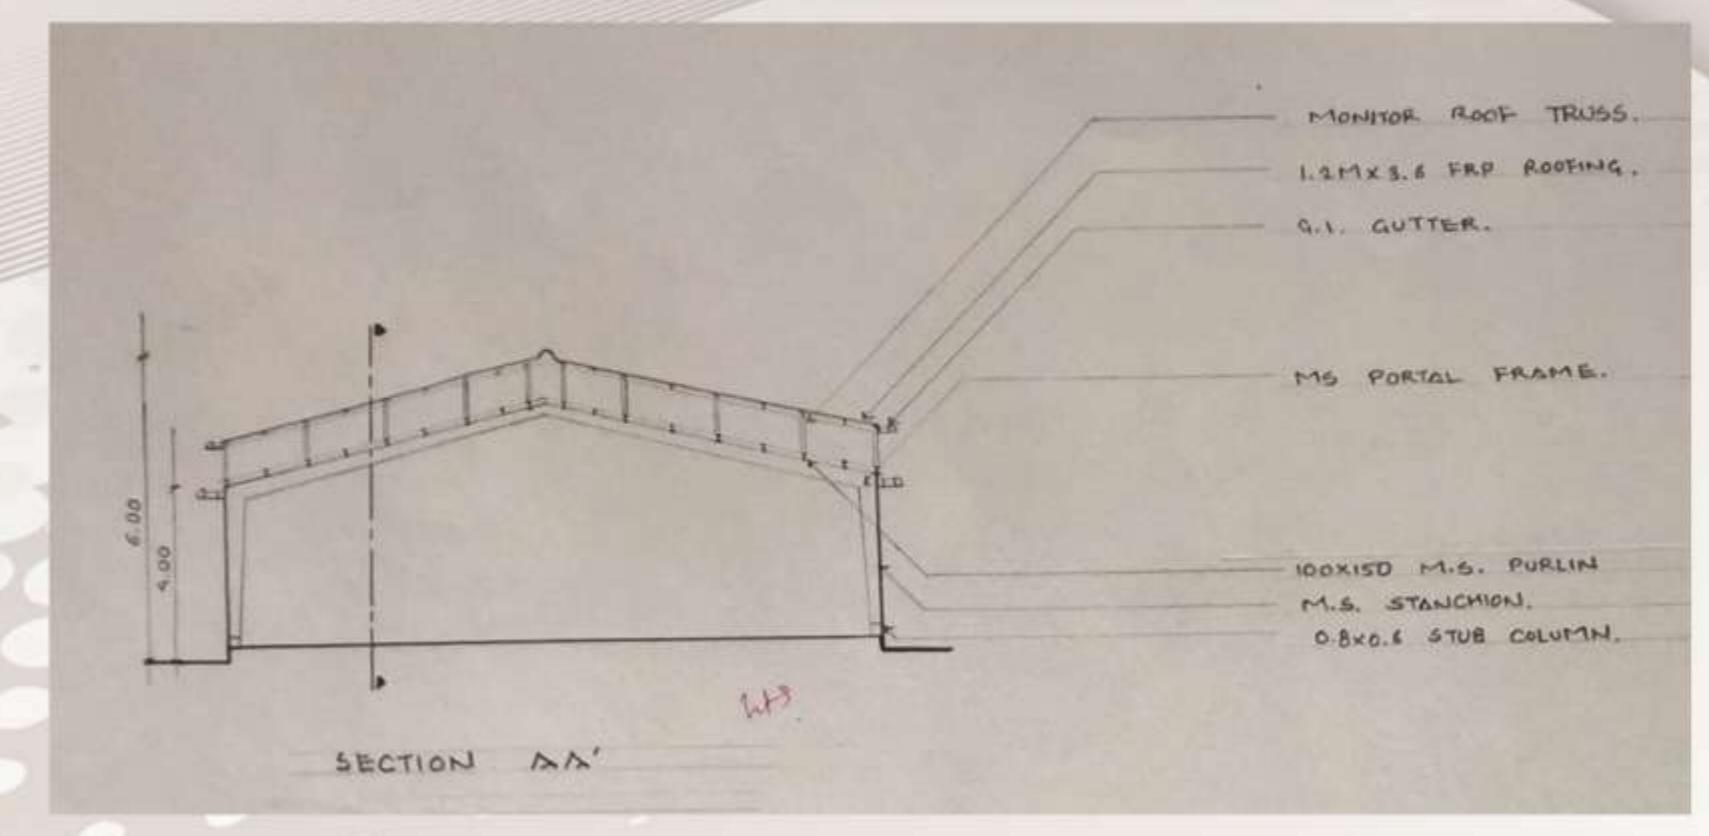

SECTION AA



THANK YOU.